

P O R  
T F O  
L I O

## CONTACTS

- +44 7867231218
- jeniscarvalho123@gmail.com
- <https://www.linkedin.com/in/jenisa-carvalho>
- London, United Kingdom

## EDUCATION

### Middlesex University, London

Masters in Interior Architecture  
2022 - 2023

### Aditya College of Architecture, Mumbai

Bachelors Degree in Interior Design  
2019 - 2022

## SKILLS

### HARD SKILLS:

- Space planning
- Rendering
- Material Selection
- Mood Boards
- Design process
- Image Manipulation

## TOOLS

- AutoCAD 2D
- SketchUp
- InDesign
- Adobe Photoshop
- Illustrator
- Enscape
- Microsoft office Suite (Excel, Word, PowerPoint)
- Adobe Creative Suite

## INTERPERSONAL SKILLS

- Implemented time management techniques, successfully balancing workload and meeting deadlines for multiple projects; reduced time spent on non-essential tasks by 30% without compromising work quality.
- Strong communication skills for collaborating with team members, conveying technical concepts to non-technical stakeholders, and participating in meetings effectively.
- Ability to quickly learn new technologies, tools, and methodologies, and adapt to changing project needs.

# JENISA CARVALHO

## Interior Architect

### PROFILE

- Enthusiastic Interior Design professional with almost 1 year of industry experience of designing innovative, functional space focused to create well-balanced and visually appealing environments.
- Proficiency in design software such as AutoCAD, SketchUp, rendering, delivering client presentations and producing key relationships to grow customer service orientation.

### WORK EXPERIENCE

#### Sneha Interior and Exterior, Mumbai, India Nov 2021-March 2022

##### Assistant interior designer

- Led on space planning projects.
- Created AutoCAD Layout and SketchUp drawings for clients.
- Developed key client interaction relationships by providing design solutions that met needs and budget without compromising quality or design intent.
- Interfaced effectively with design team members, including contractors, vendors and suppliers to resolve issues and discuss ideas and gather feedback.
- Consulted with clients to determine architectural preference to meet overall design goals.

#### Queen Kitchen Décor Co., Mumbai, India Nov 2018-May 2019

##### Assistant Interior designer

- Conducted on-site measurements by ensuring seamless integration of design elements, which led to a 19% decrease in construction errors.
- Coordinated with furniture, tiles selection and documentation of specifications.
- Prepared design presentations, including 2D and 3D visualizations, illustrations, mood boards, and material sourcing for Bathrooms/Kitchen.

### PROJECTS

#### Gardening for elderly in Kingsgate community center (Masters Thesis)

- The Project "GROW TOGETHER" at Kingsgate Community Center aims to create an accessible and therapeutic green space for senior citizens.
- This initiative provides a platform to engage in gardening activities, fostering physical and mental well-being while stimulating a sense of community and connection.

#### School for partially impaired children (Bachelors Thesis)

- In an era of inclusivity, it is imperative to ensure that all children, regardless of visual abilities, have access to quality education.
- This thesis delves into the critical realm of inclusive education for partially visually impaired students between the ages of 4 and 7.

### EXTRACURRICULAR ACTIVITIES

- Coordinated with a team of 20 members to organise multiple fest events.
- Collaborated as an Assistant coordinator team security for junior college fest.

# Internship



The proposed residential house, Belonging to an elderly couple, the proposed development fulfils the household requirements as well as includes an independent residential unit which is intended to be put on rent.

Site Area- 776 Sq. m.  
Built Up Area- 276.23 Sq. m.

My contributions to this project include developing drawings and 3D models right from the conceptual stage till the sanction stage, base working drawings and client presentations



ELEVATION 1  
SCALE- 1:200



ELEVATION 2  
SCALE- 1:200




ELEVATION 3  
SCALE- 1:200



North- East View towards Studio, Master Bedroom & the Deck joining both spaces



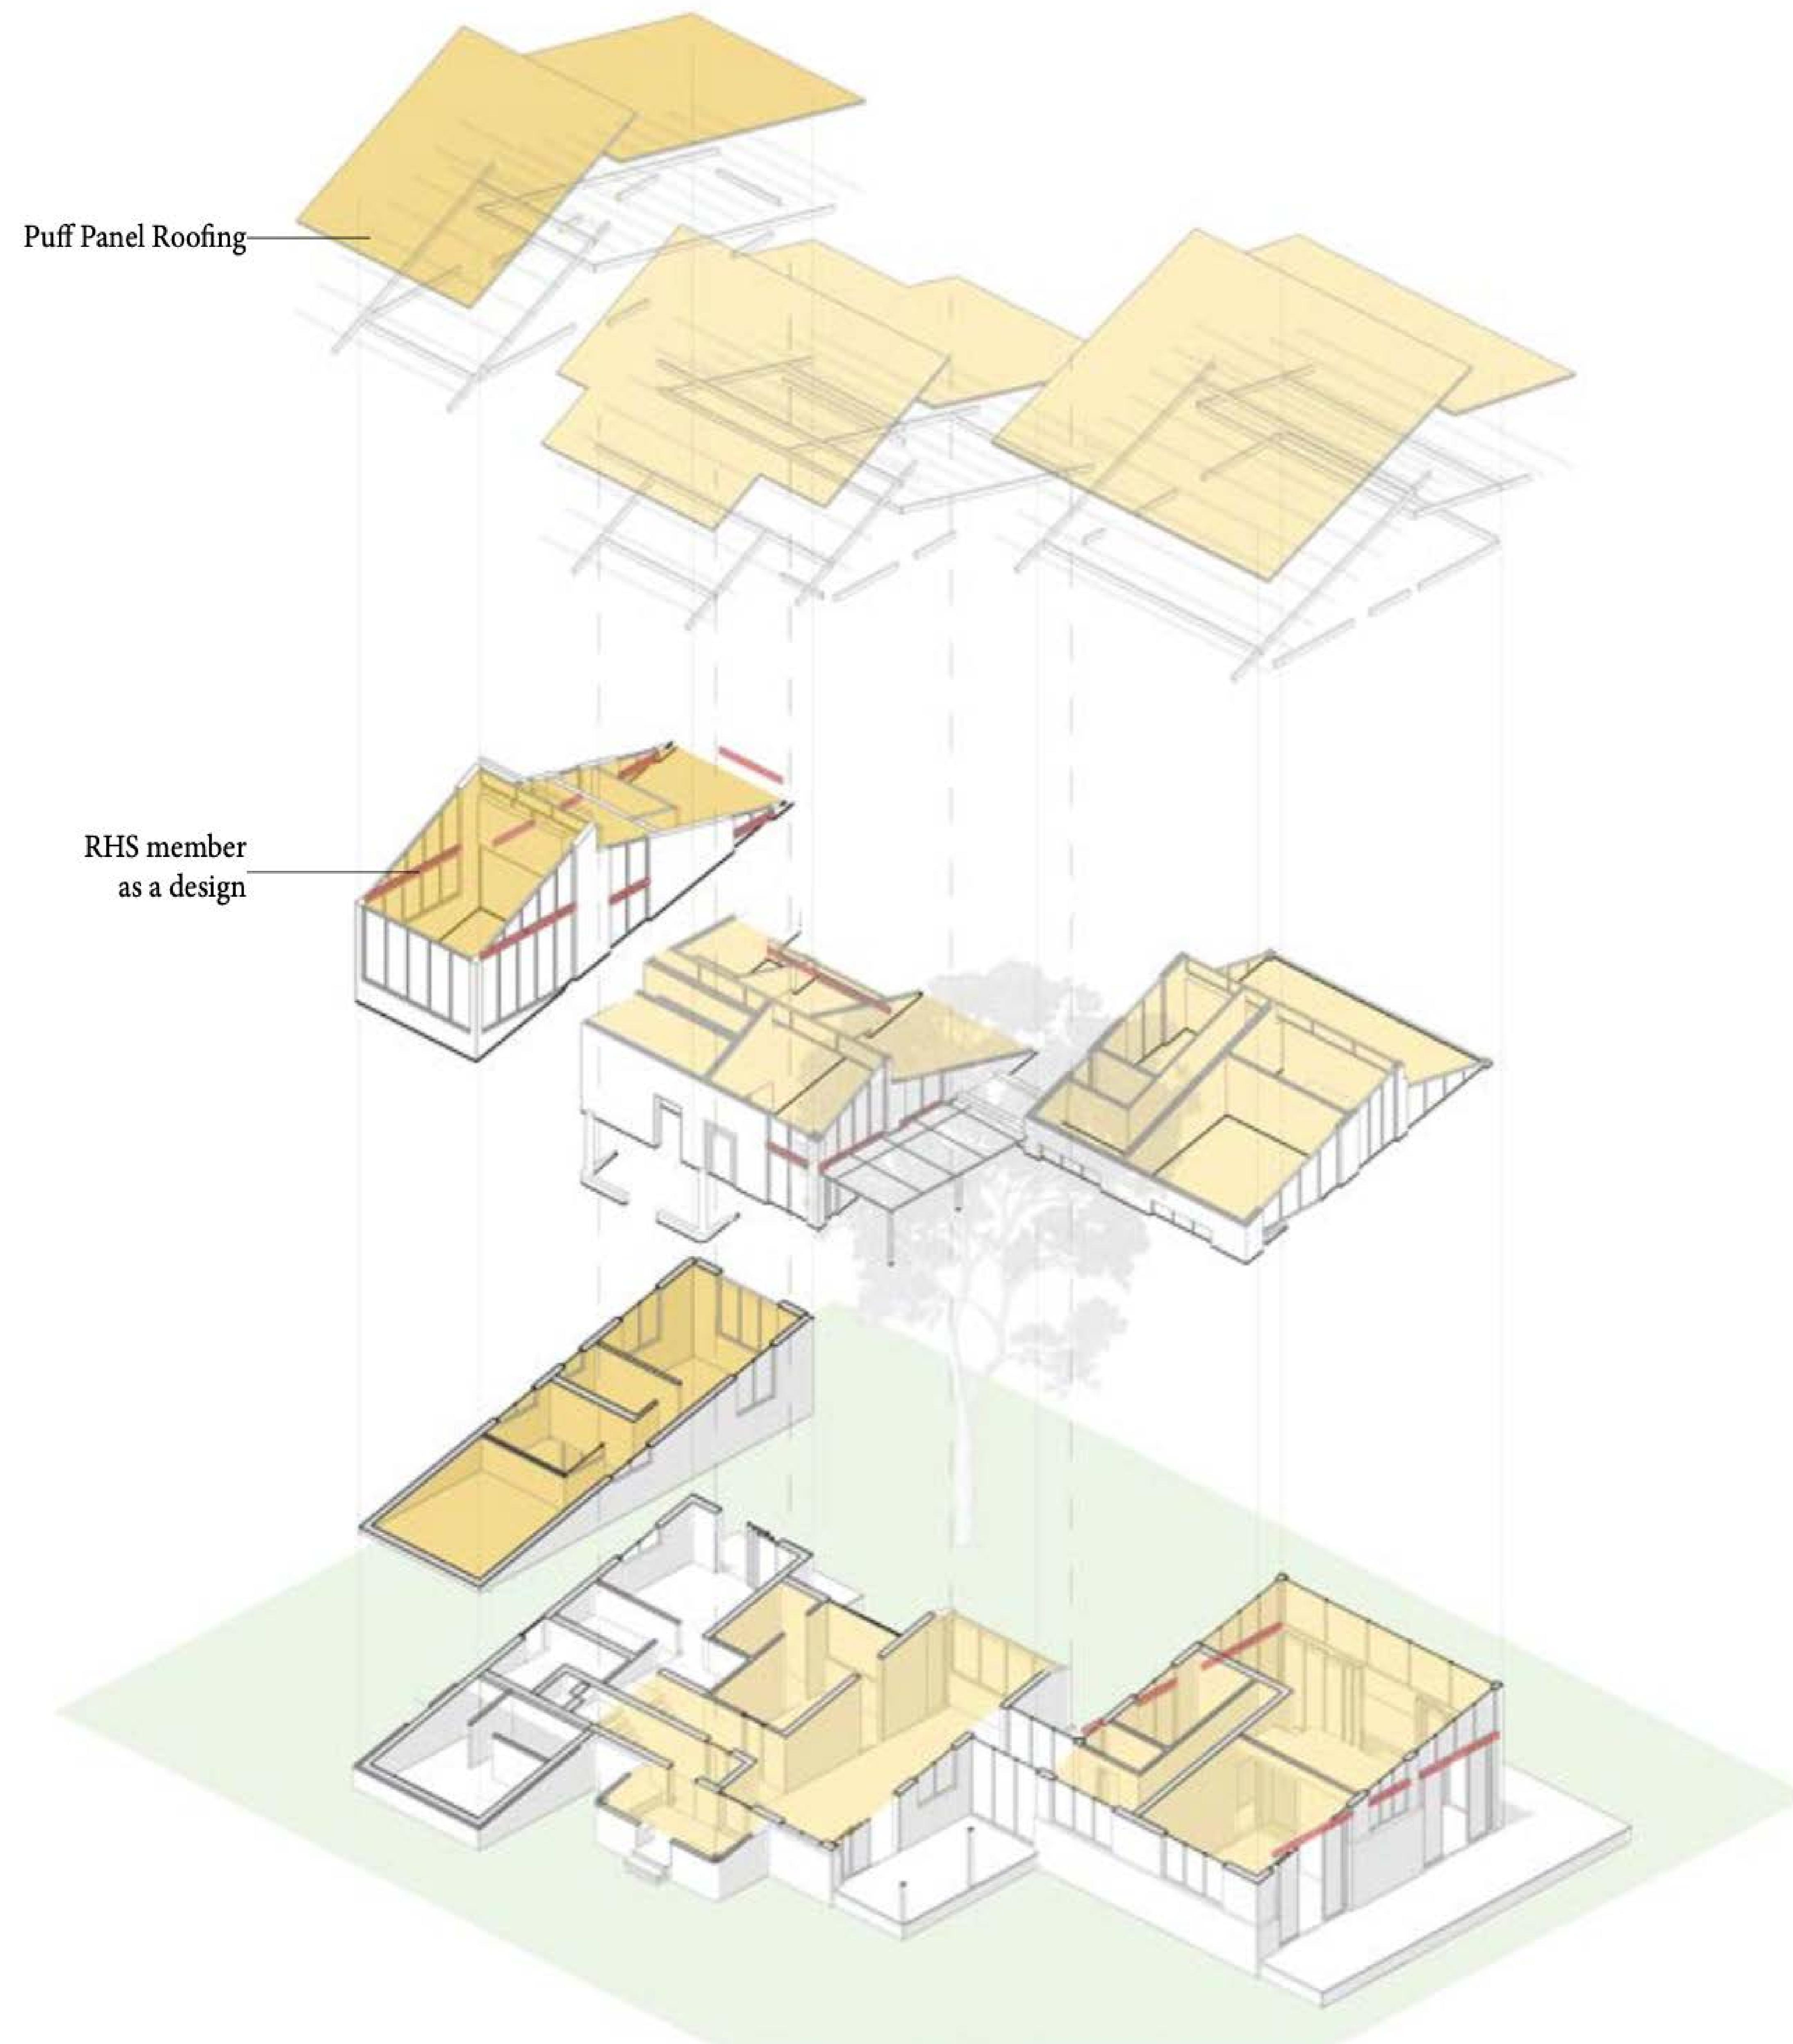


# Internship









Freelance Projects  
 Client - Thomas D'monte  
 Built Up Area- 1140 Sq.ft


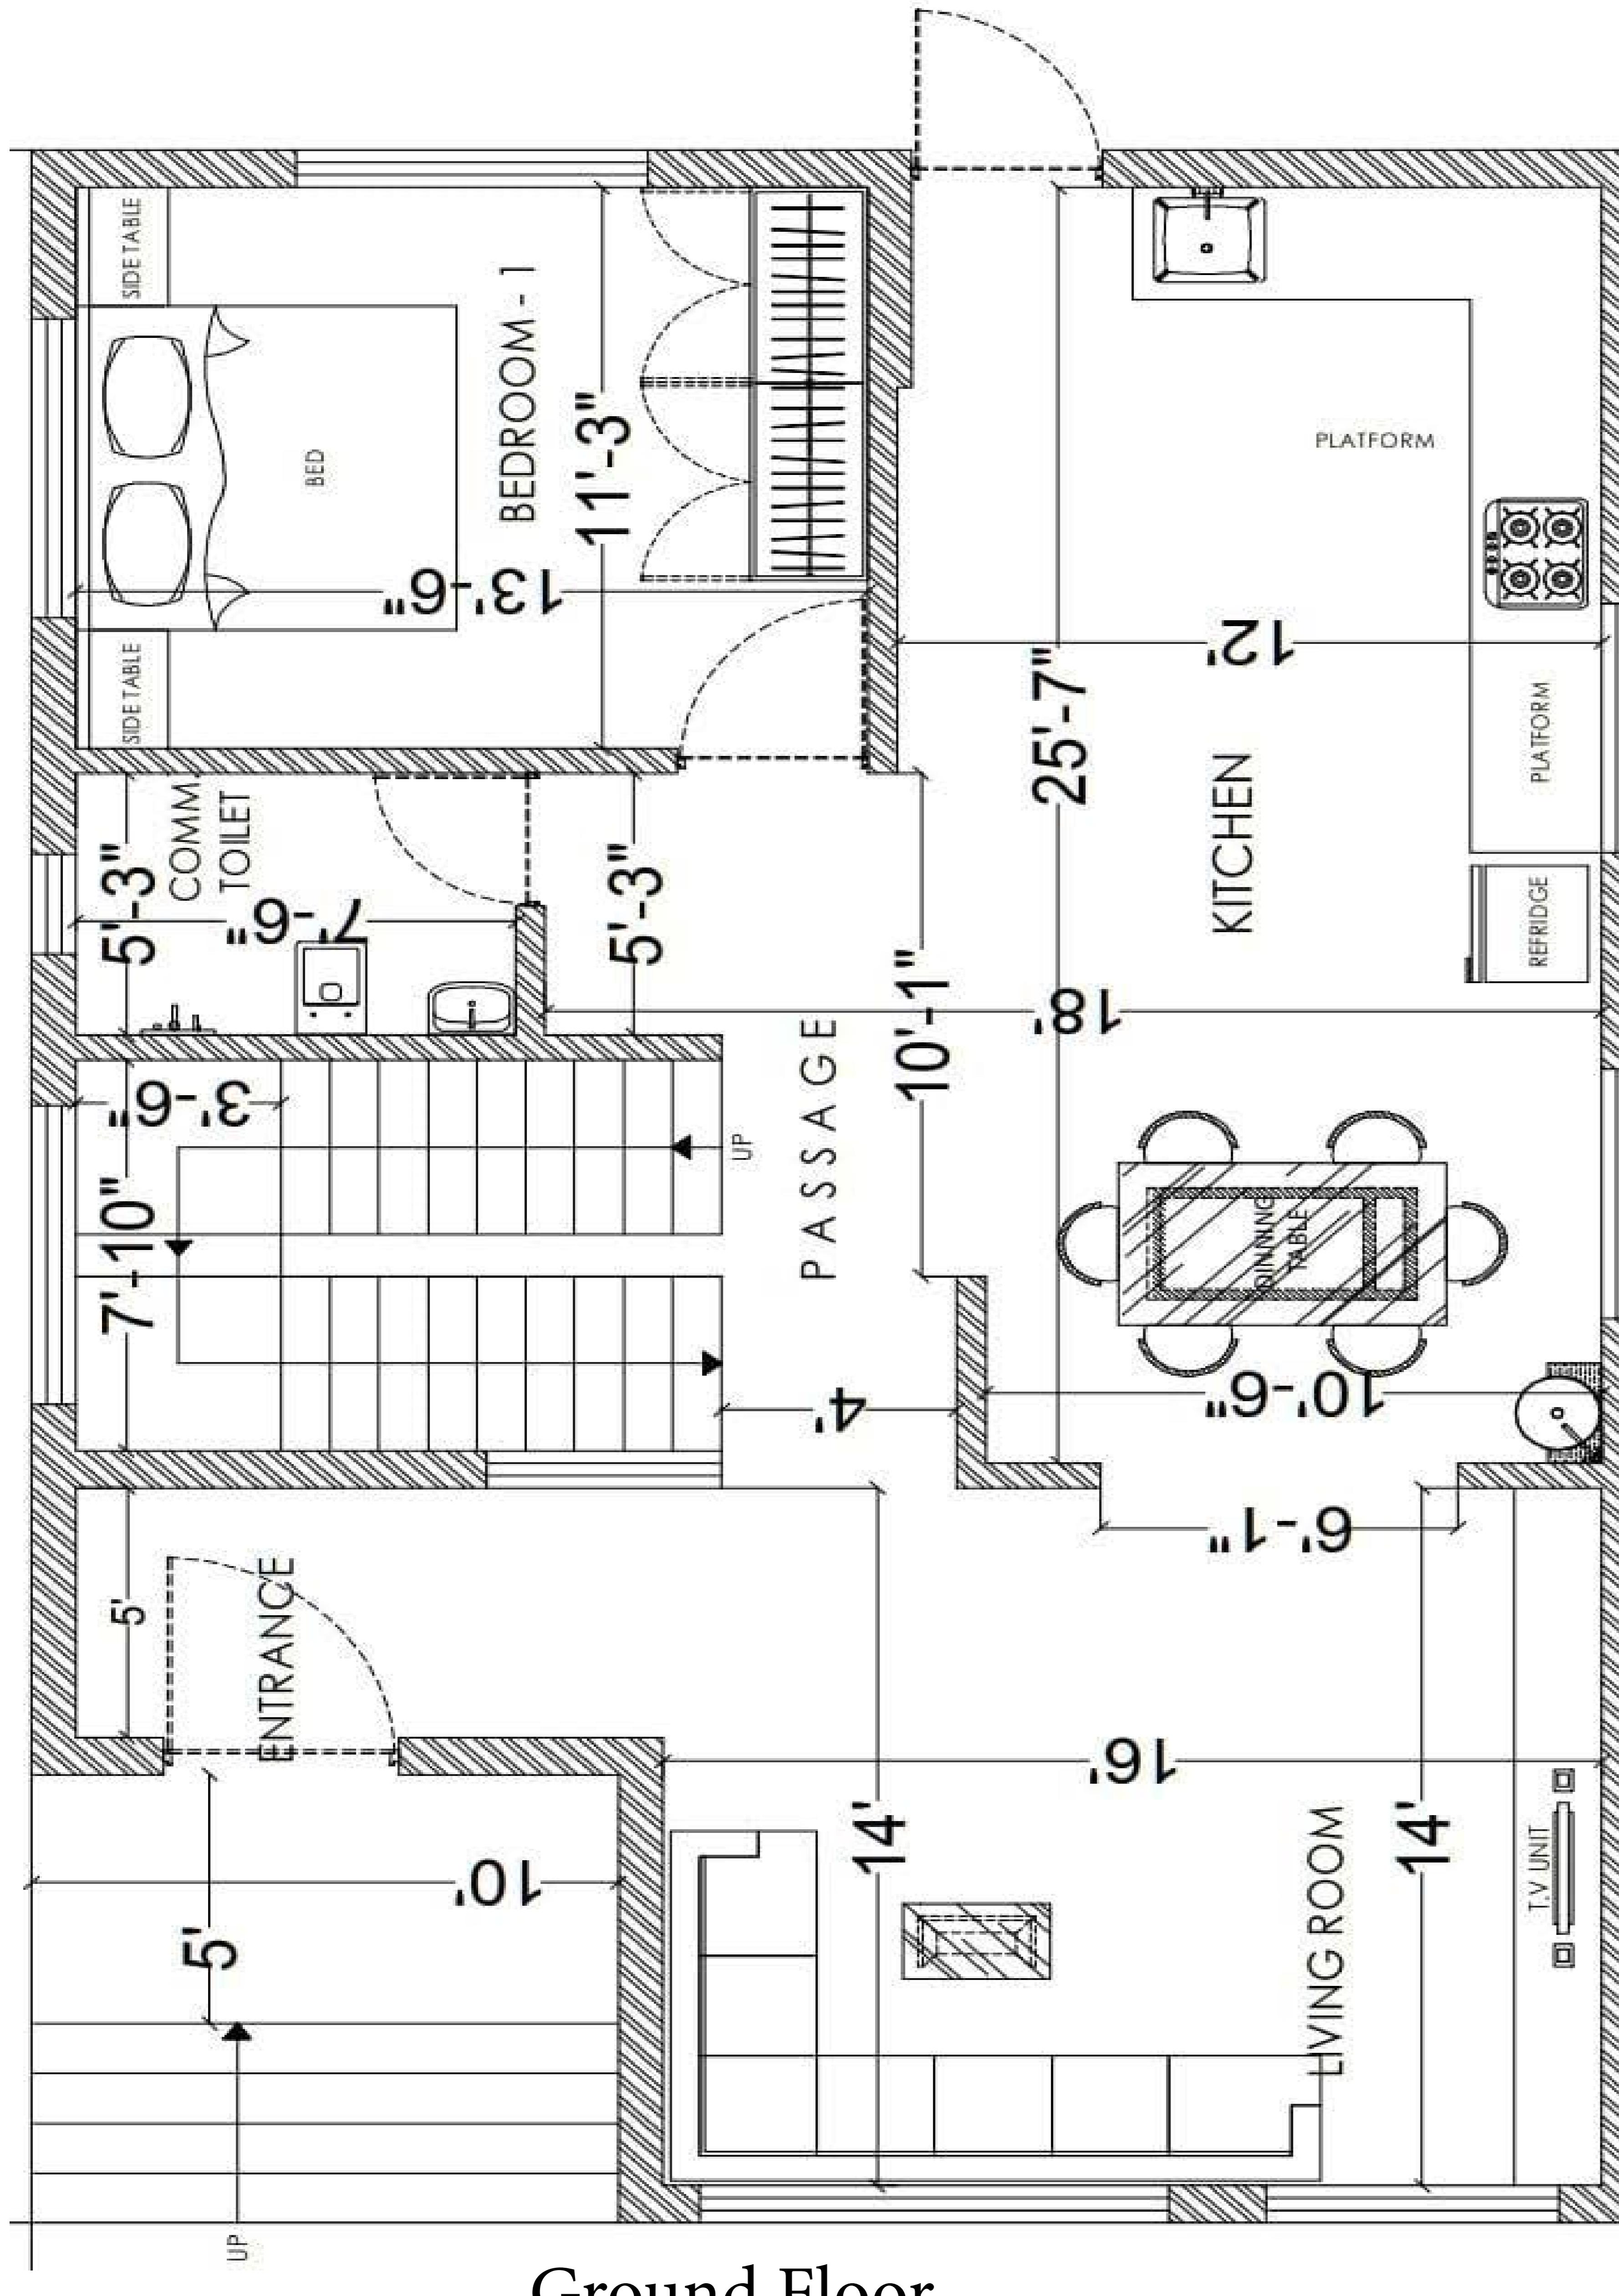


Ground Floor

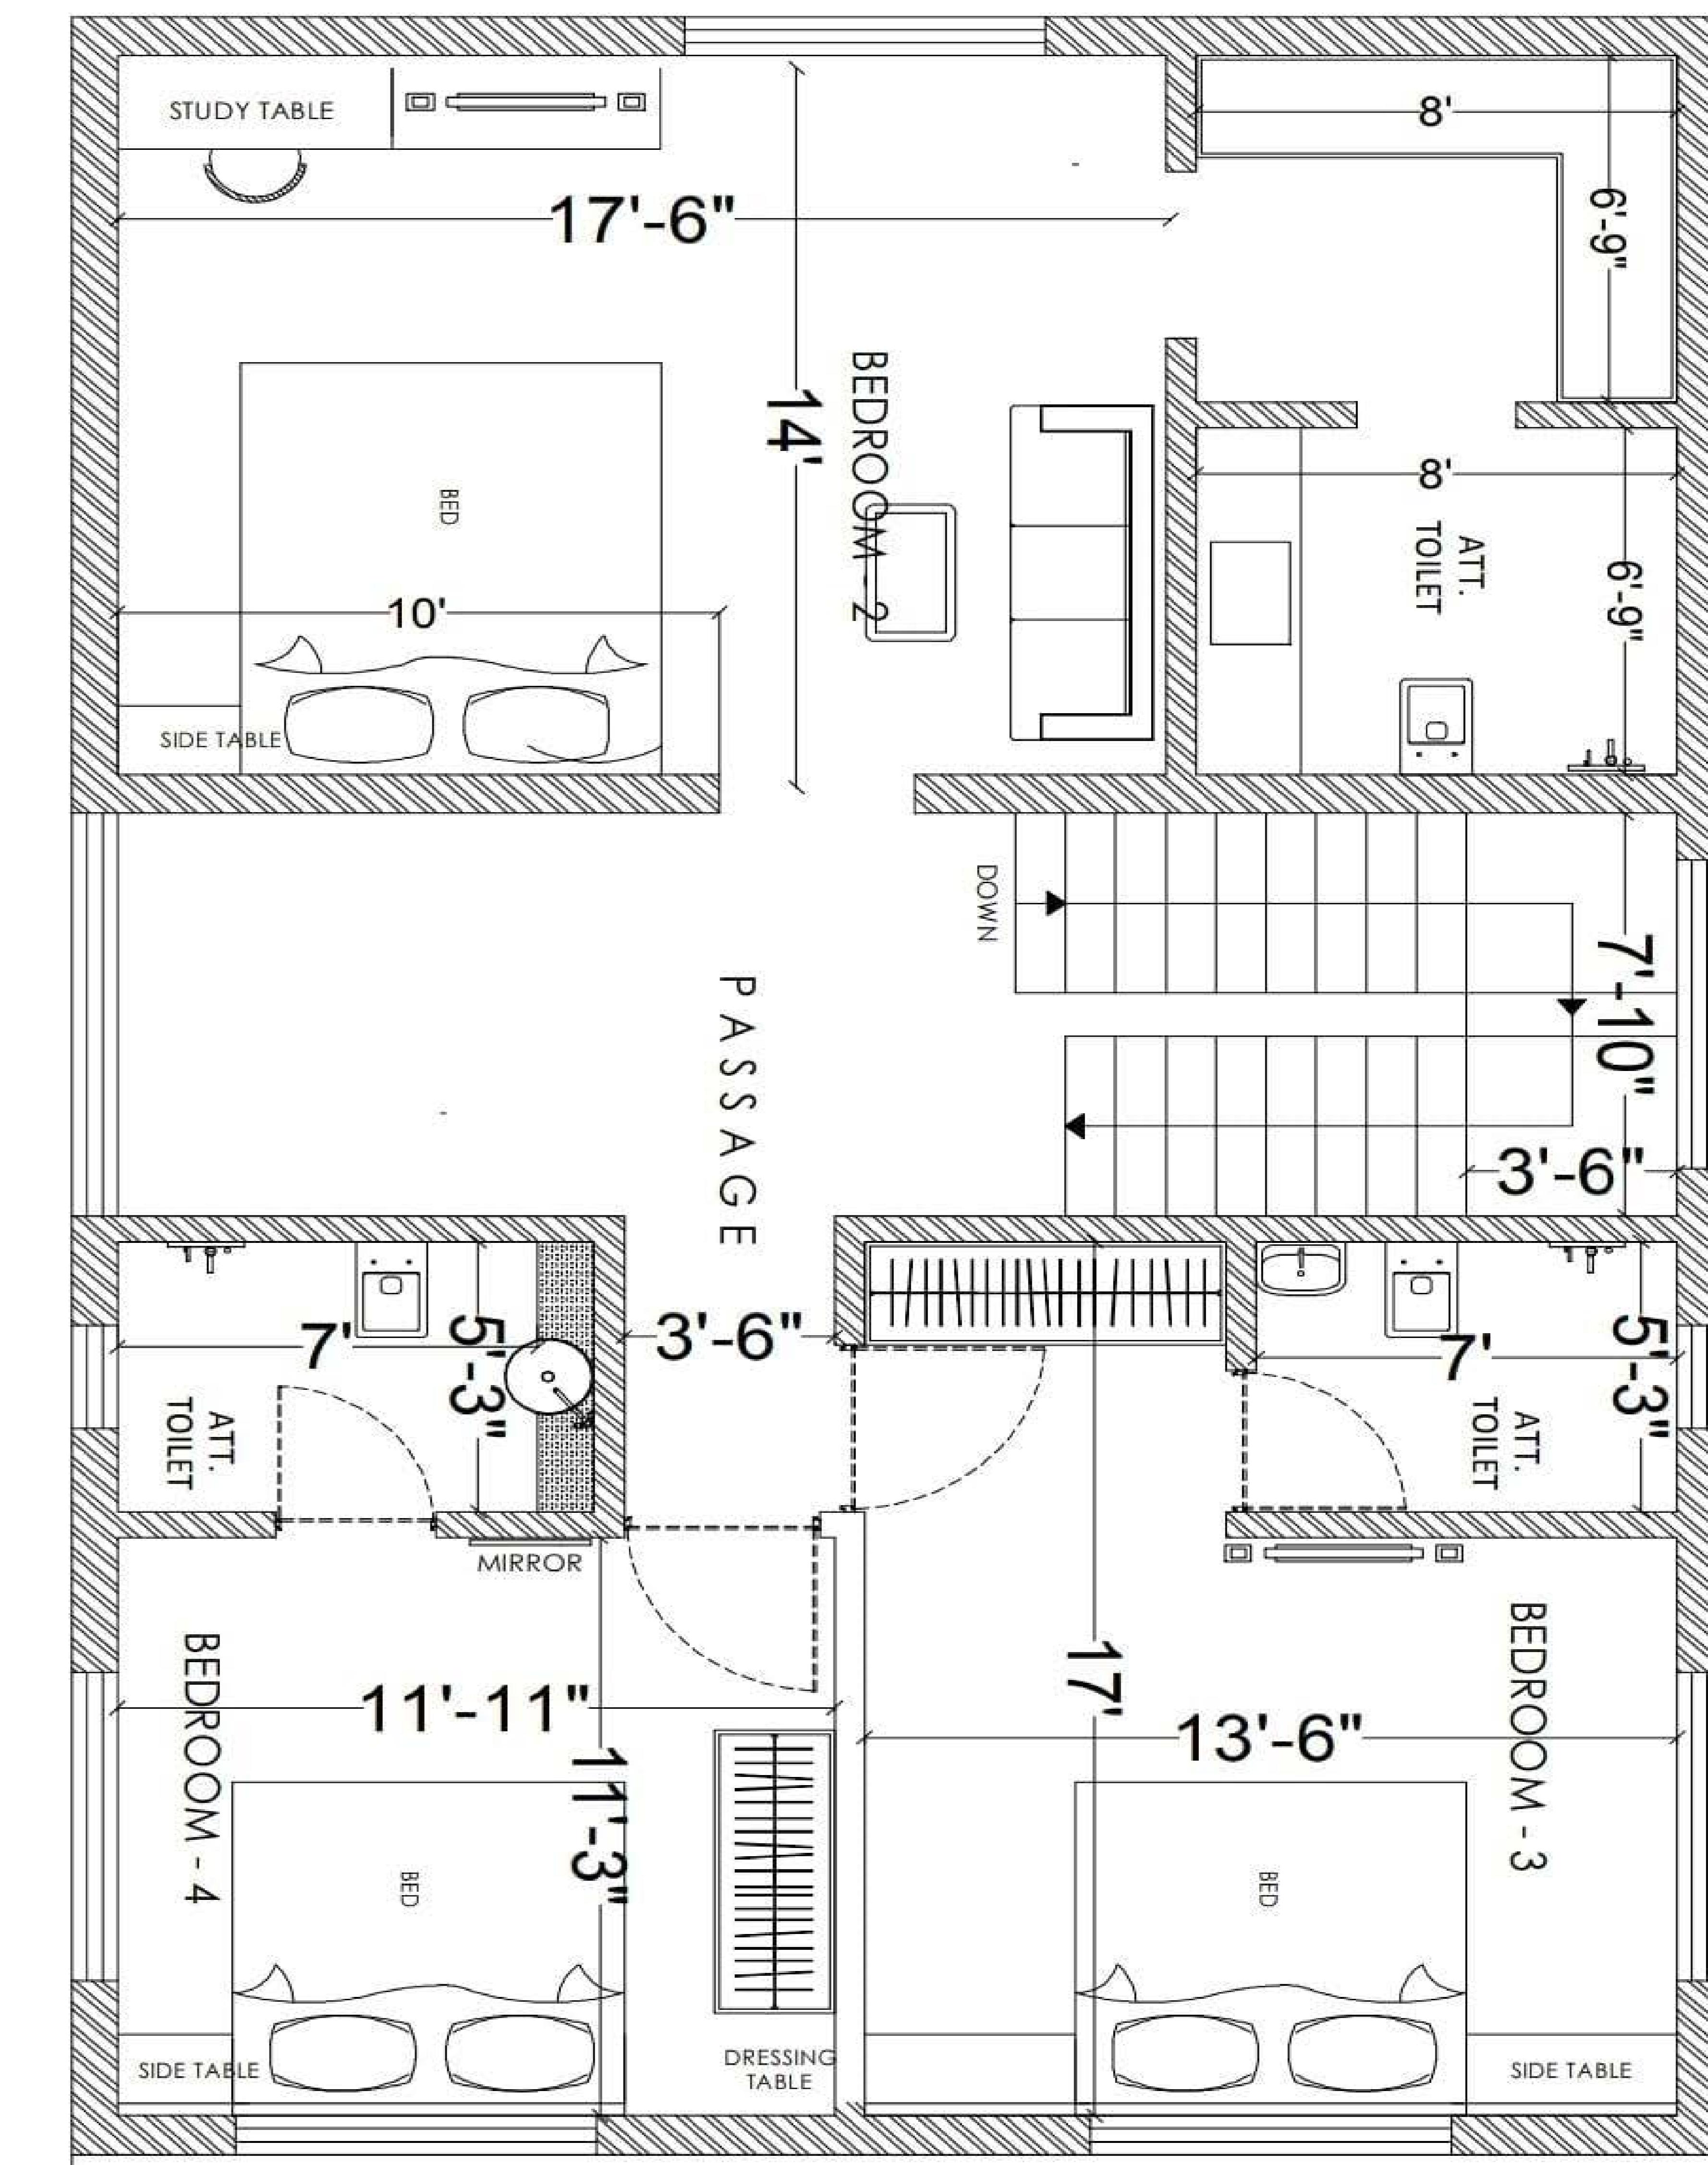

First Floor

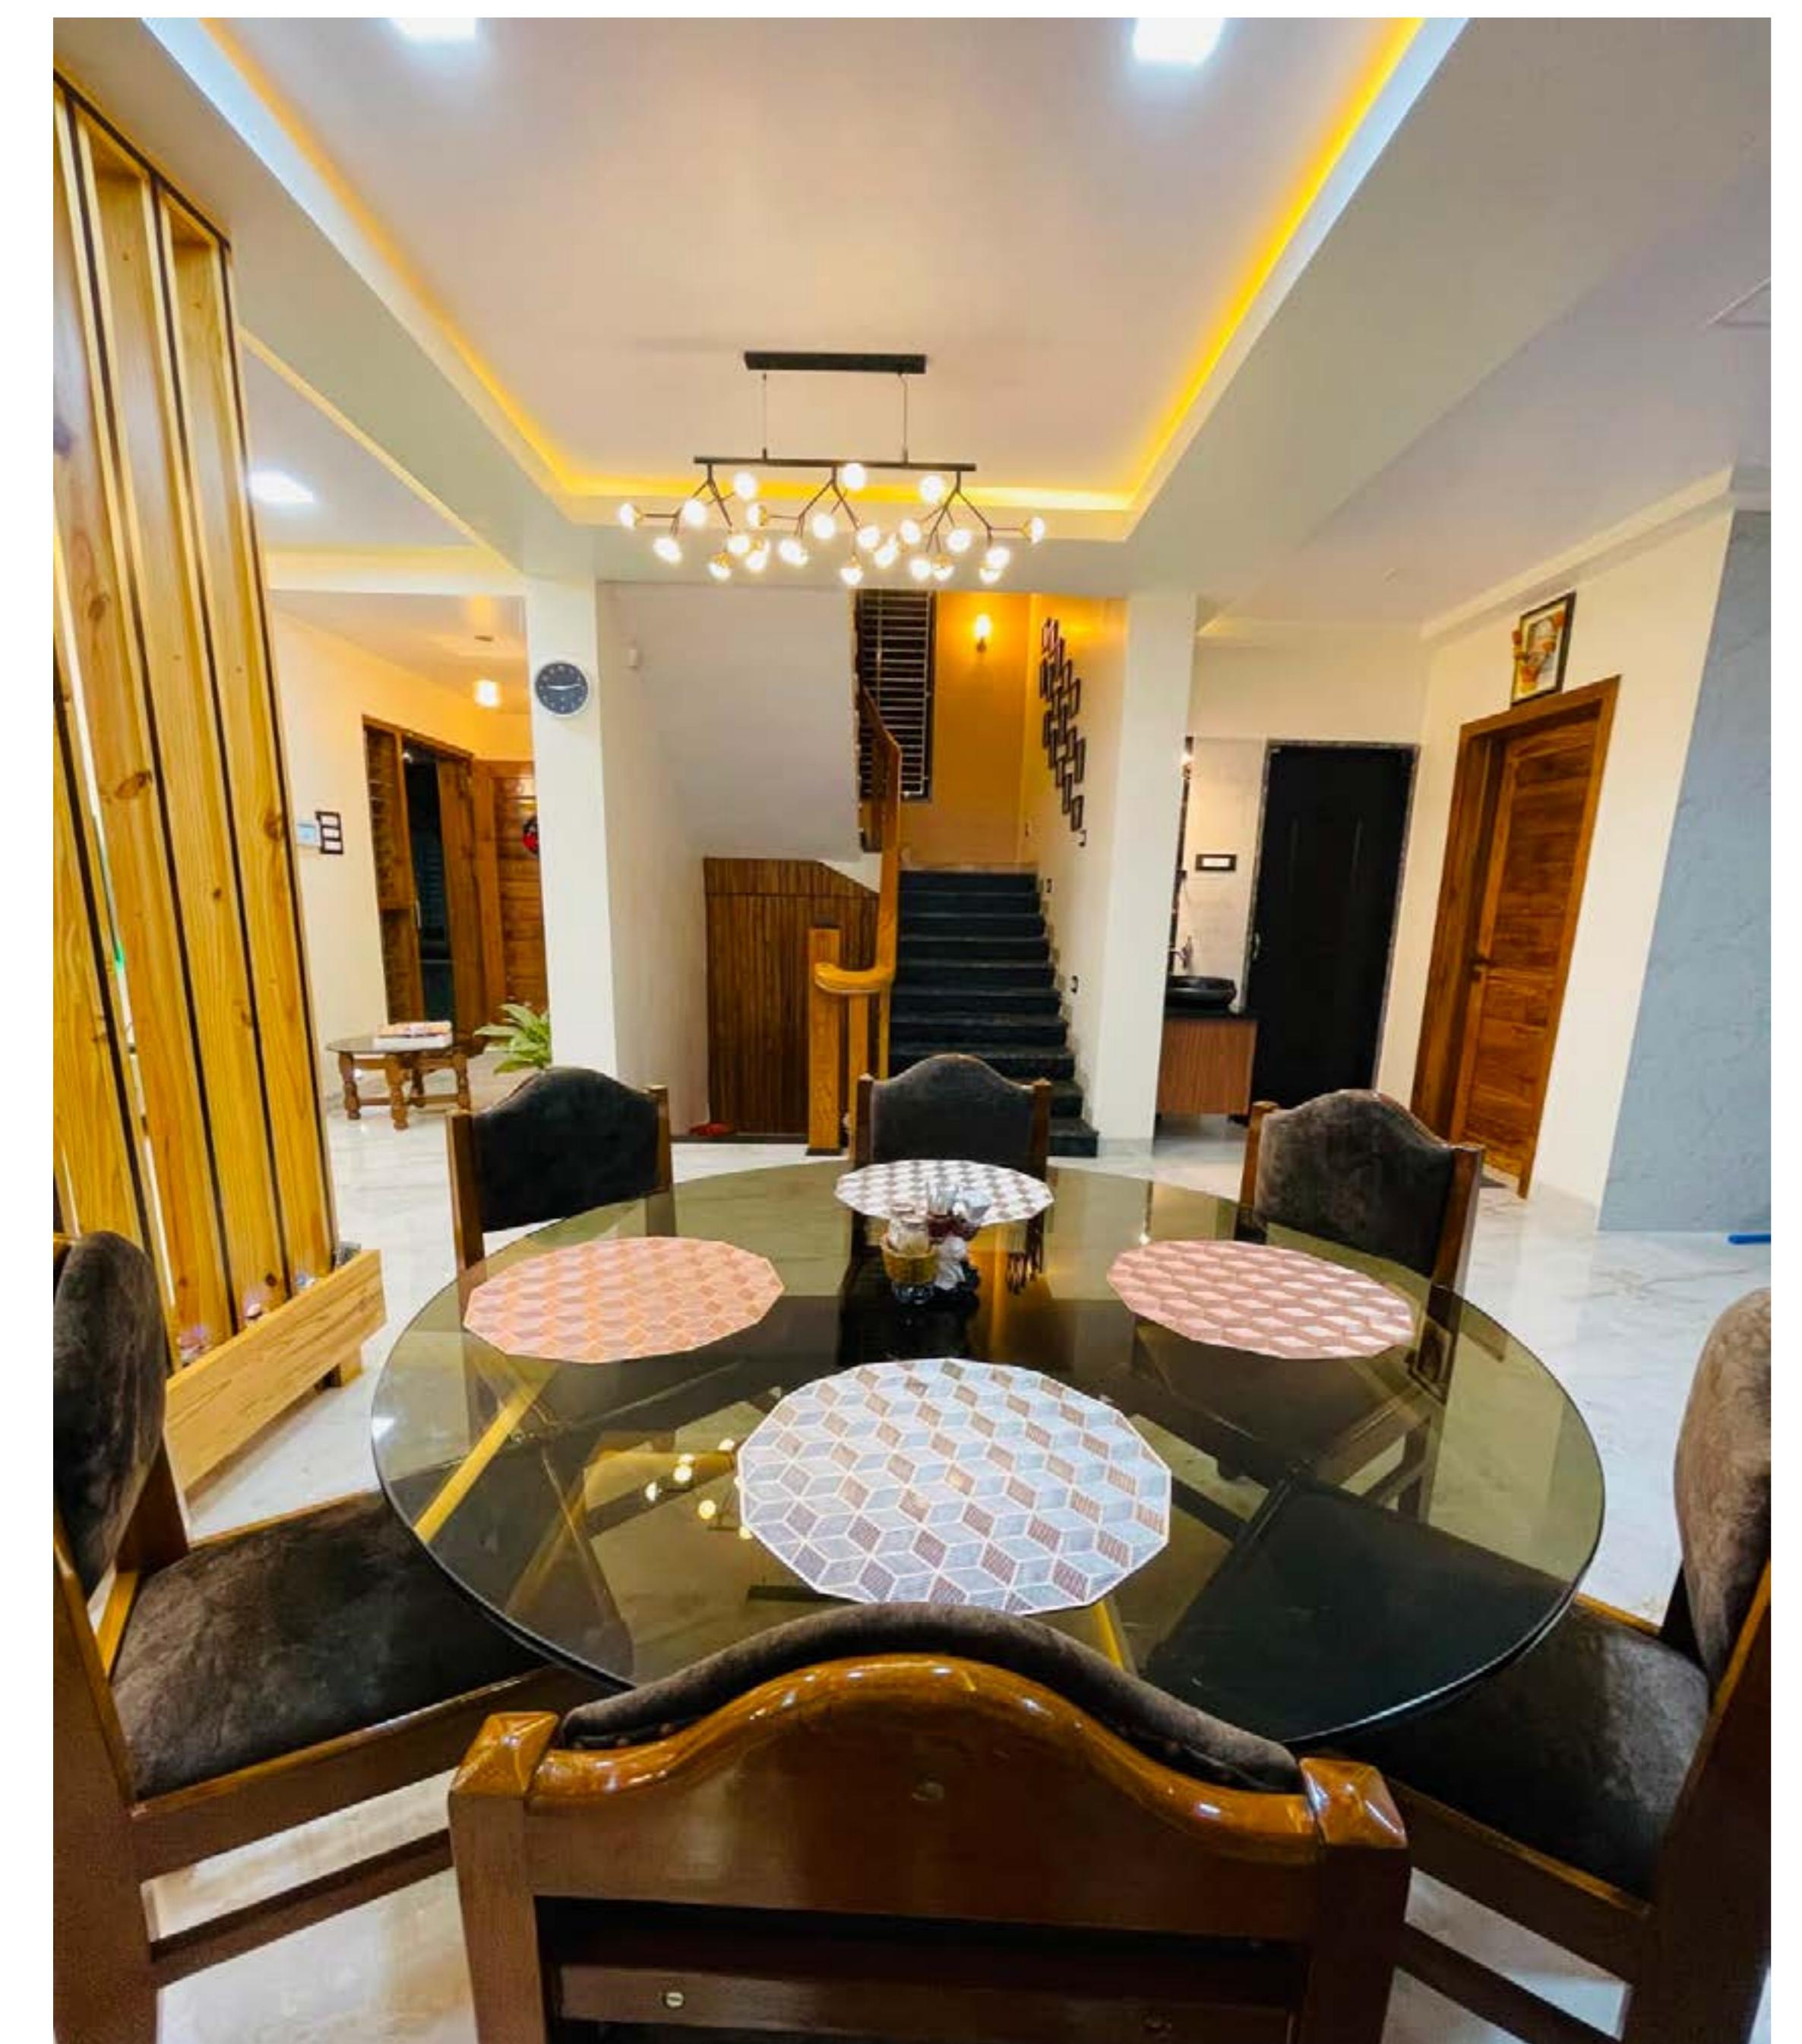


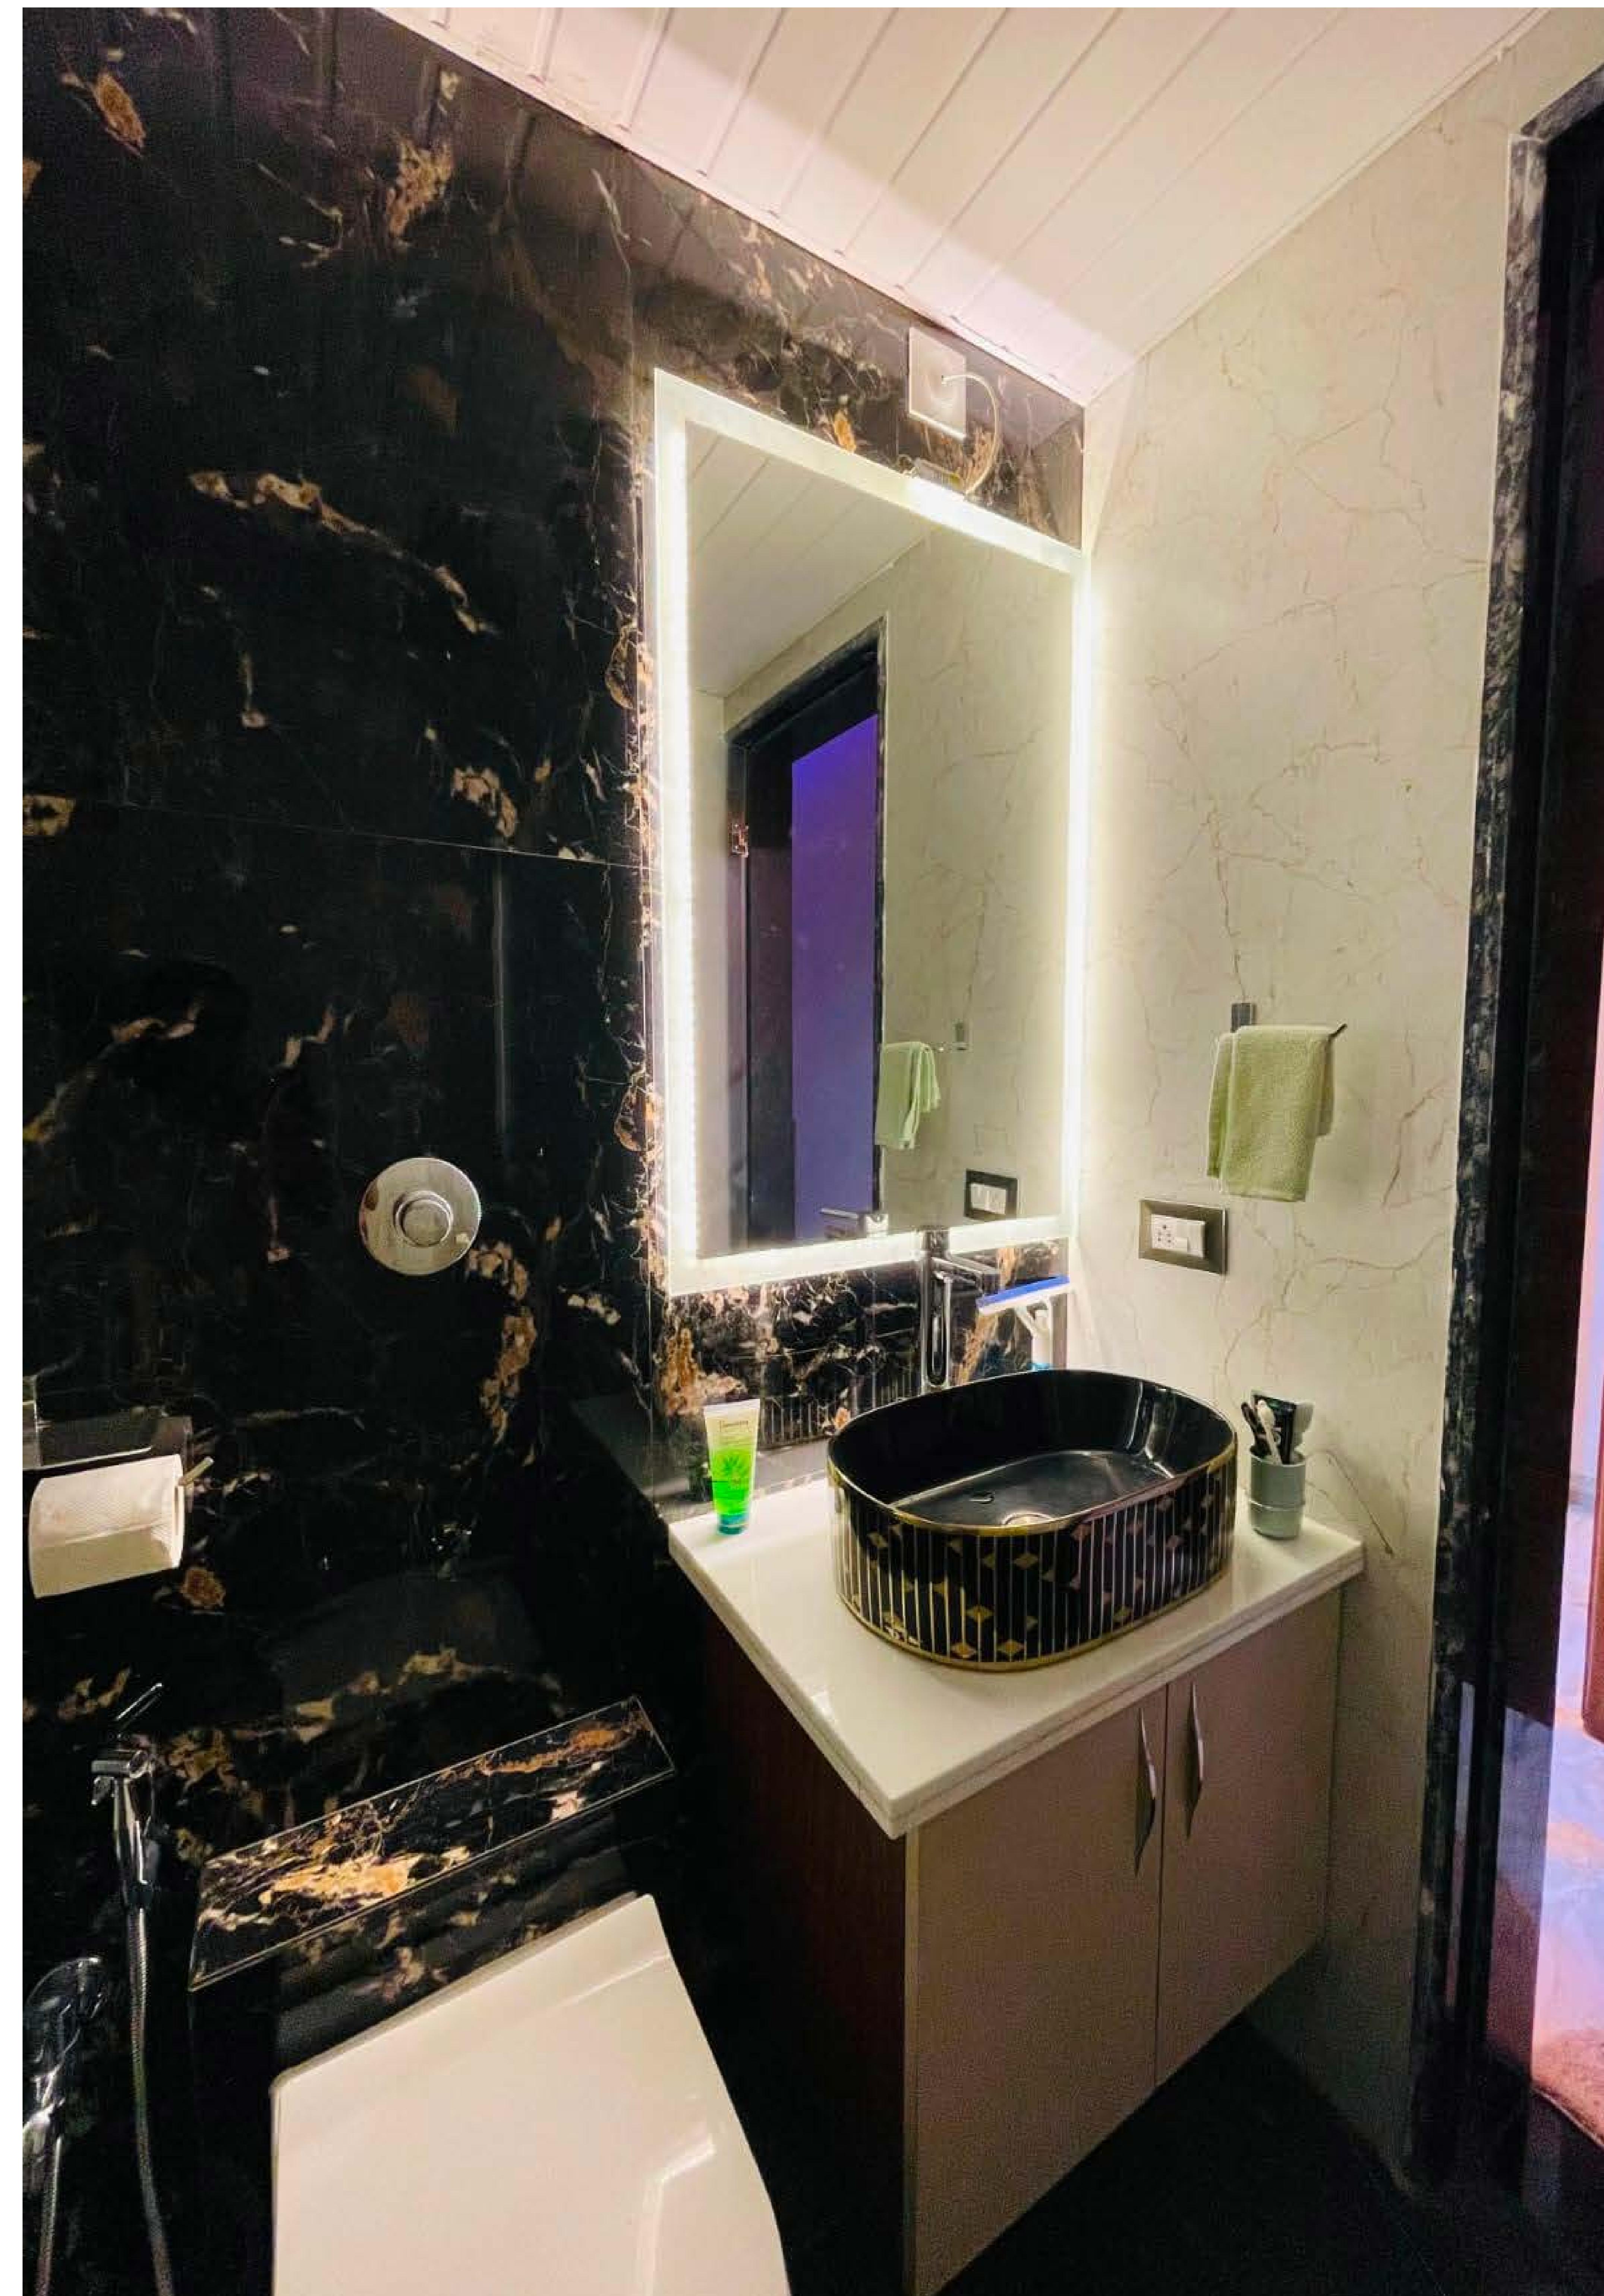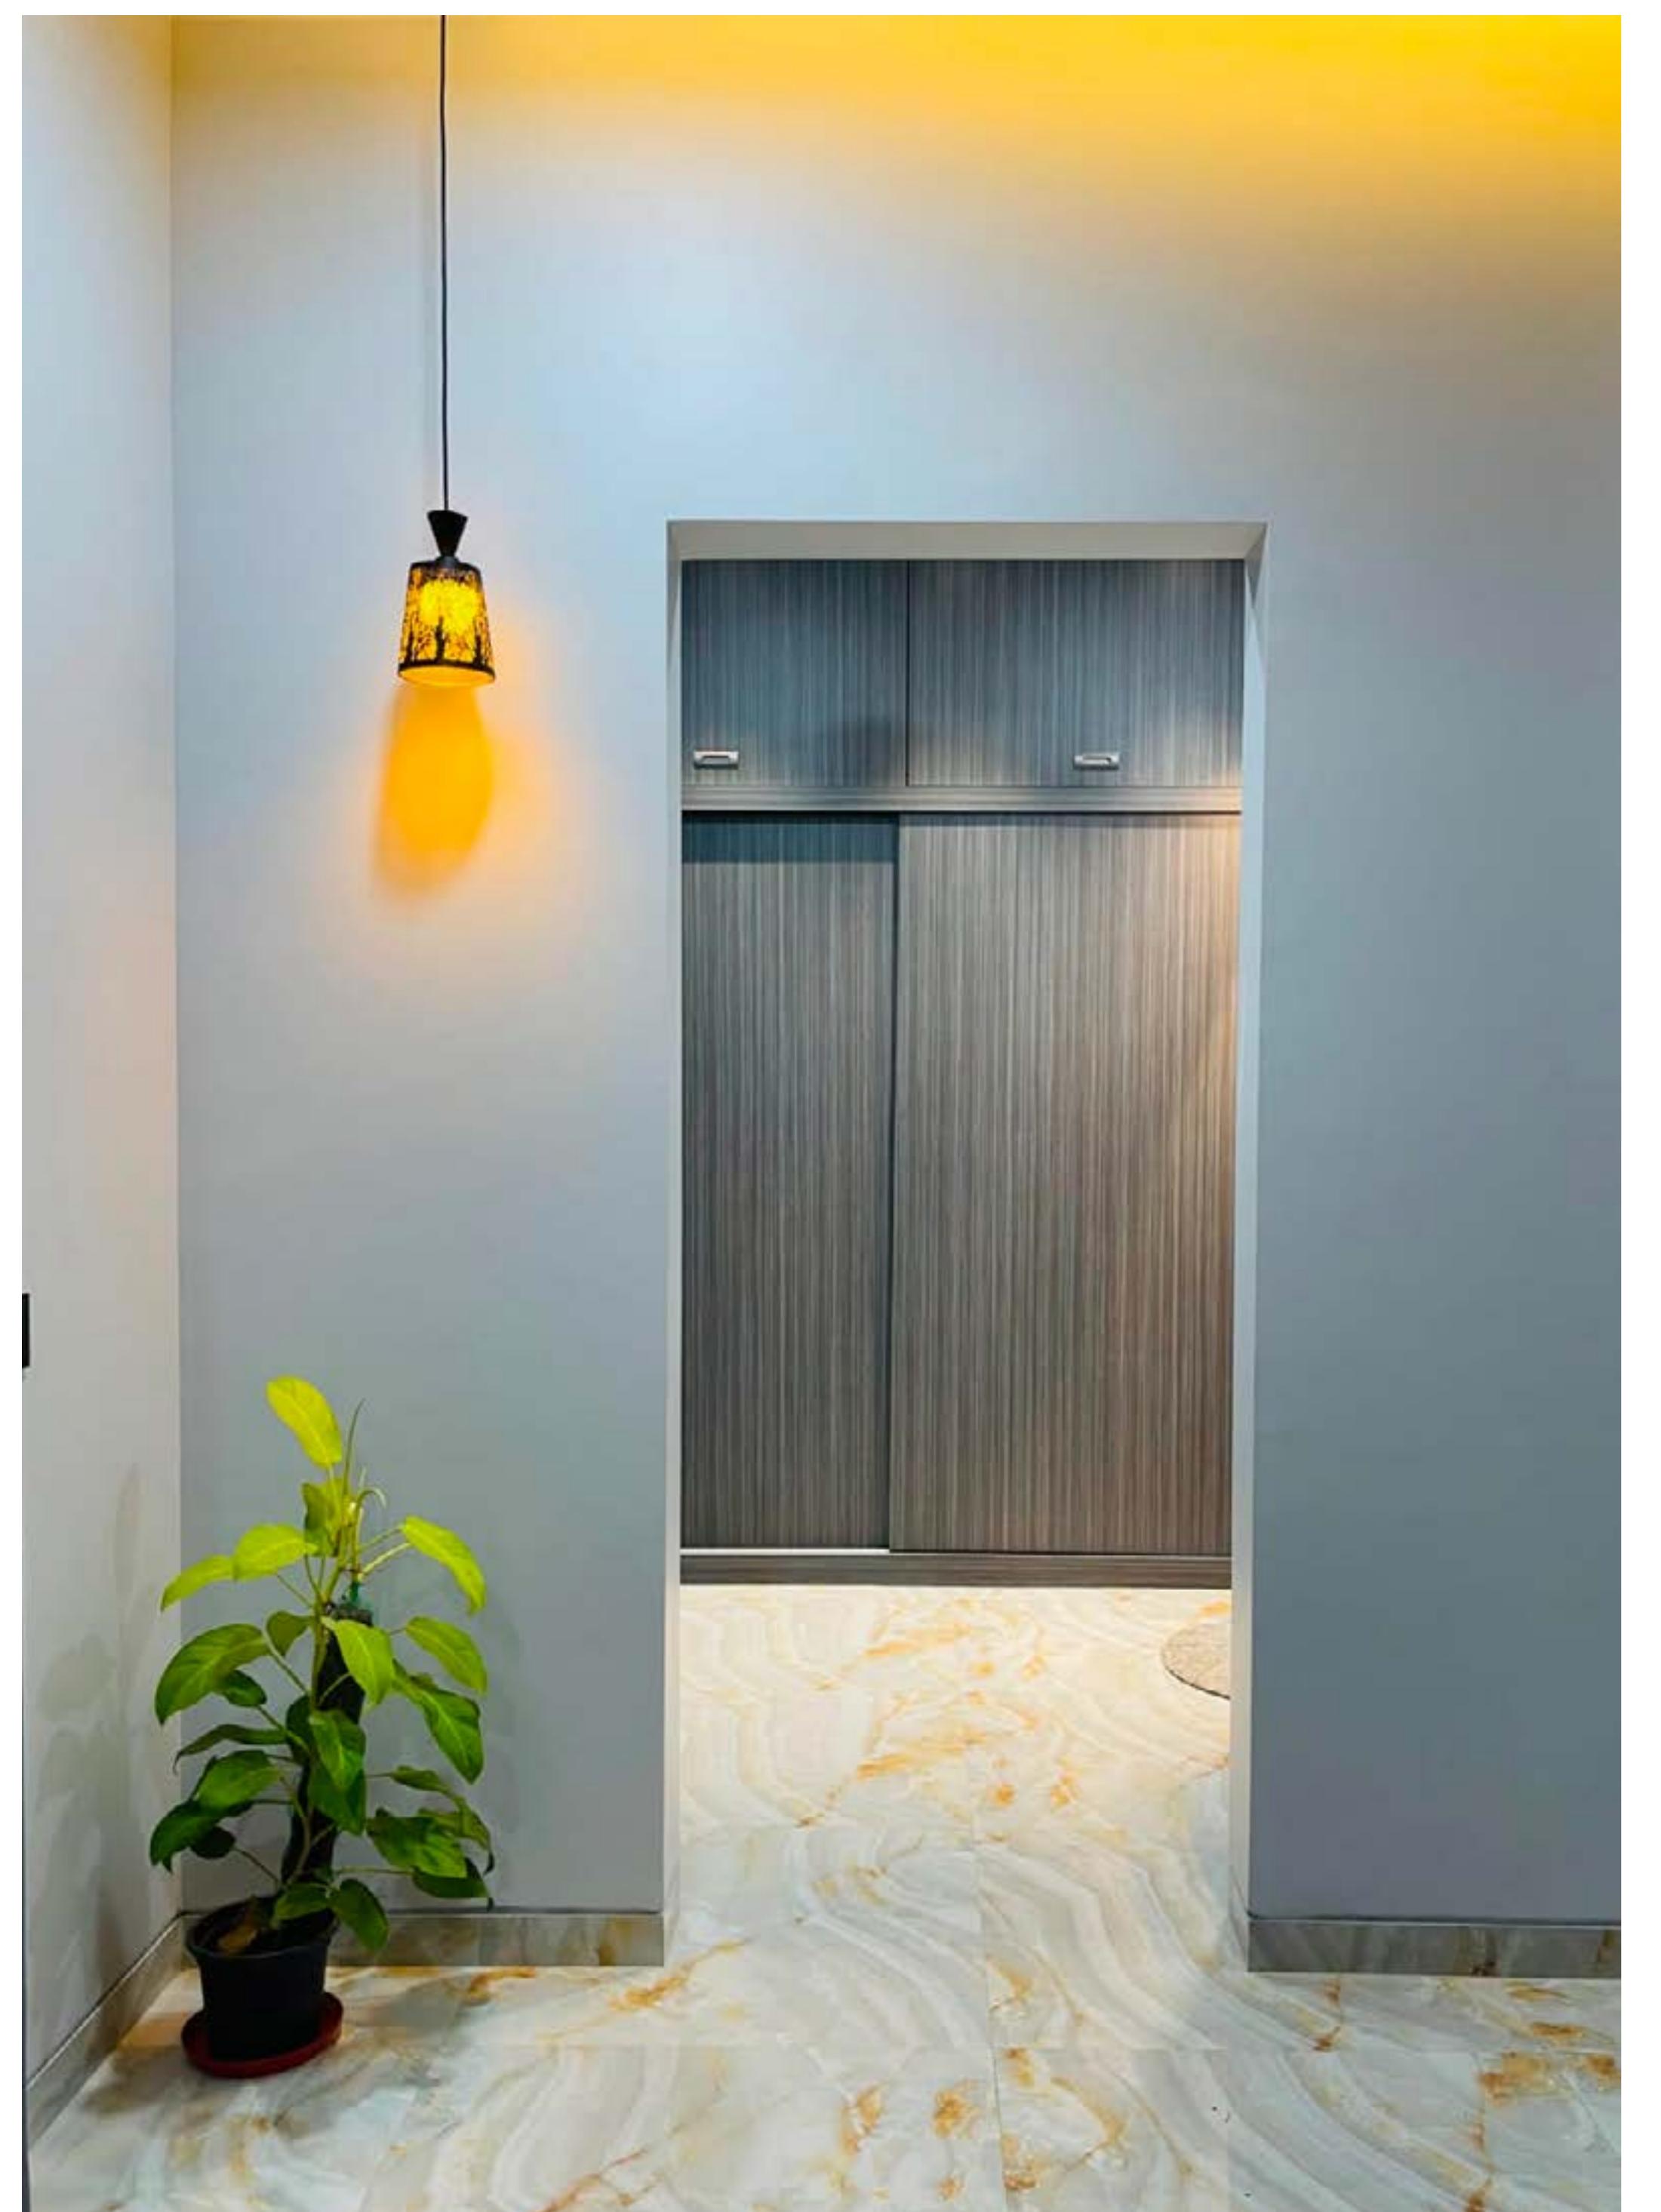


Client- Mathew Rodrigues

Plot Area- 3753.39 Sq.ft





Built Up Area- 1364.03 Sq.ft



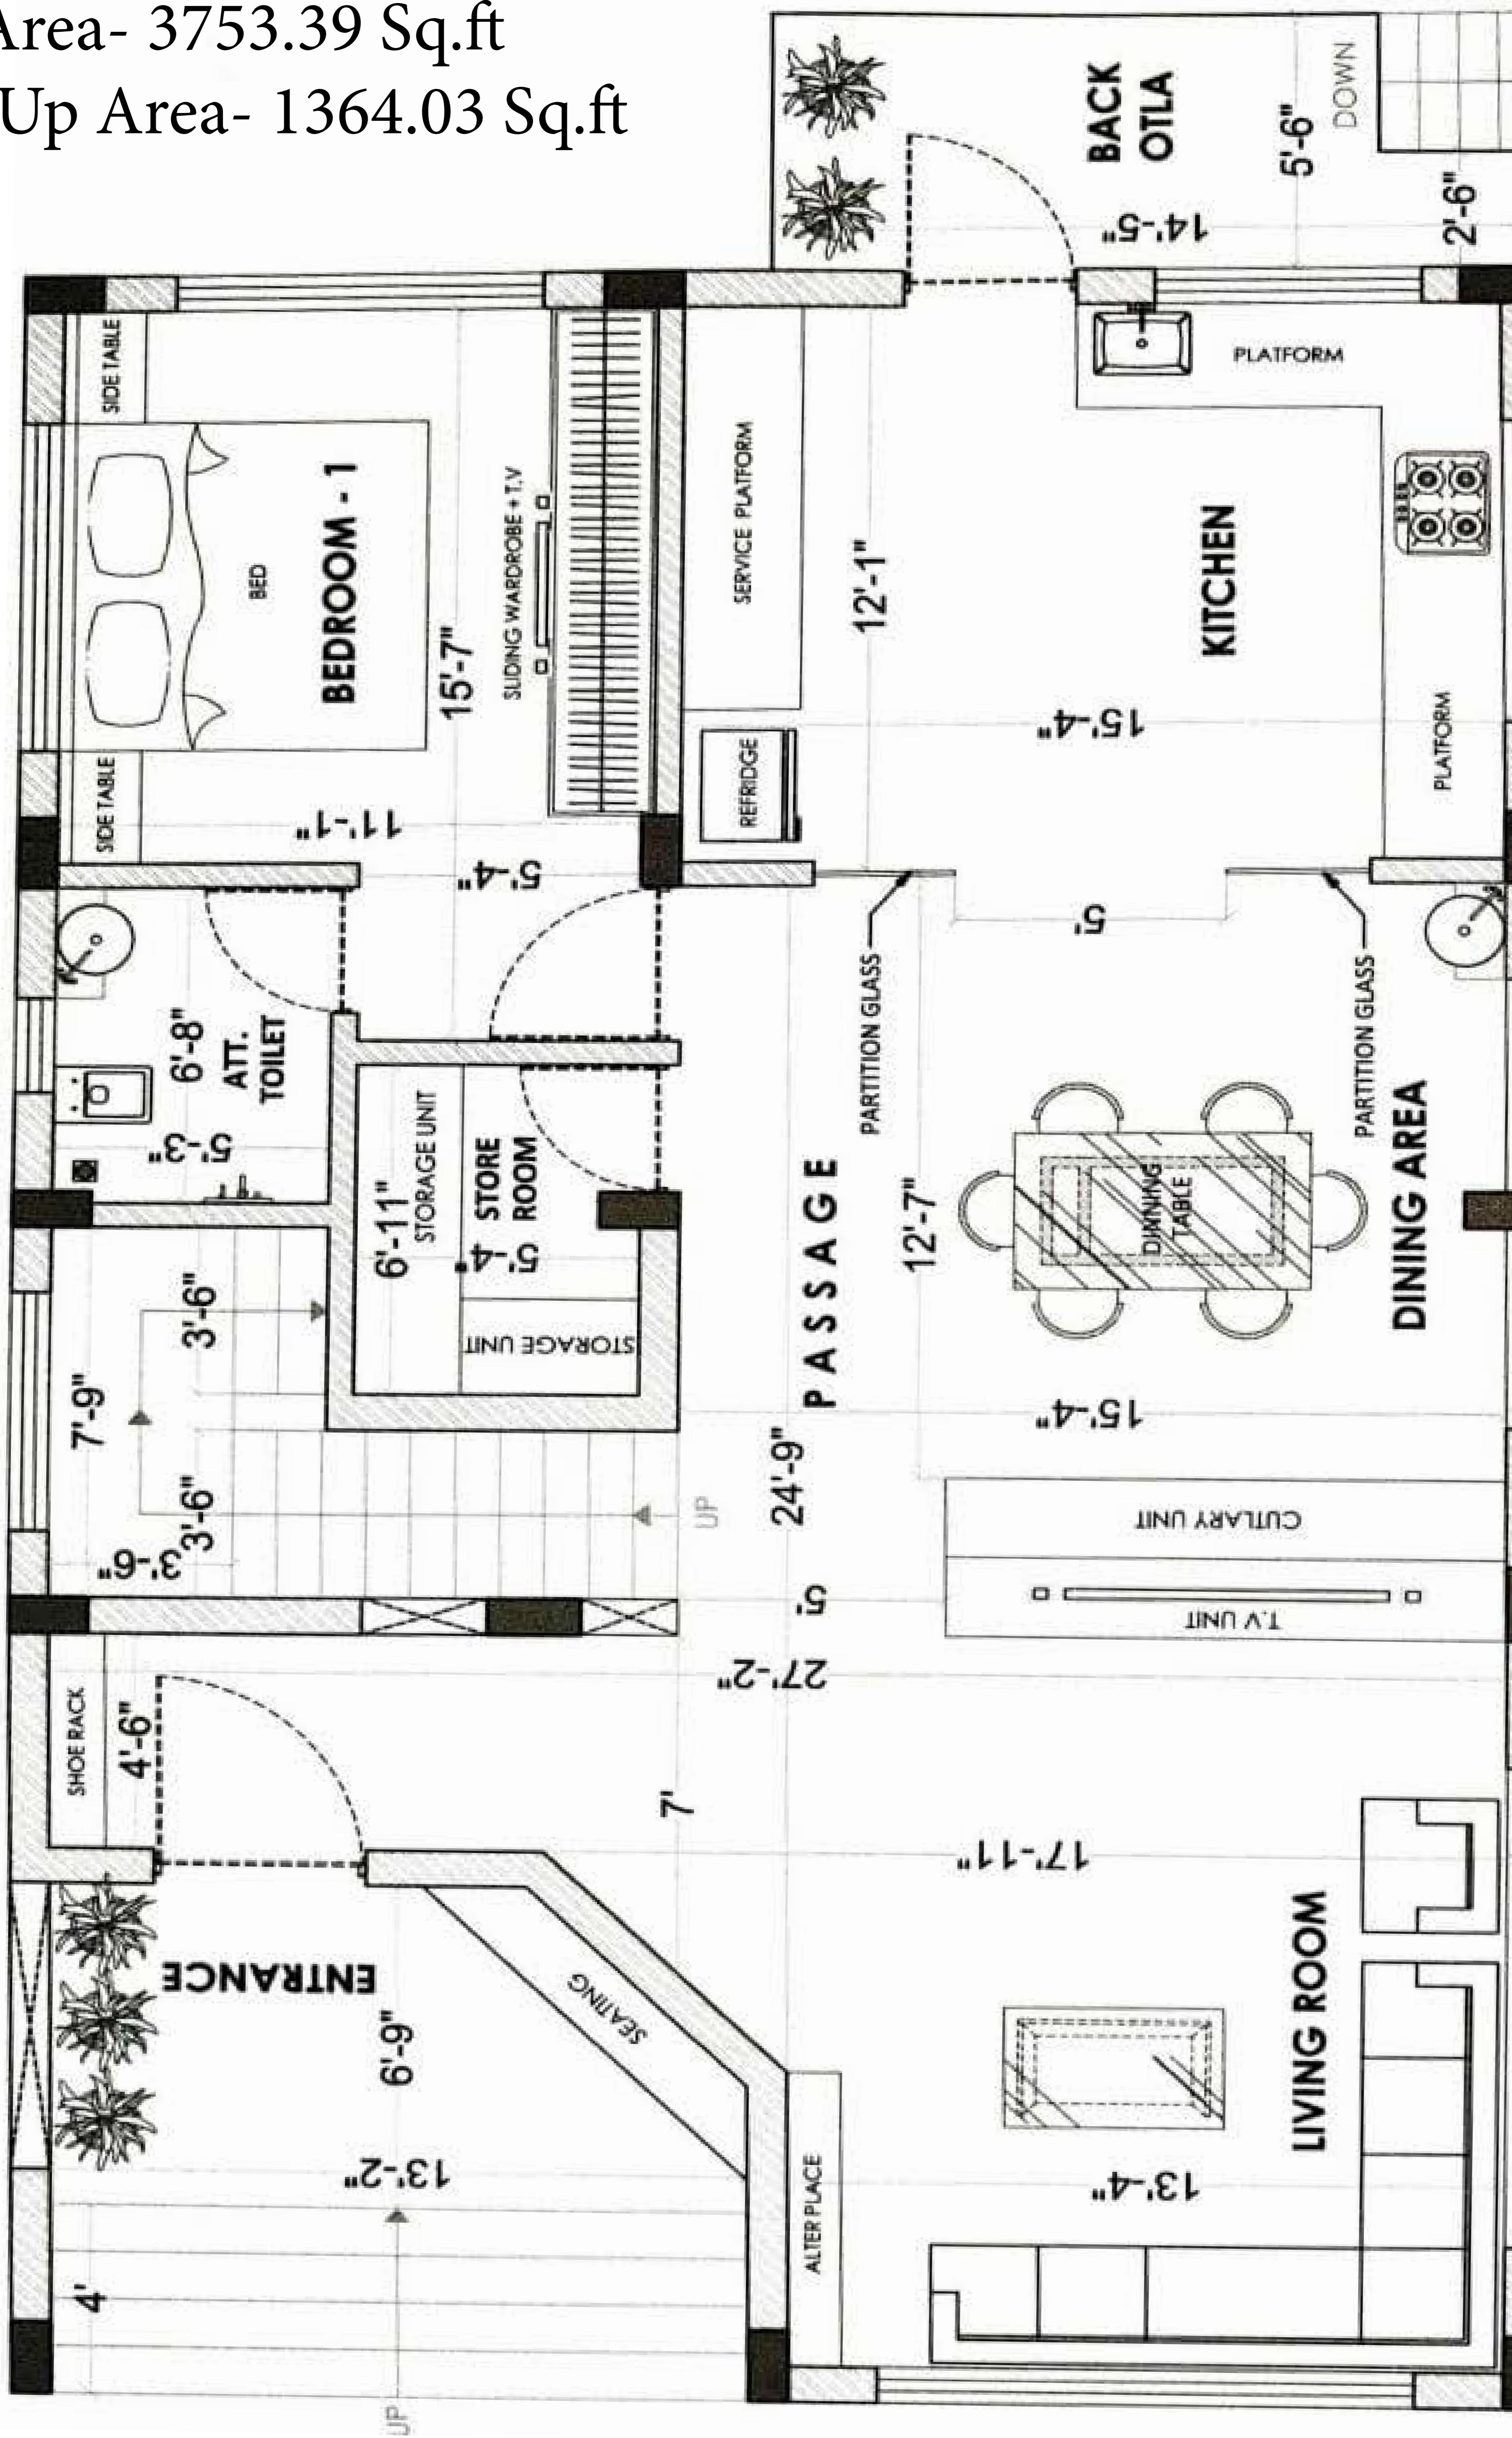


Ground Floor

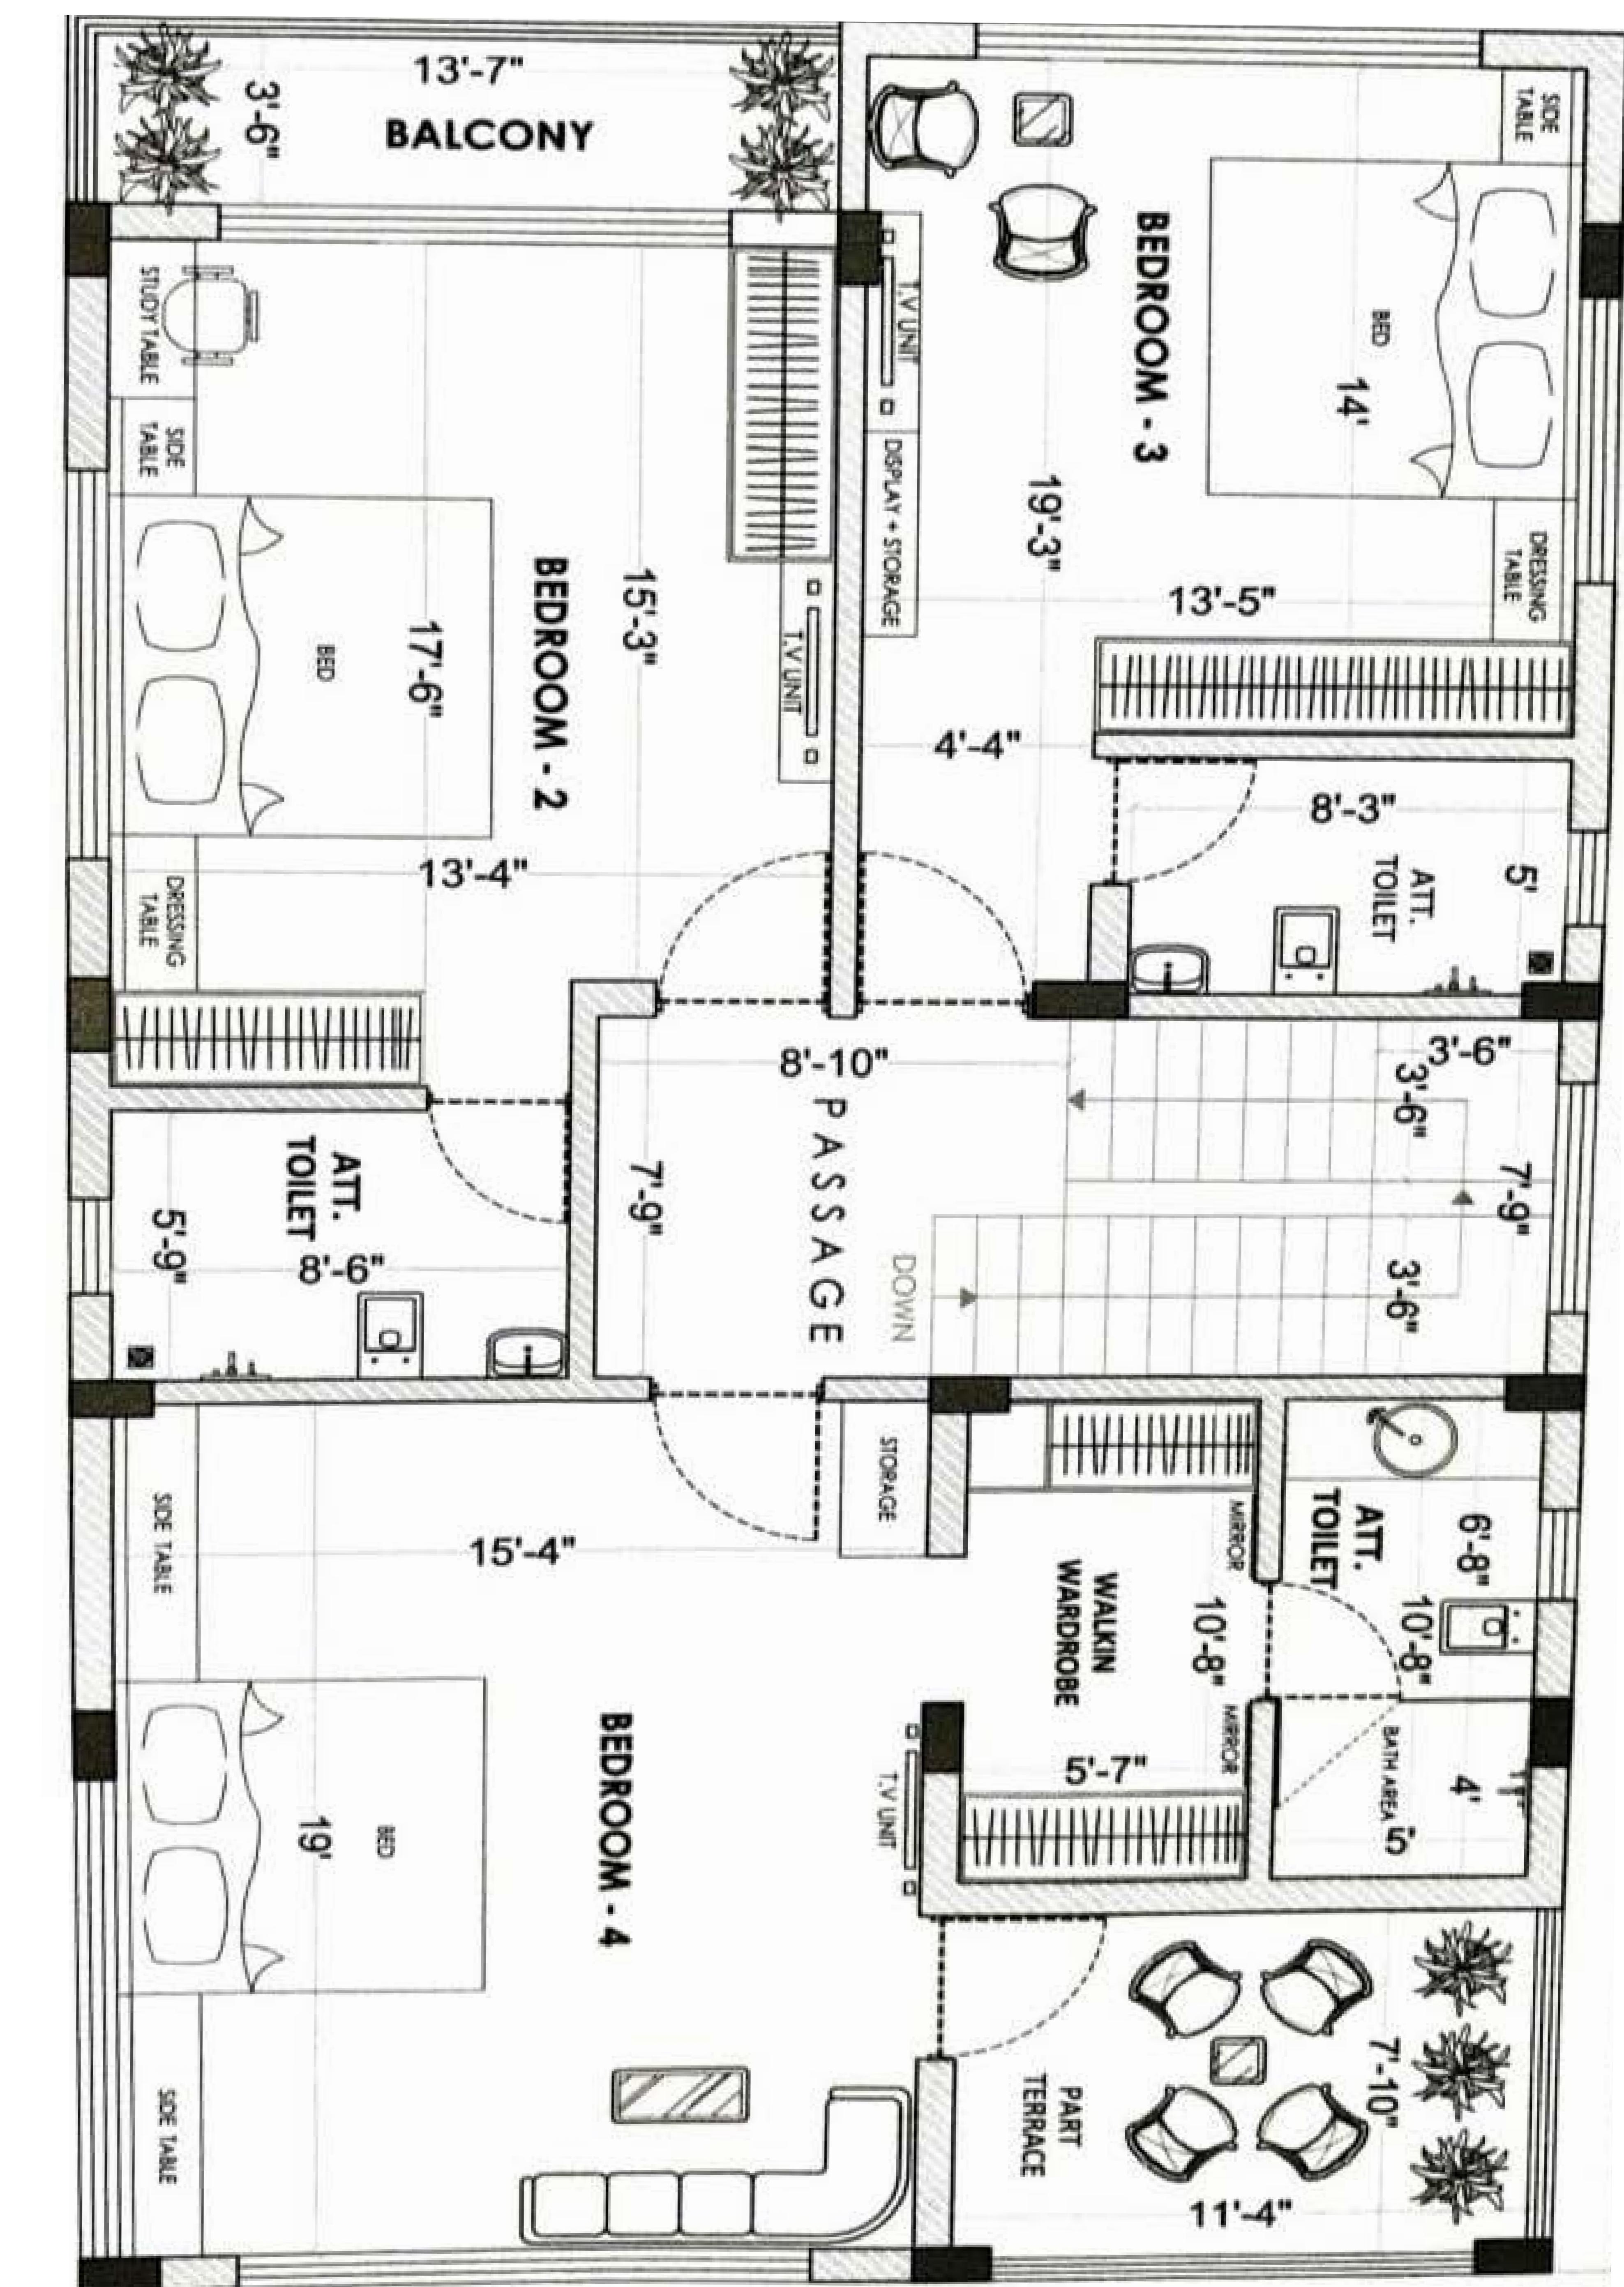

First Floor

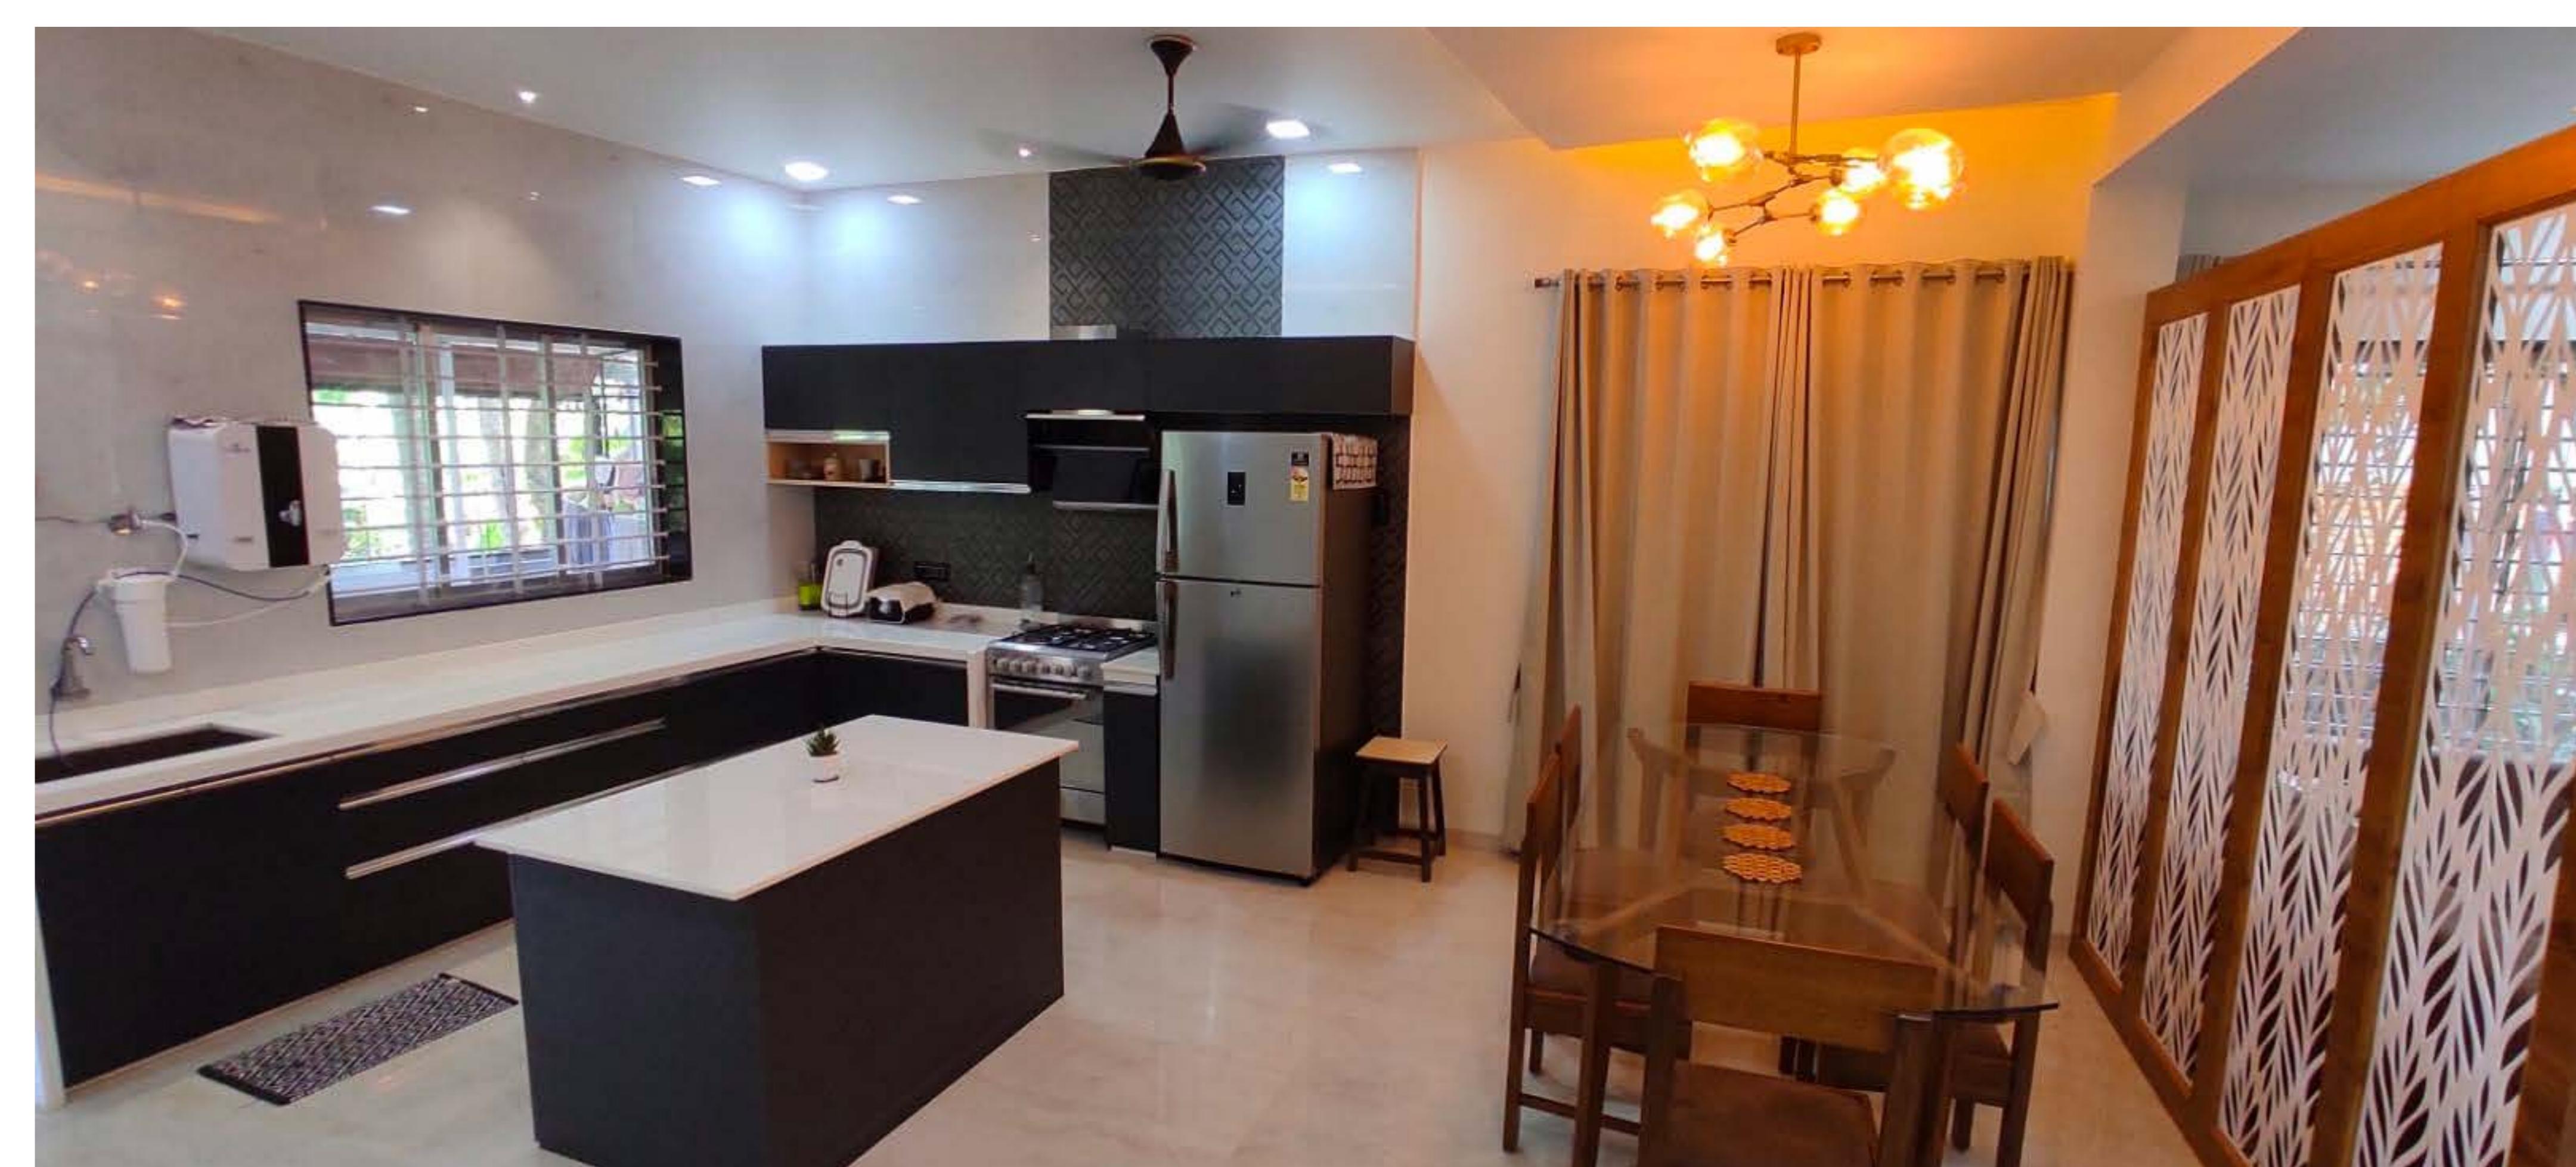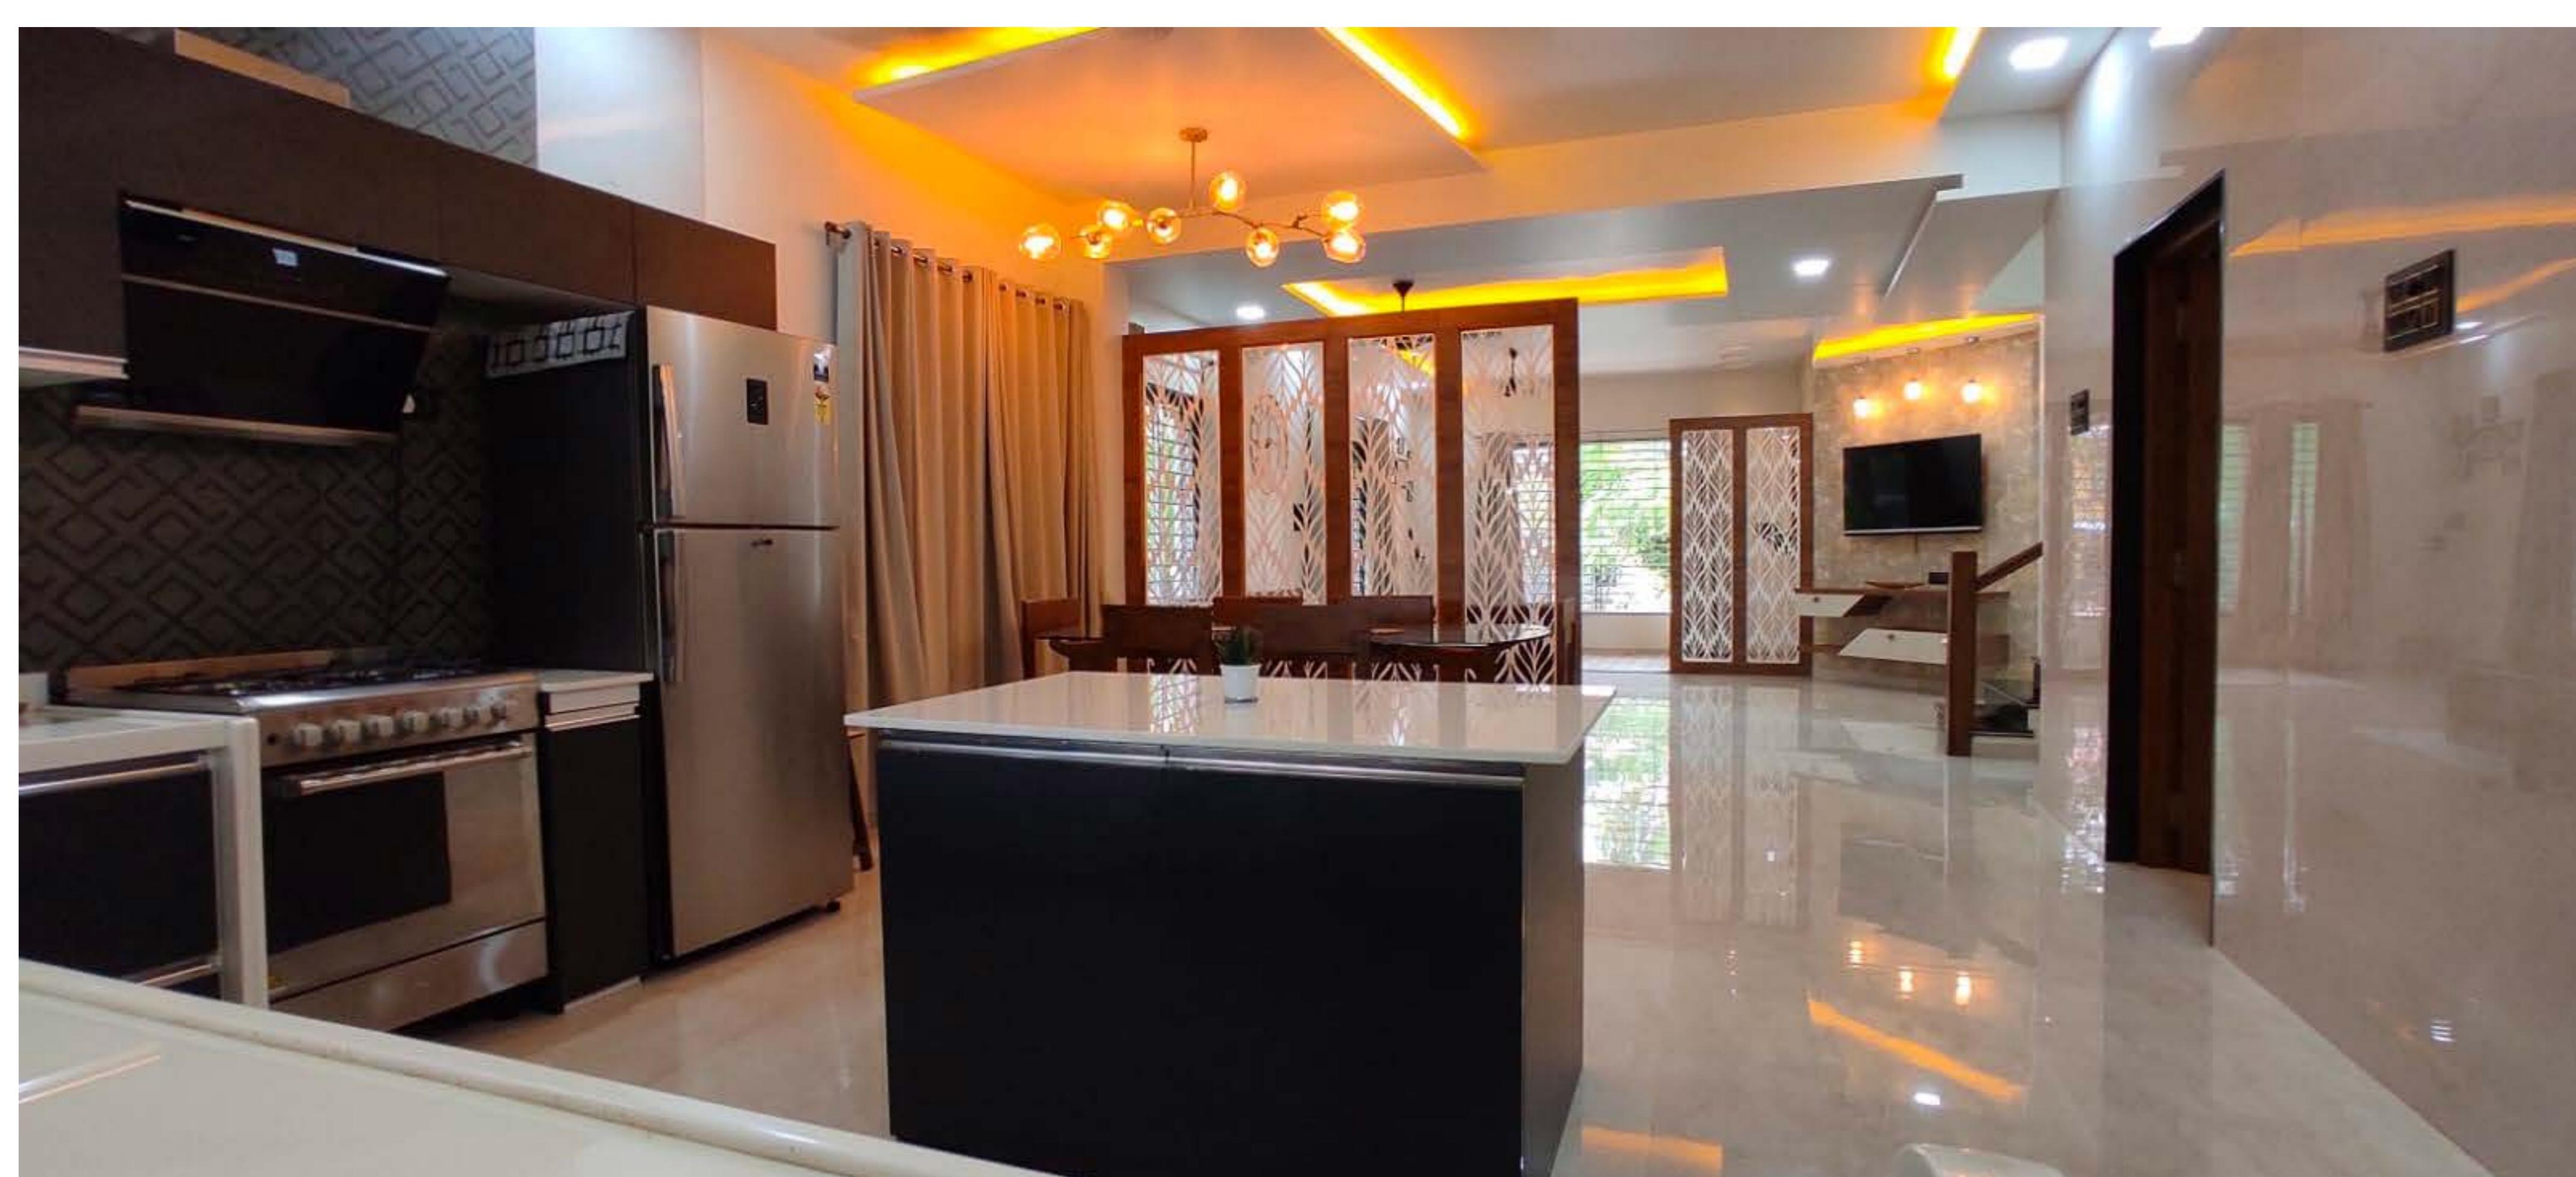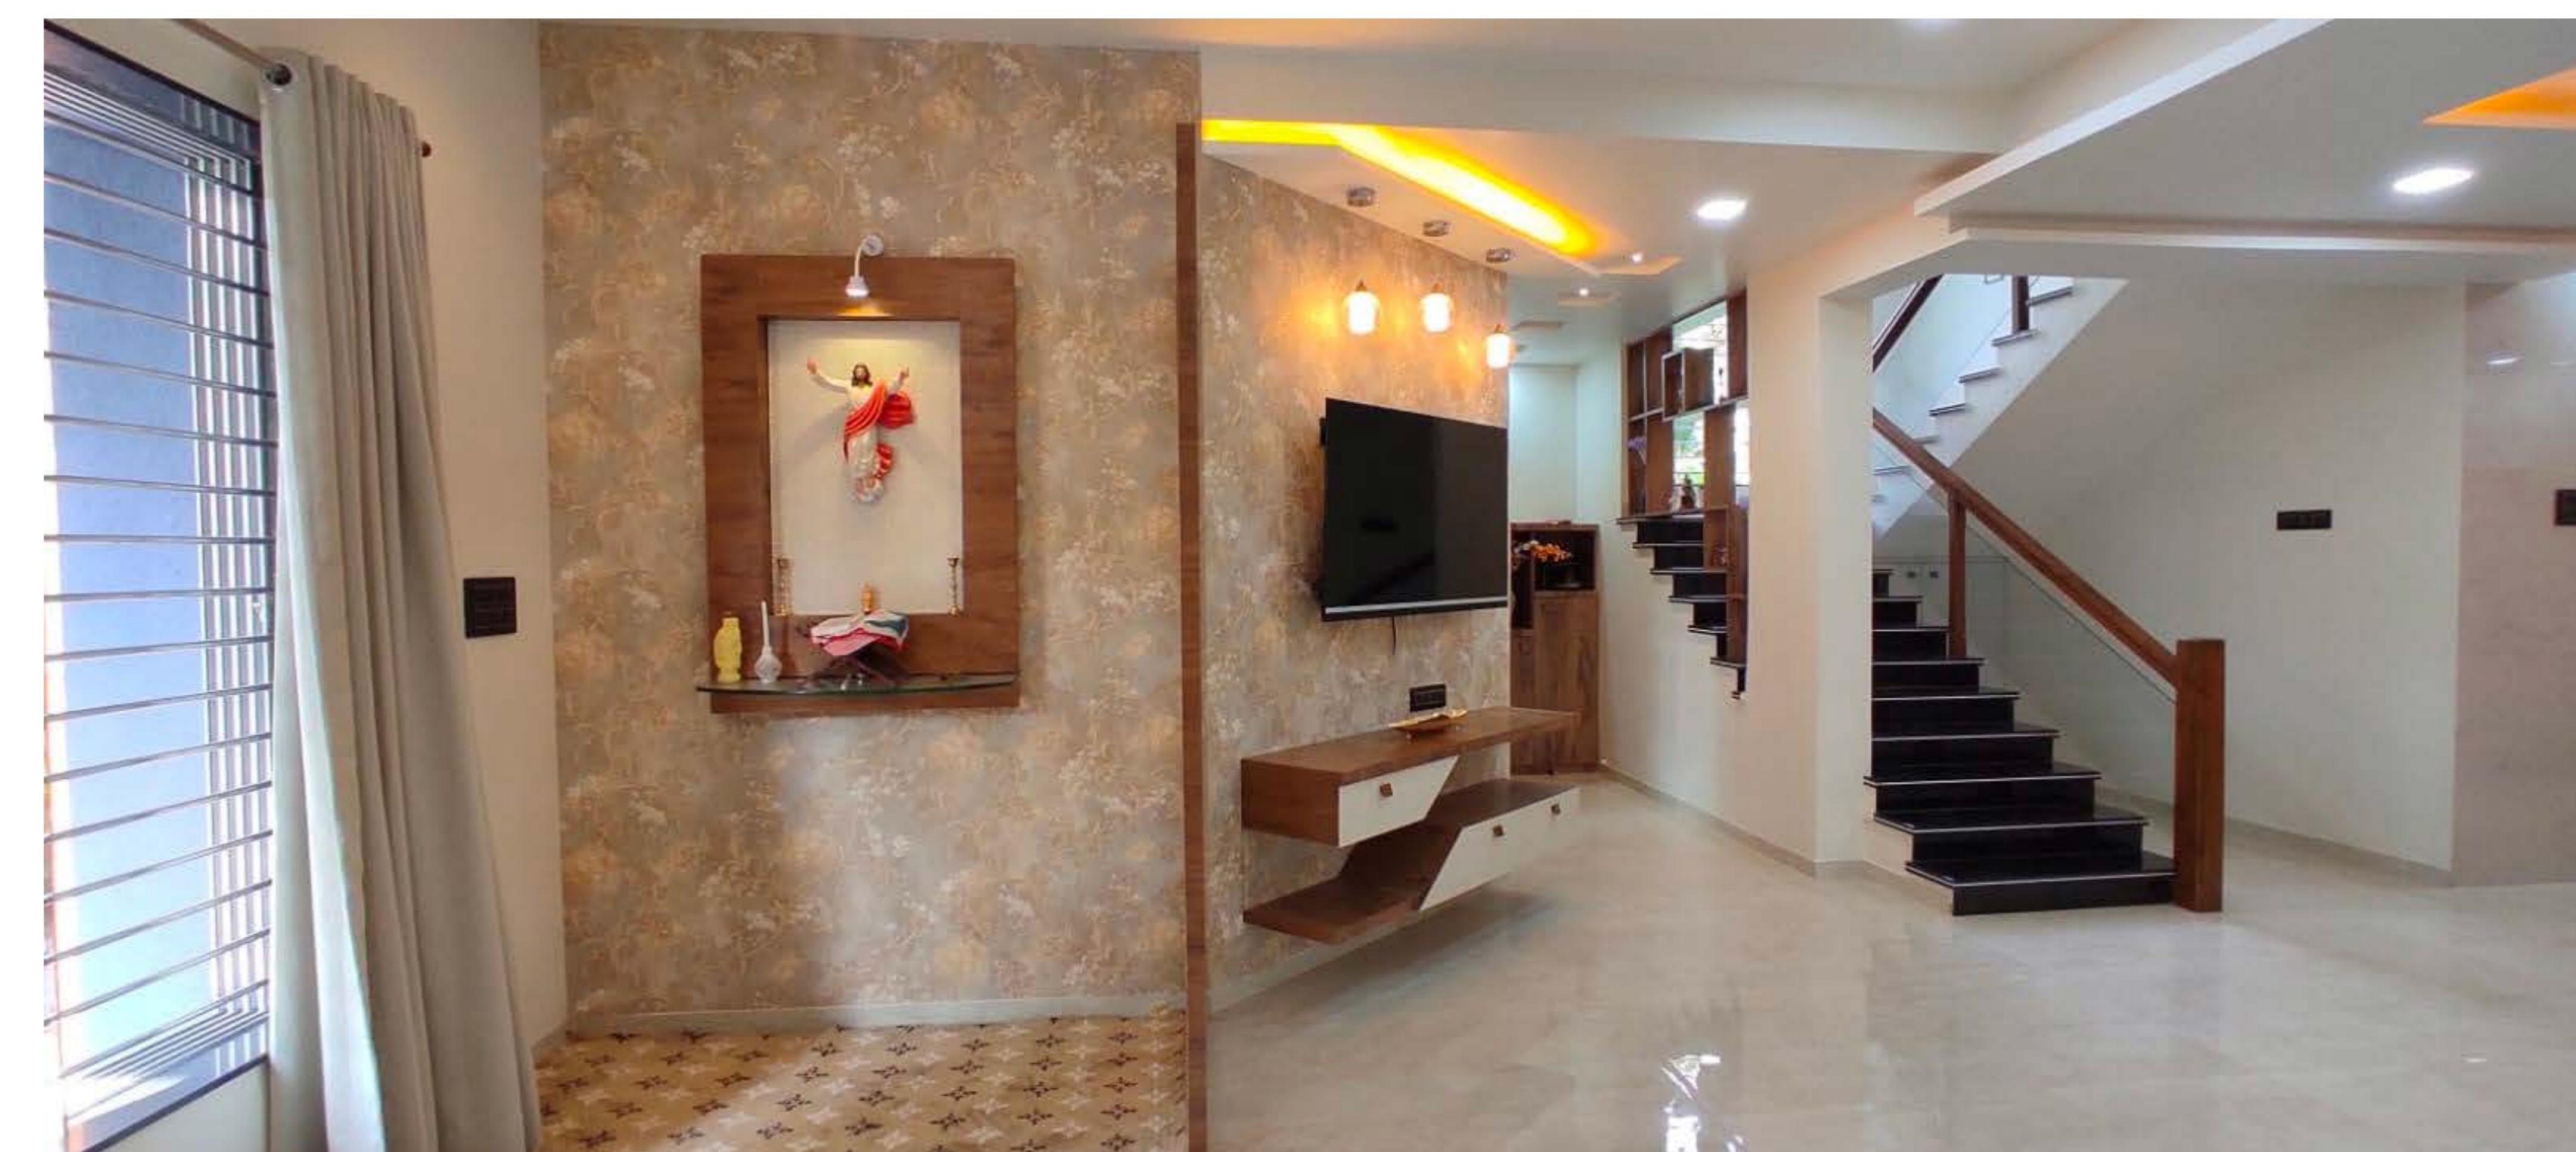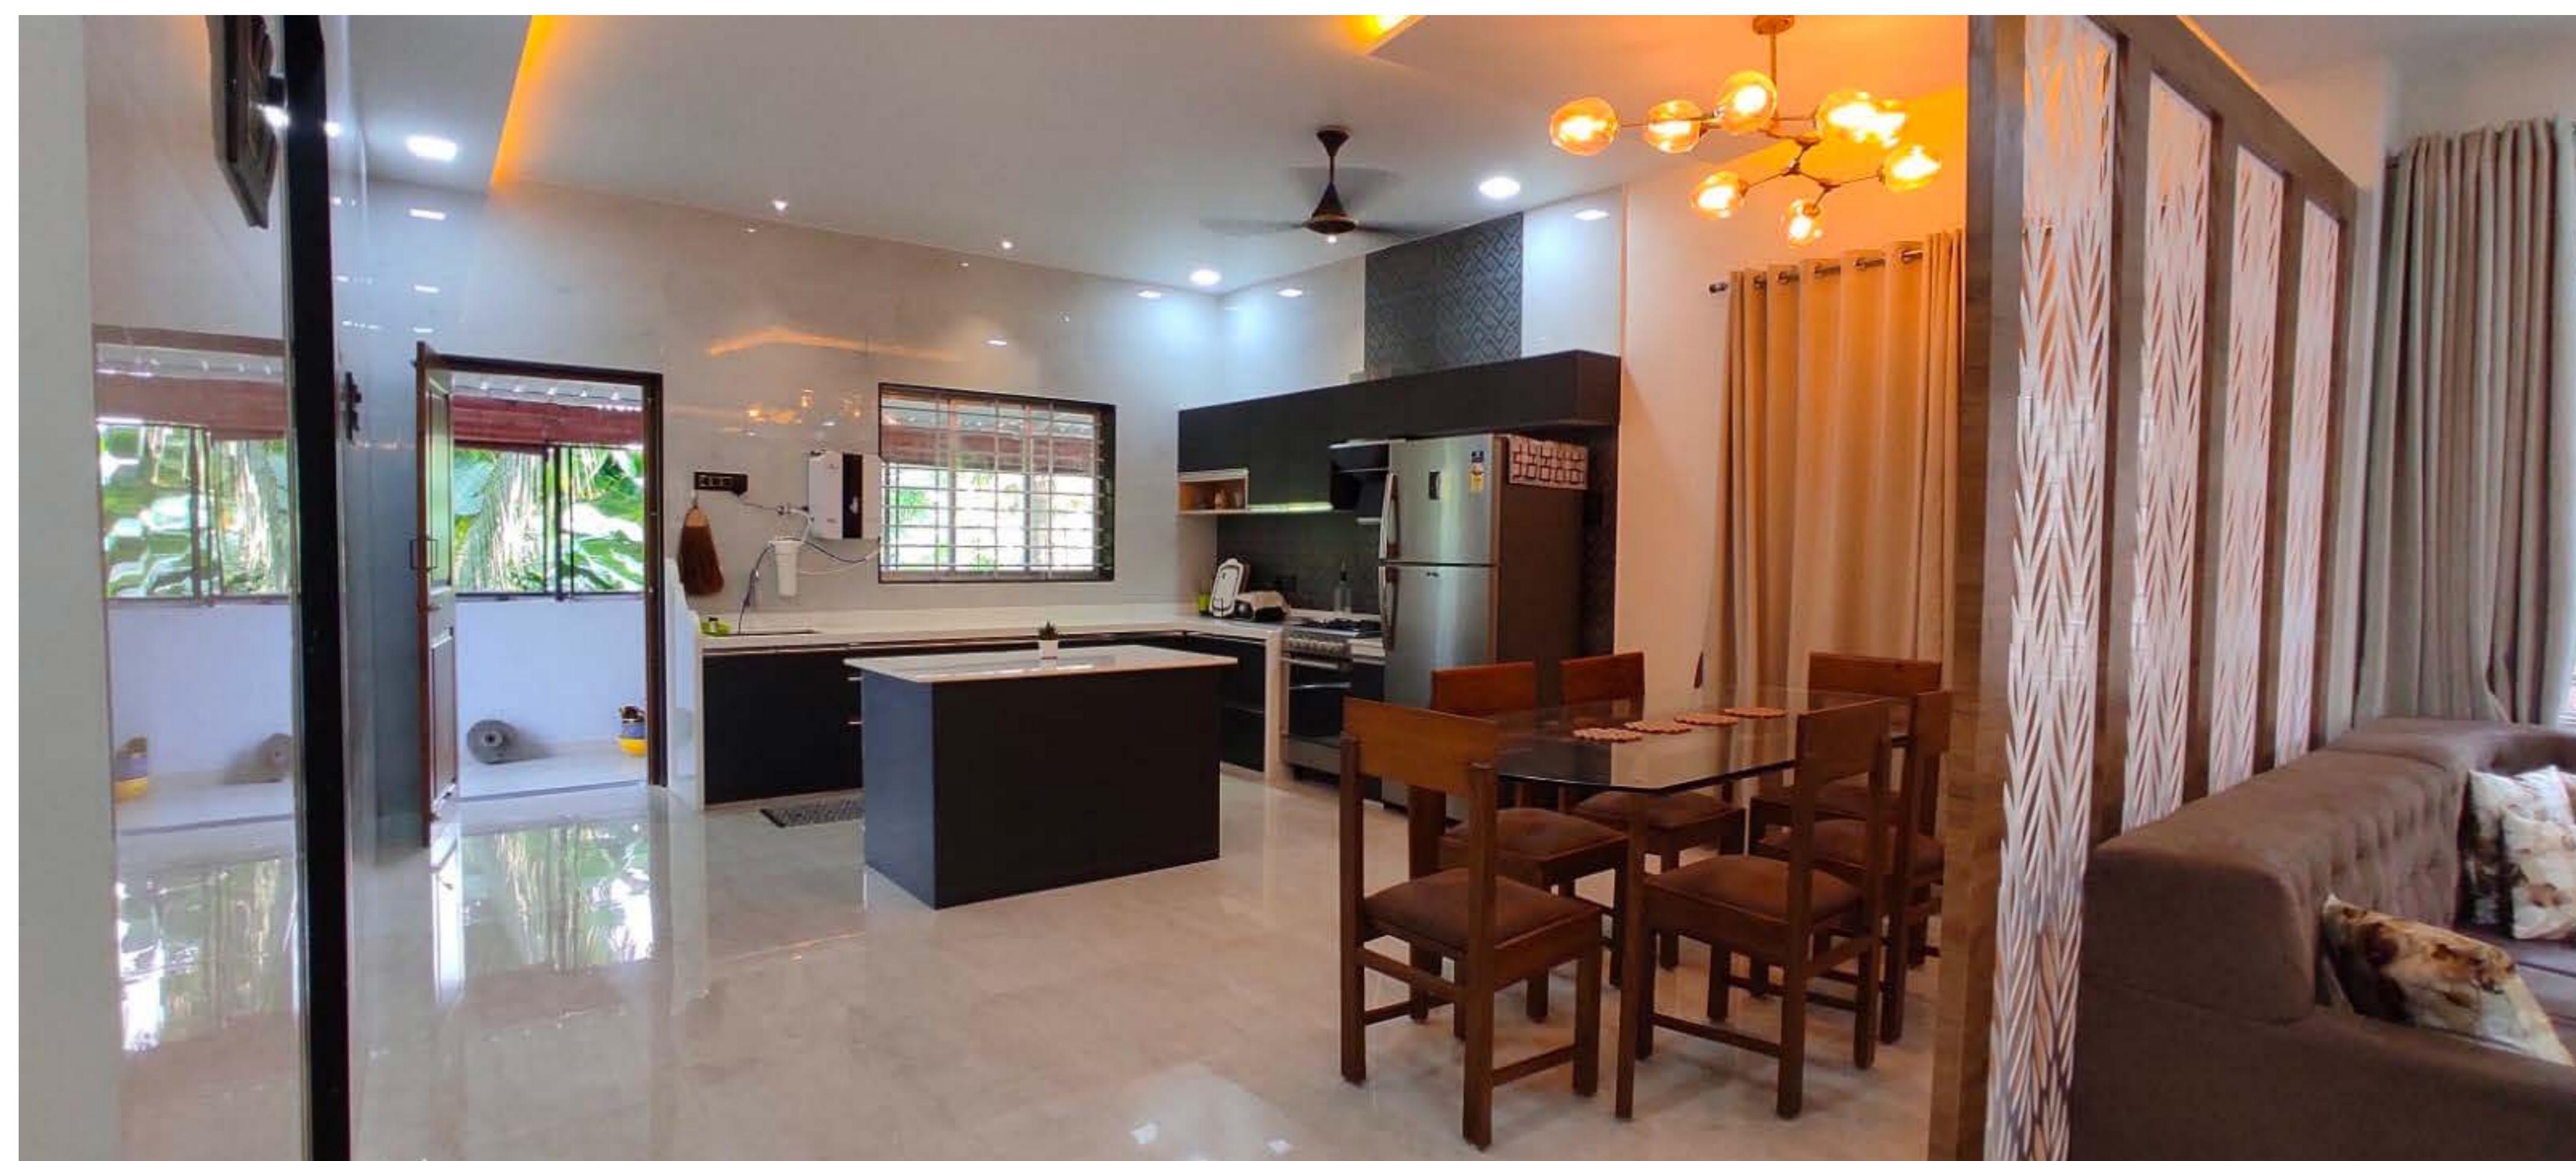

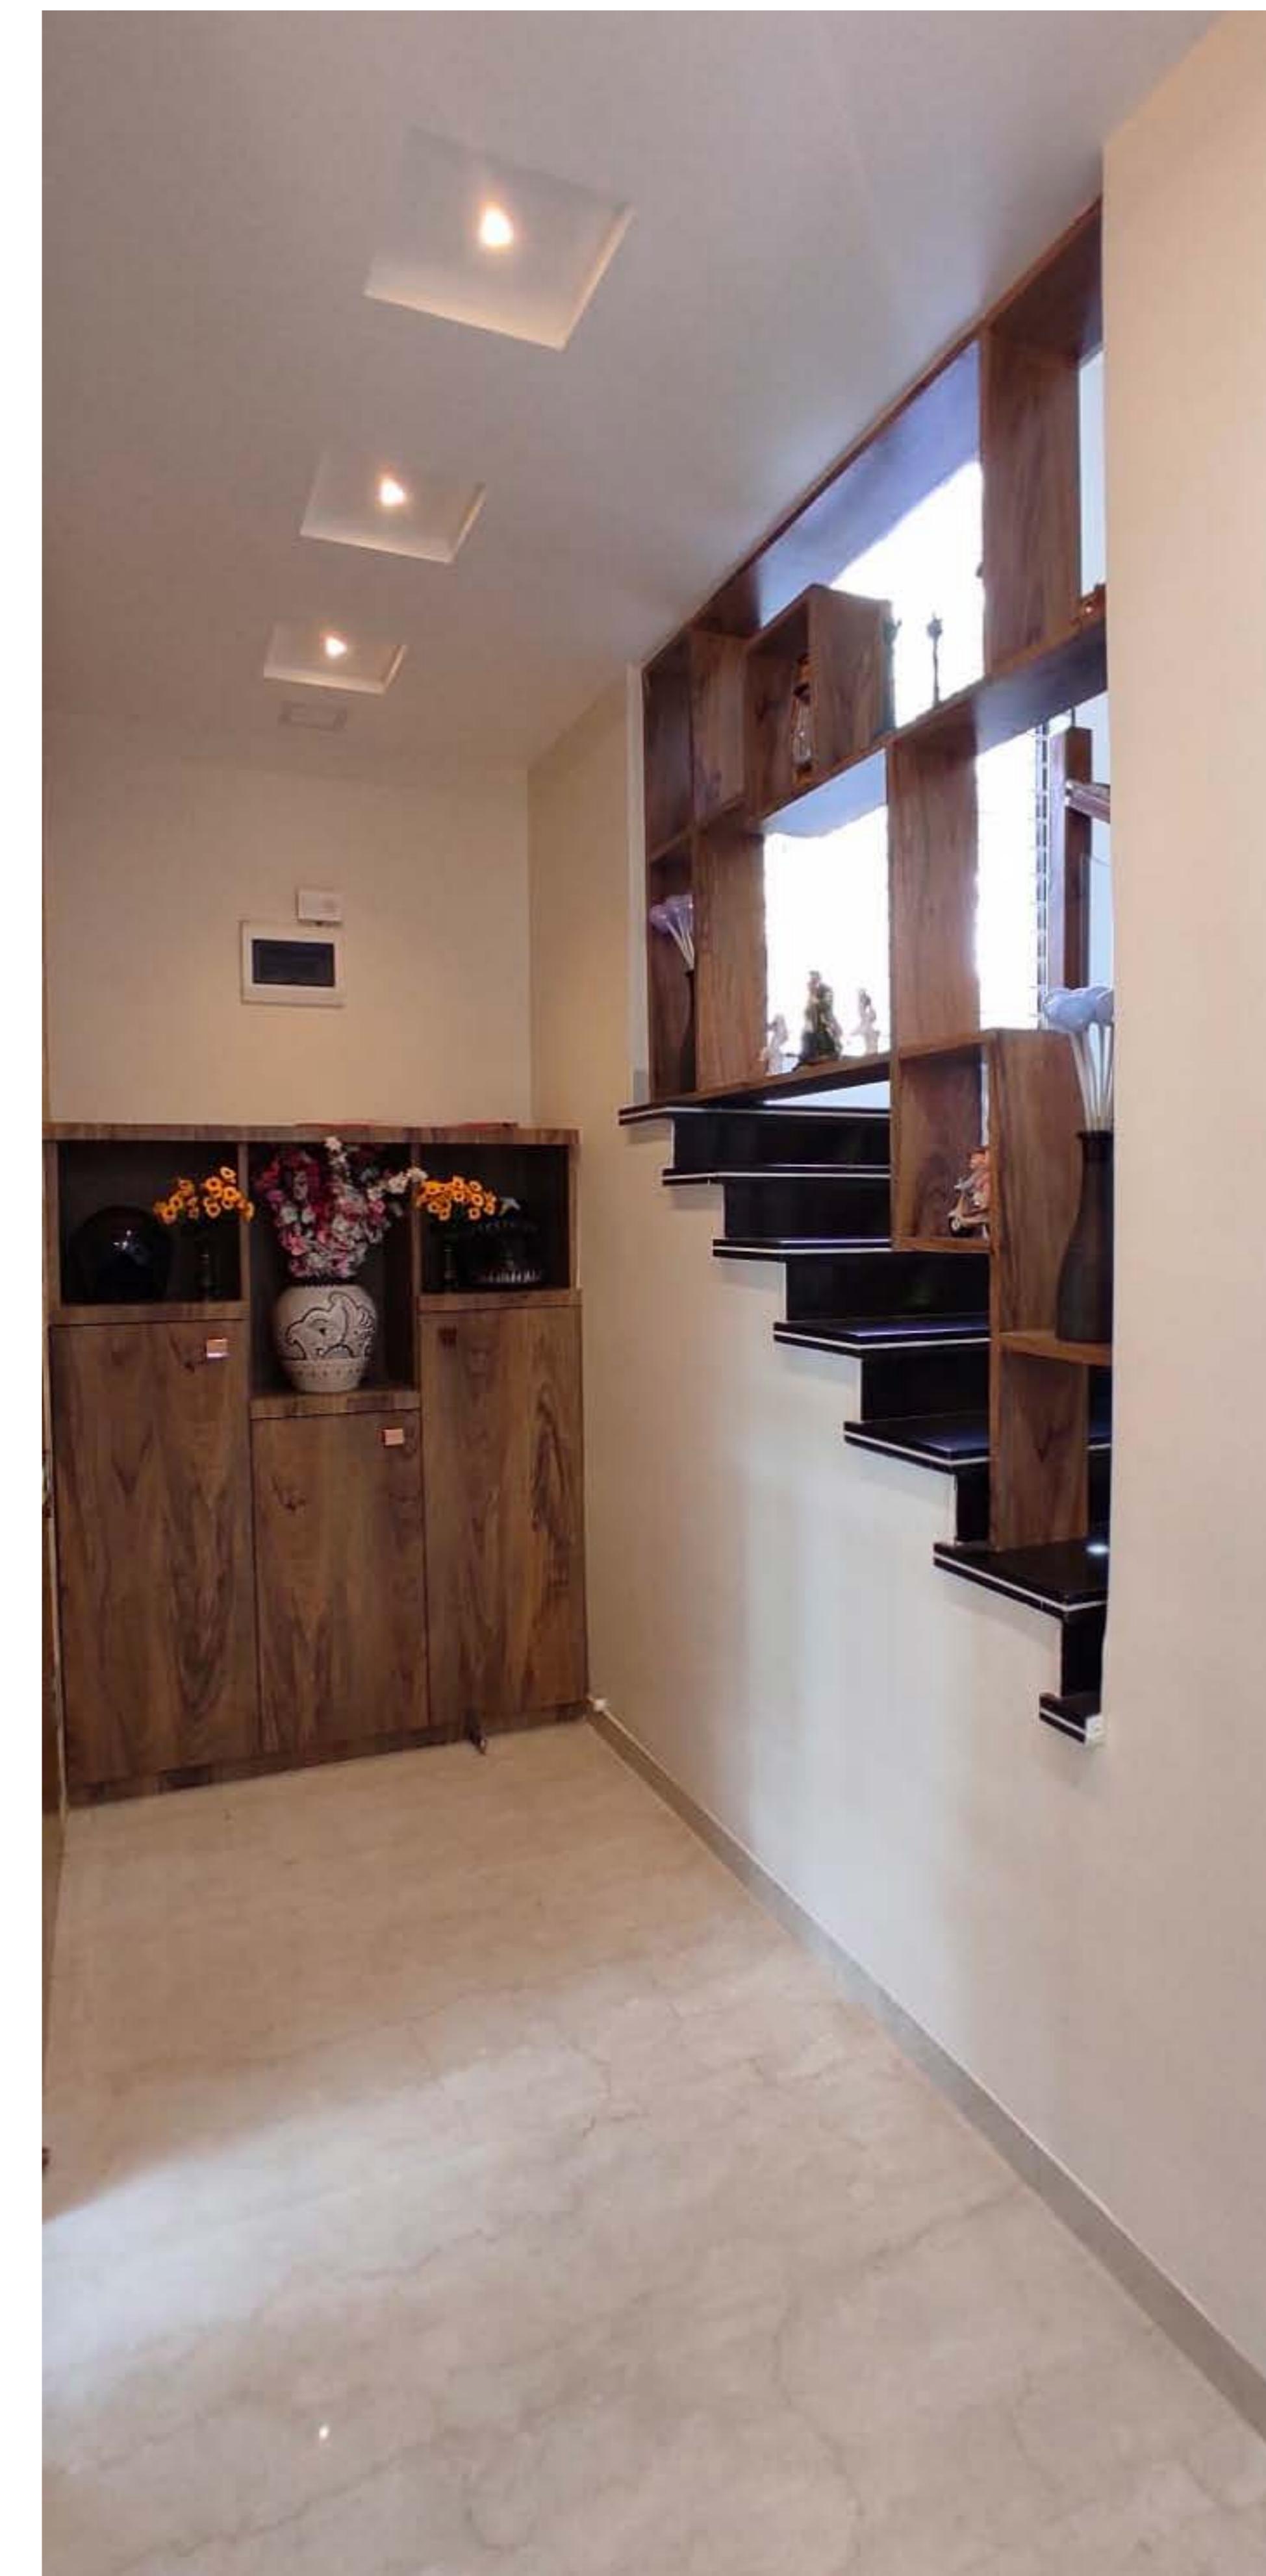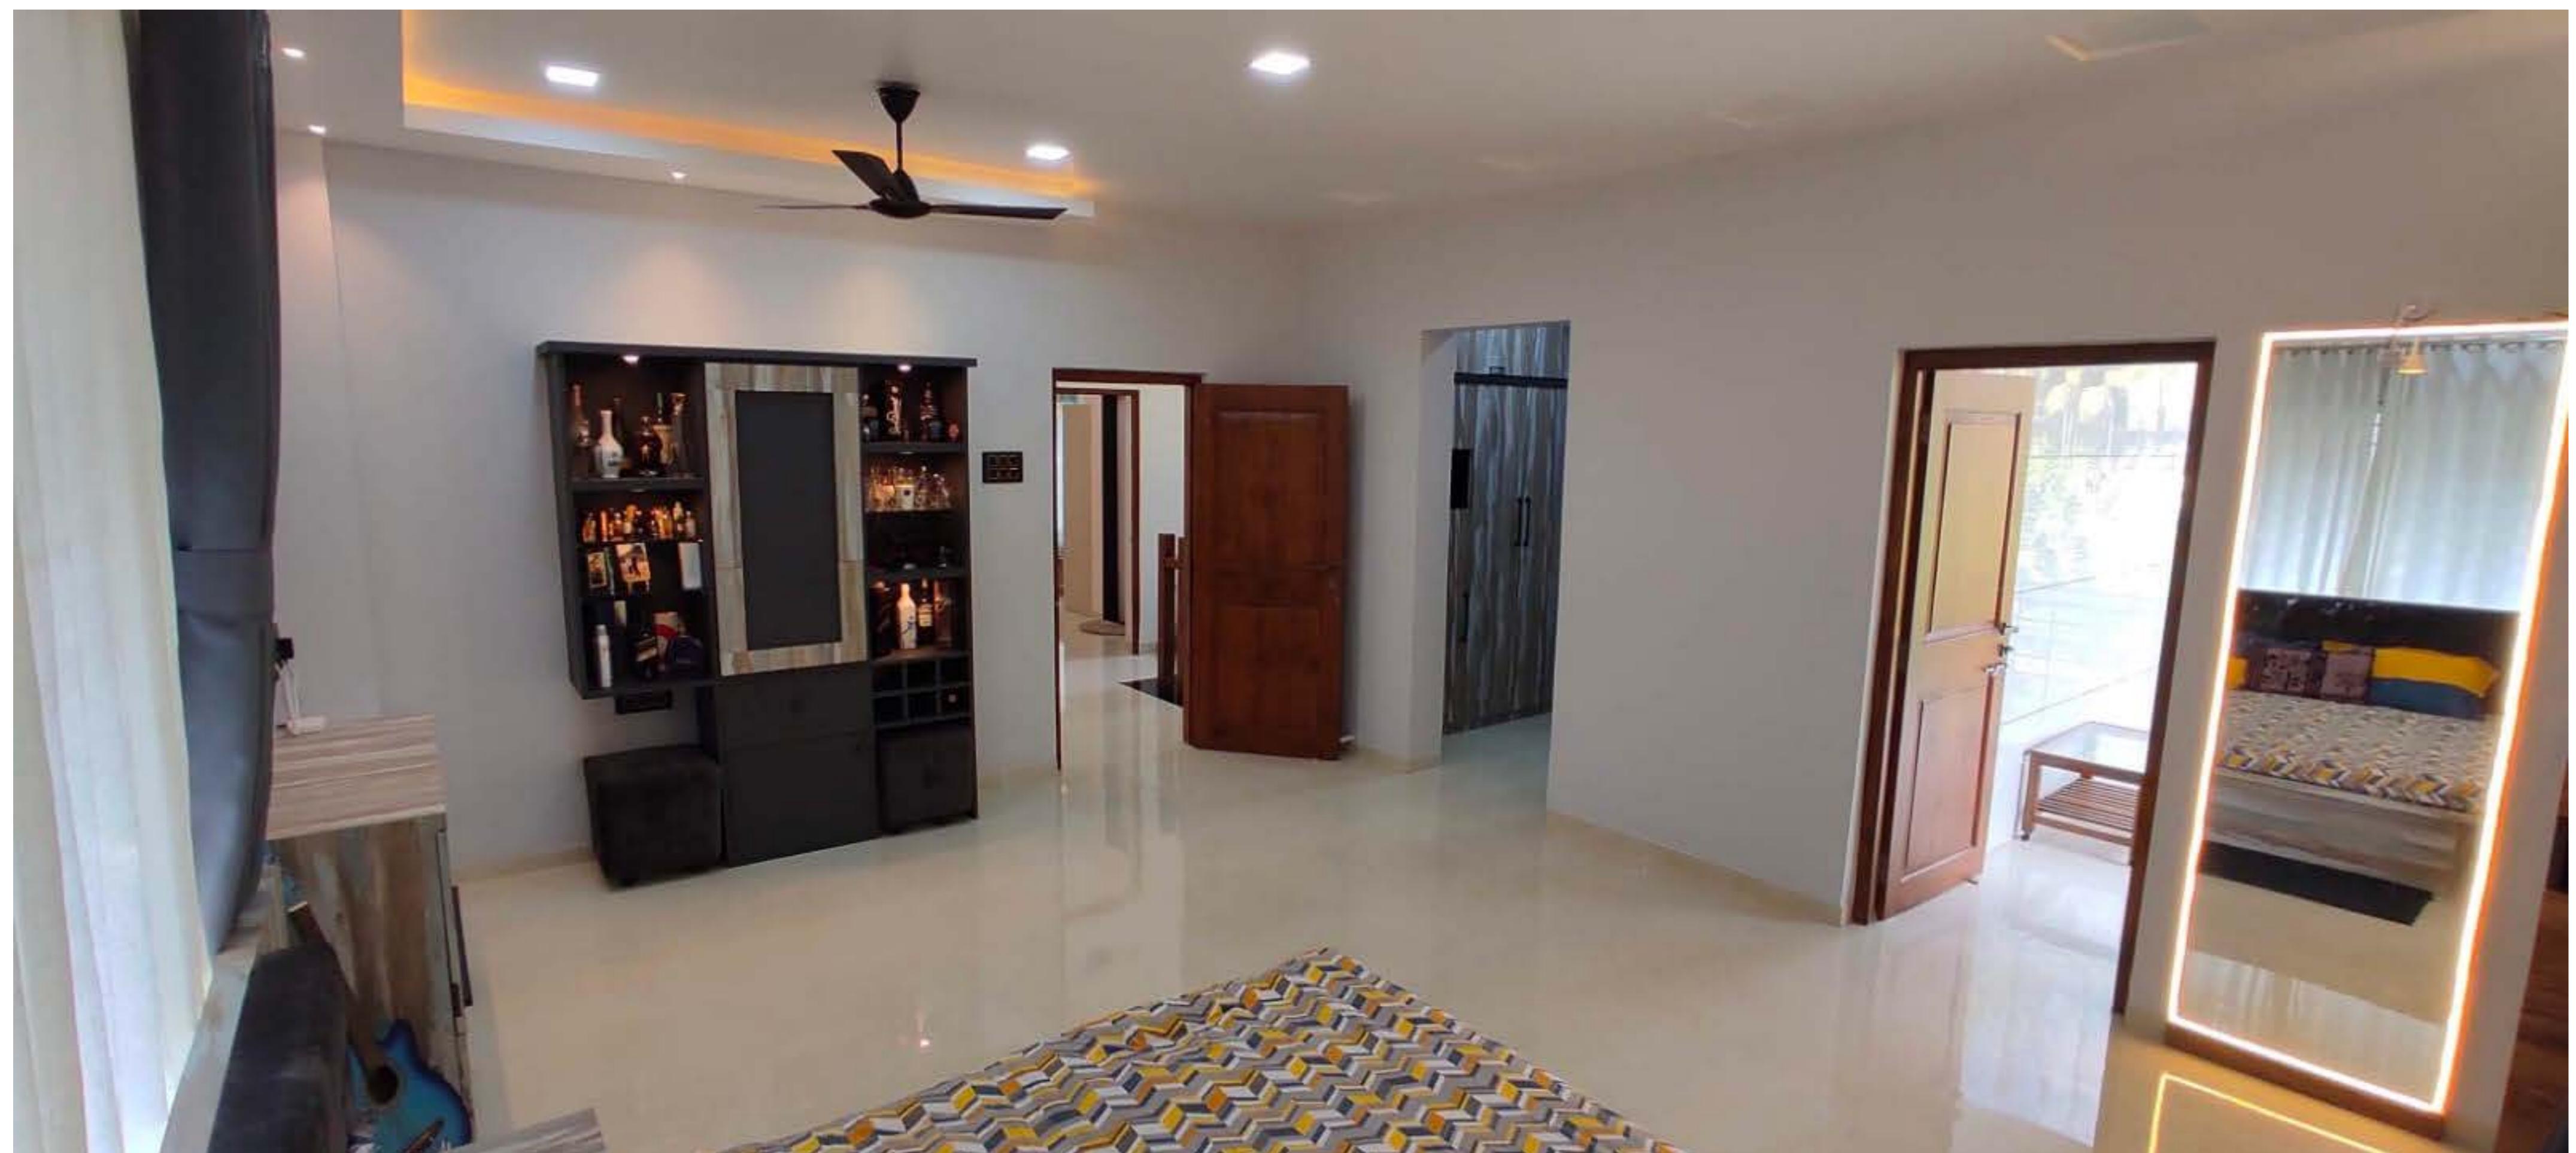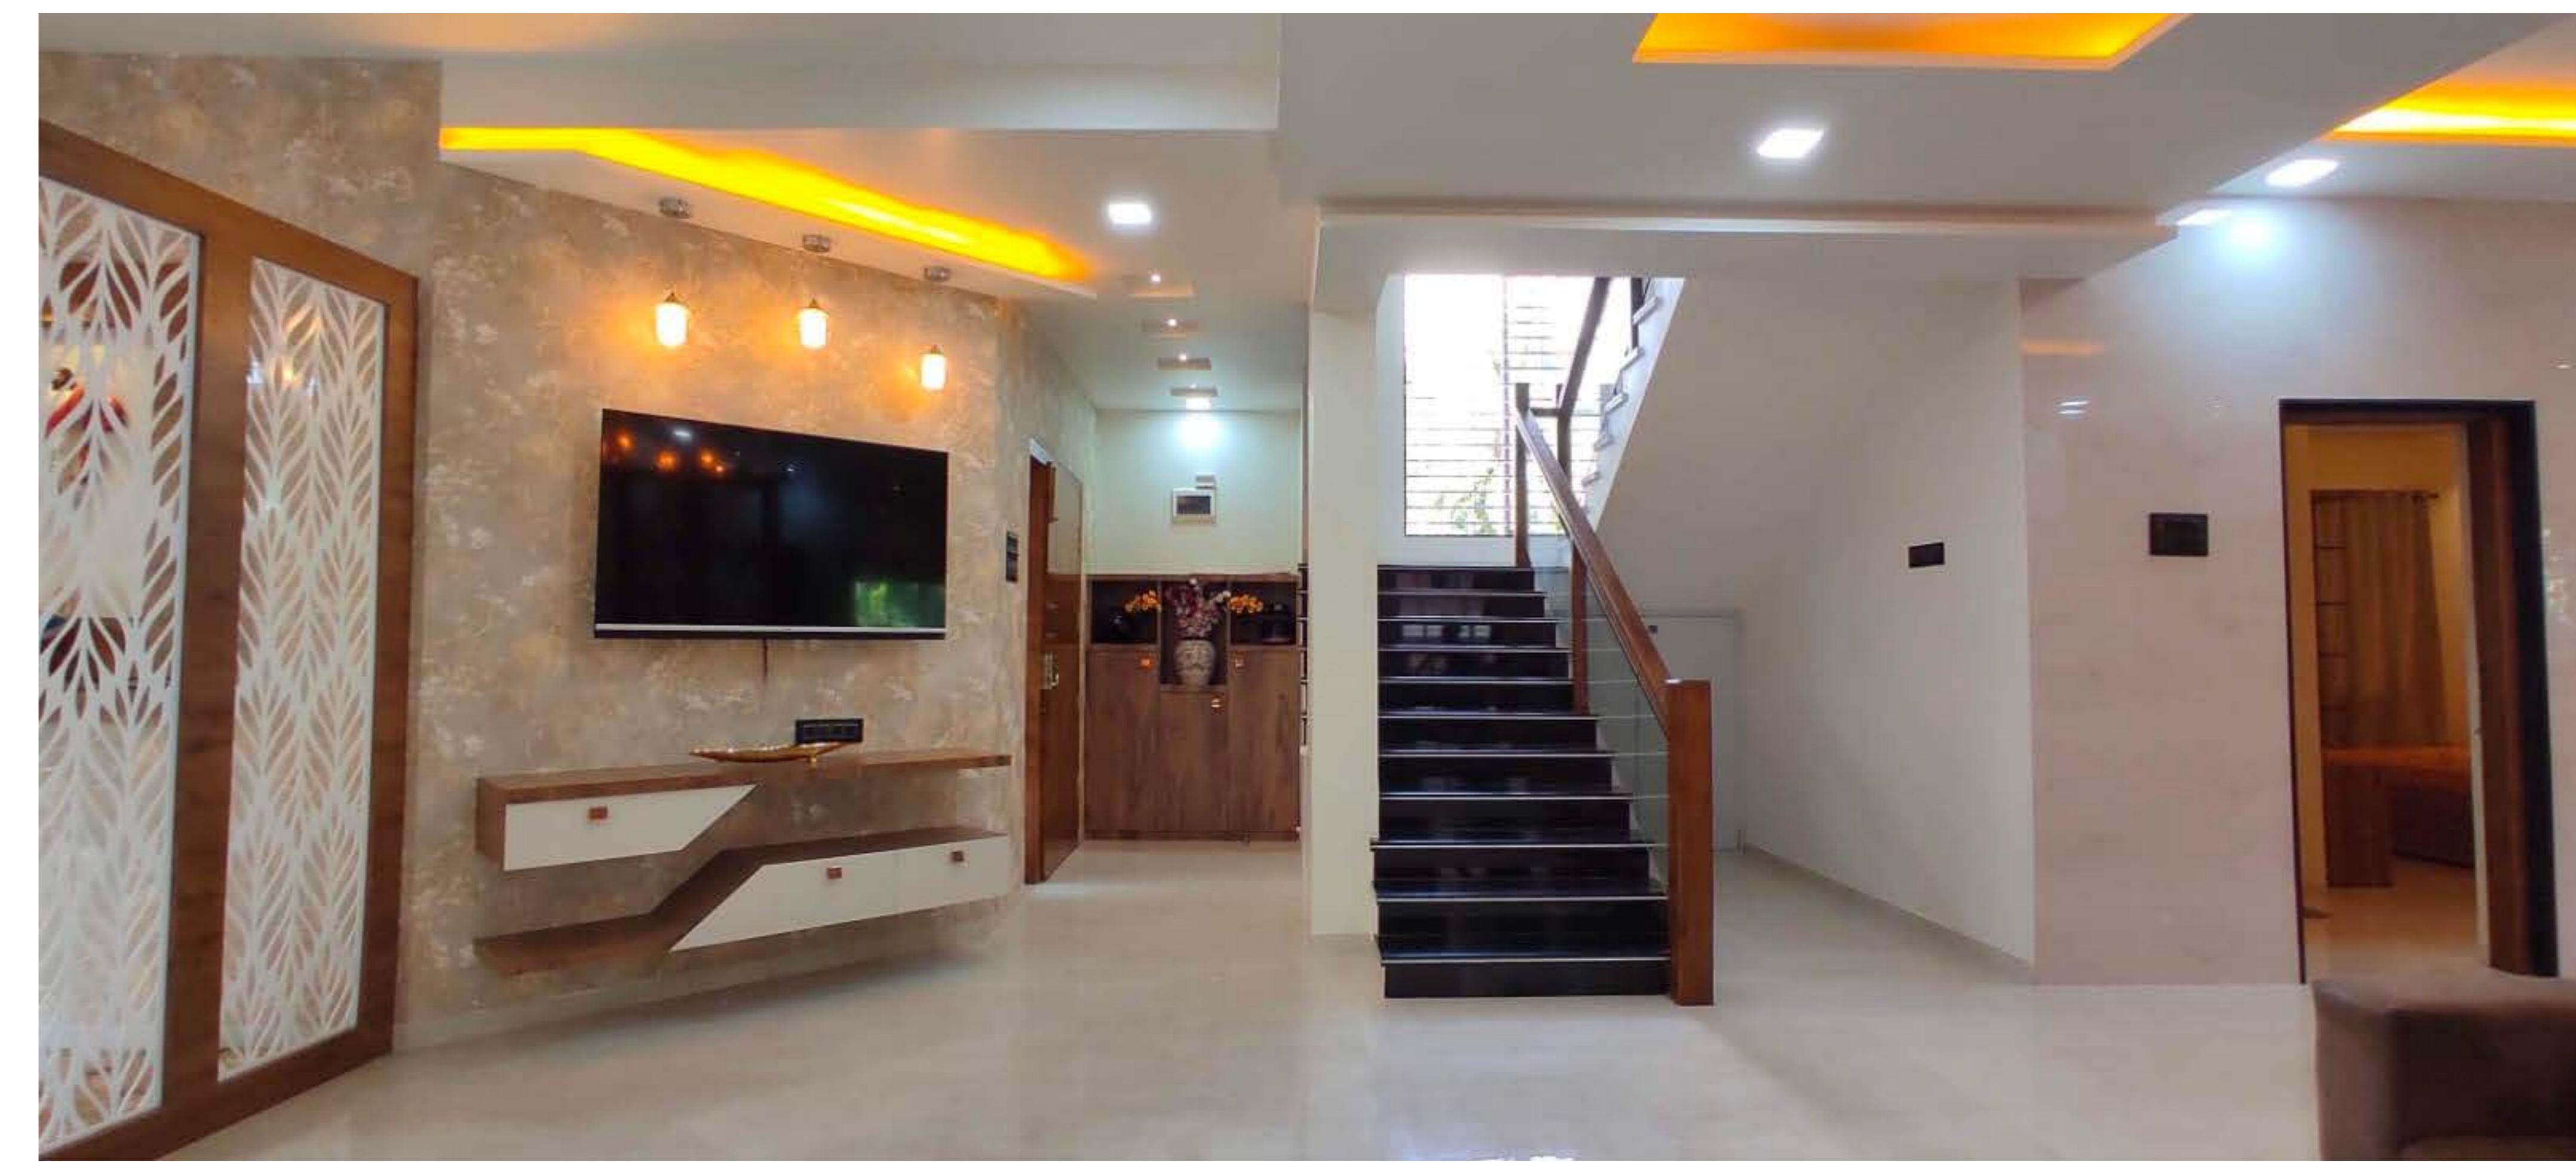

# Restaurant Design

Semester V

The world got busy for their life, especially due to pandemic people need the place to relax and feel calm.

The main purpose of this project is to make people feel comfortable with natural modern mood.

Theme

TROPICAL STYLE

COMFORT,EASE,UTILITY



STYLE CHARACTERISED BY MODERN LOOK

COLOUR THEME ACCORDING TO THE NATURE USE OF NEUTRAL COLOURS









Area - 4810 sq.ft

Location- Borivali,Mumbai west

Aim- To create an environment in which people can relax and get comfortable

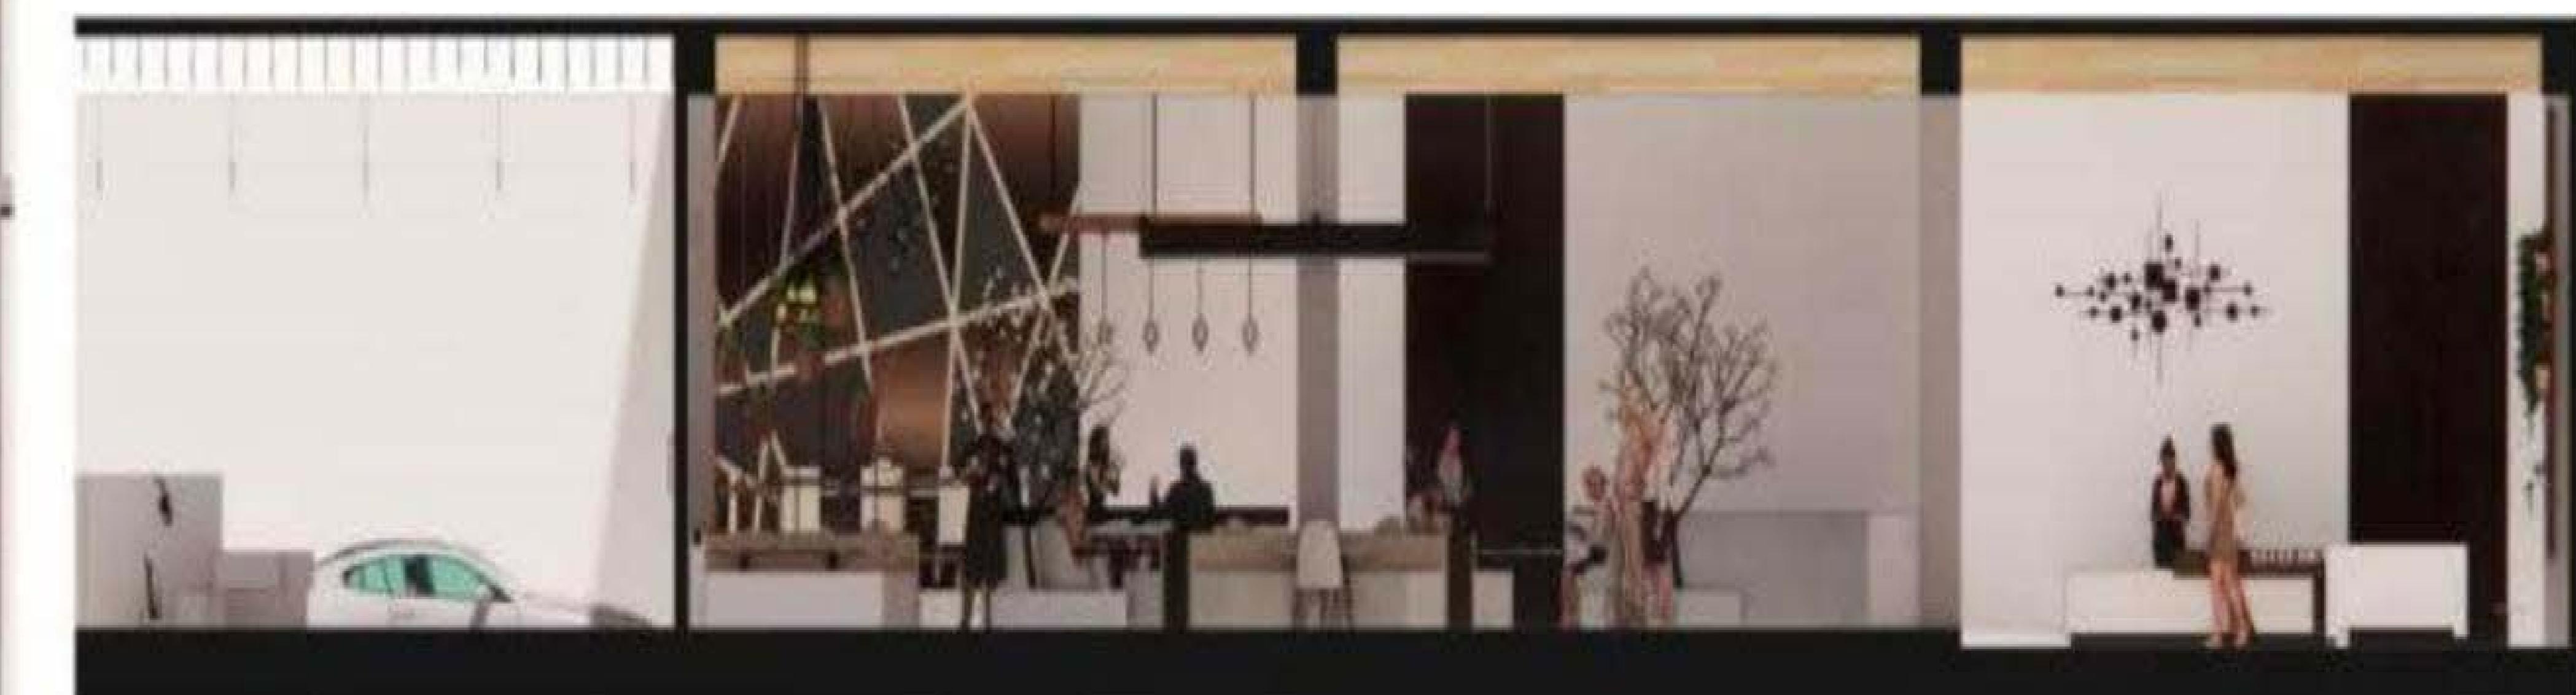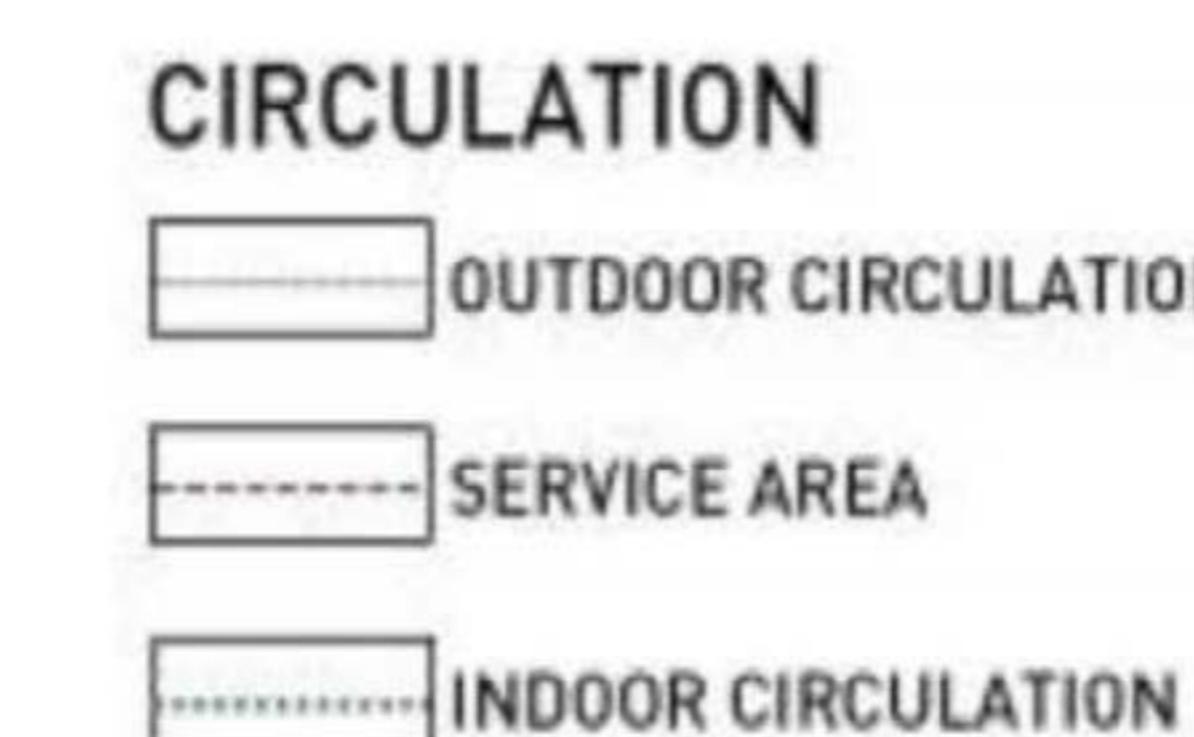


SECTION AA'

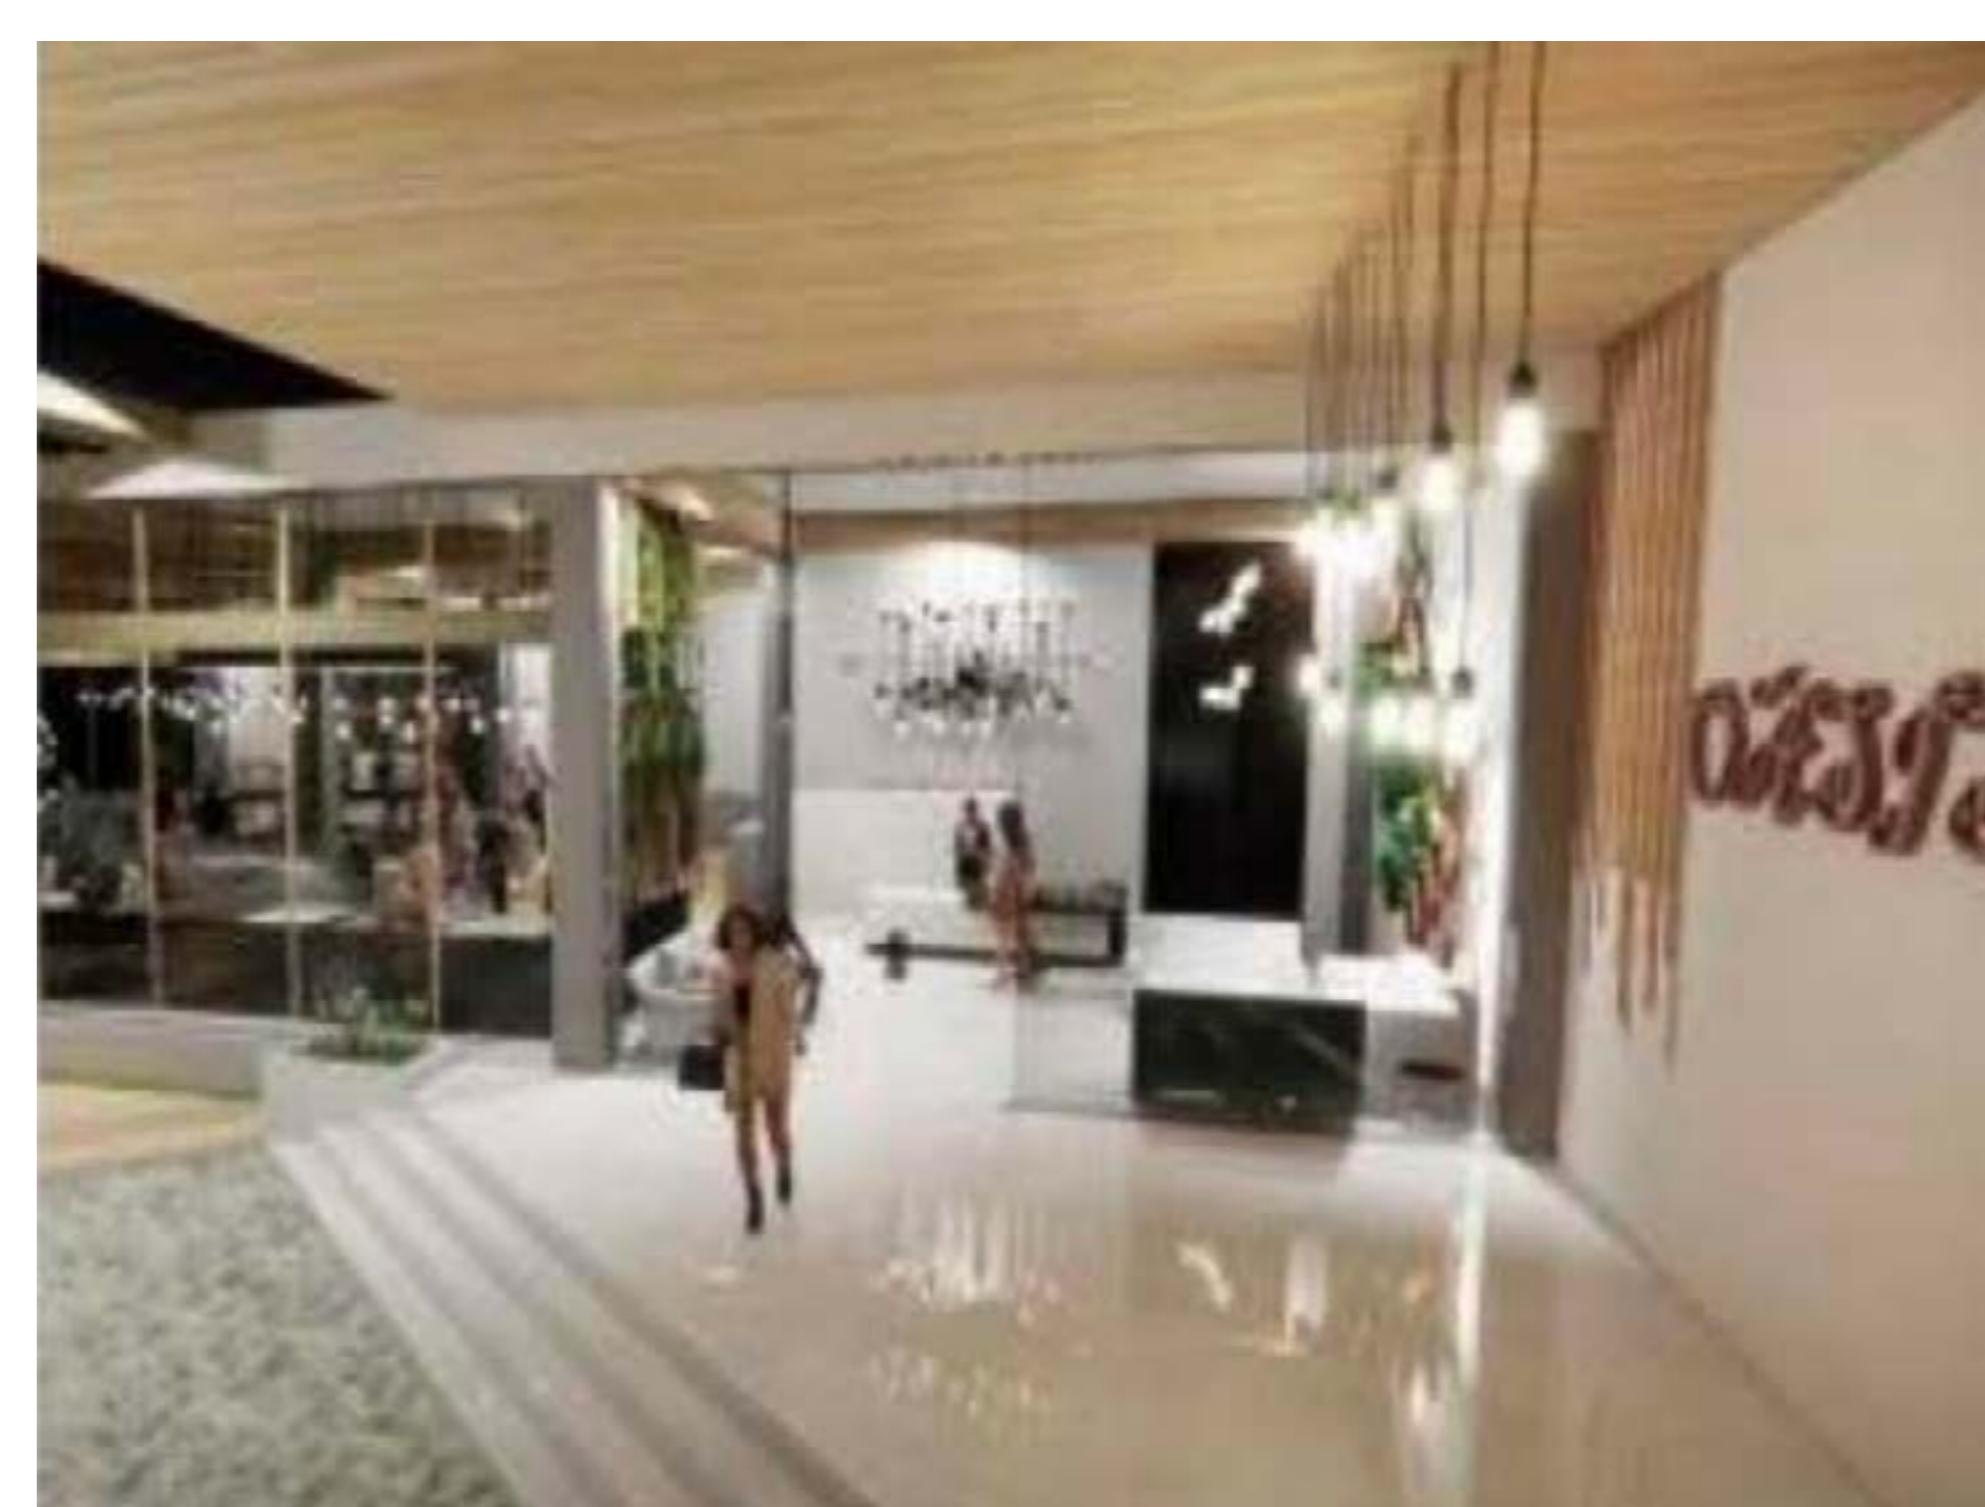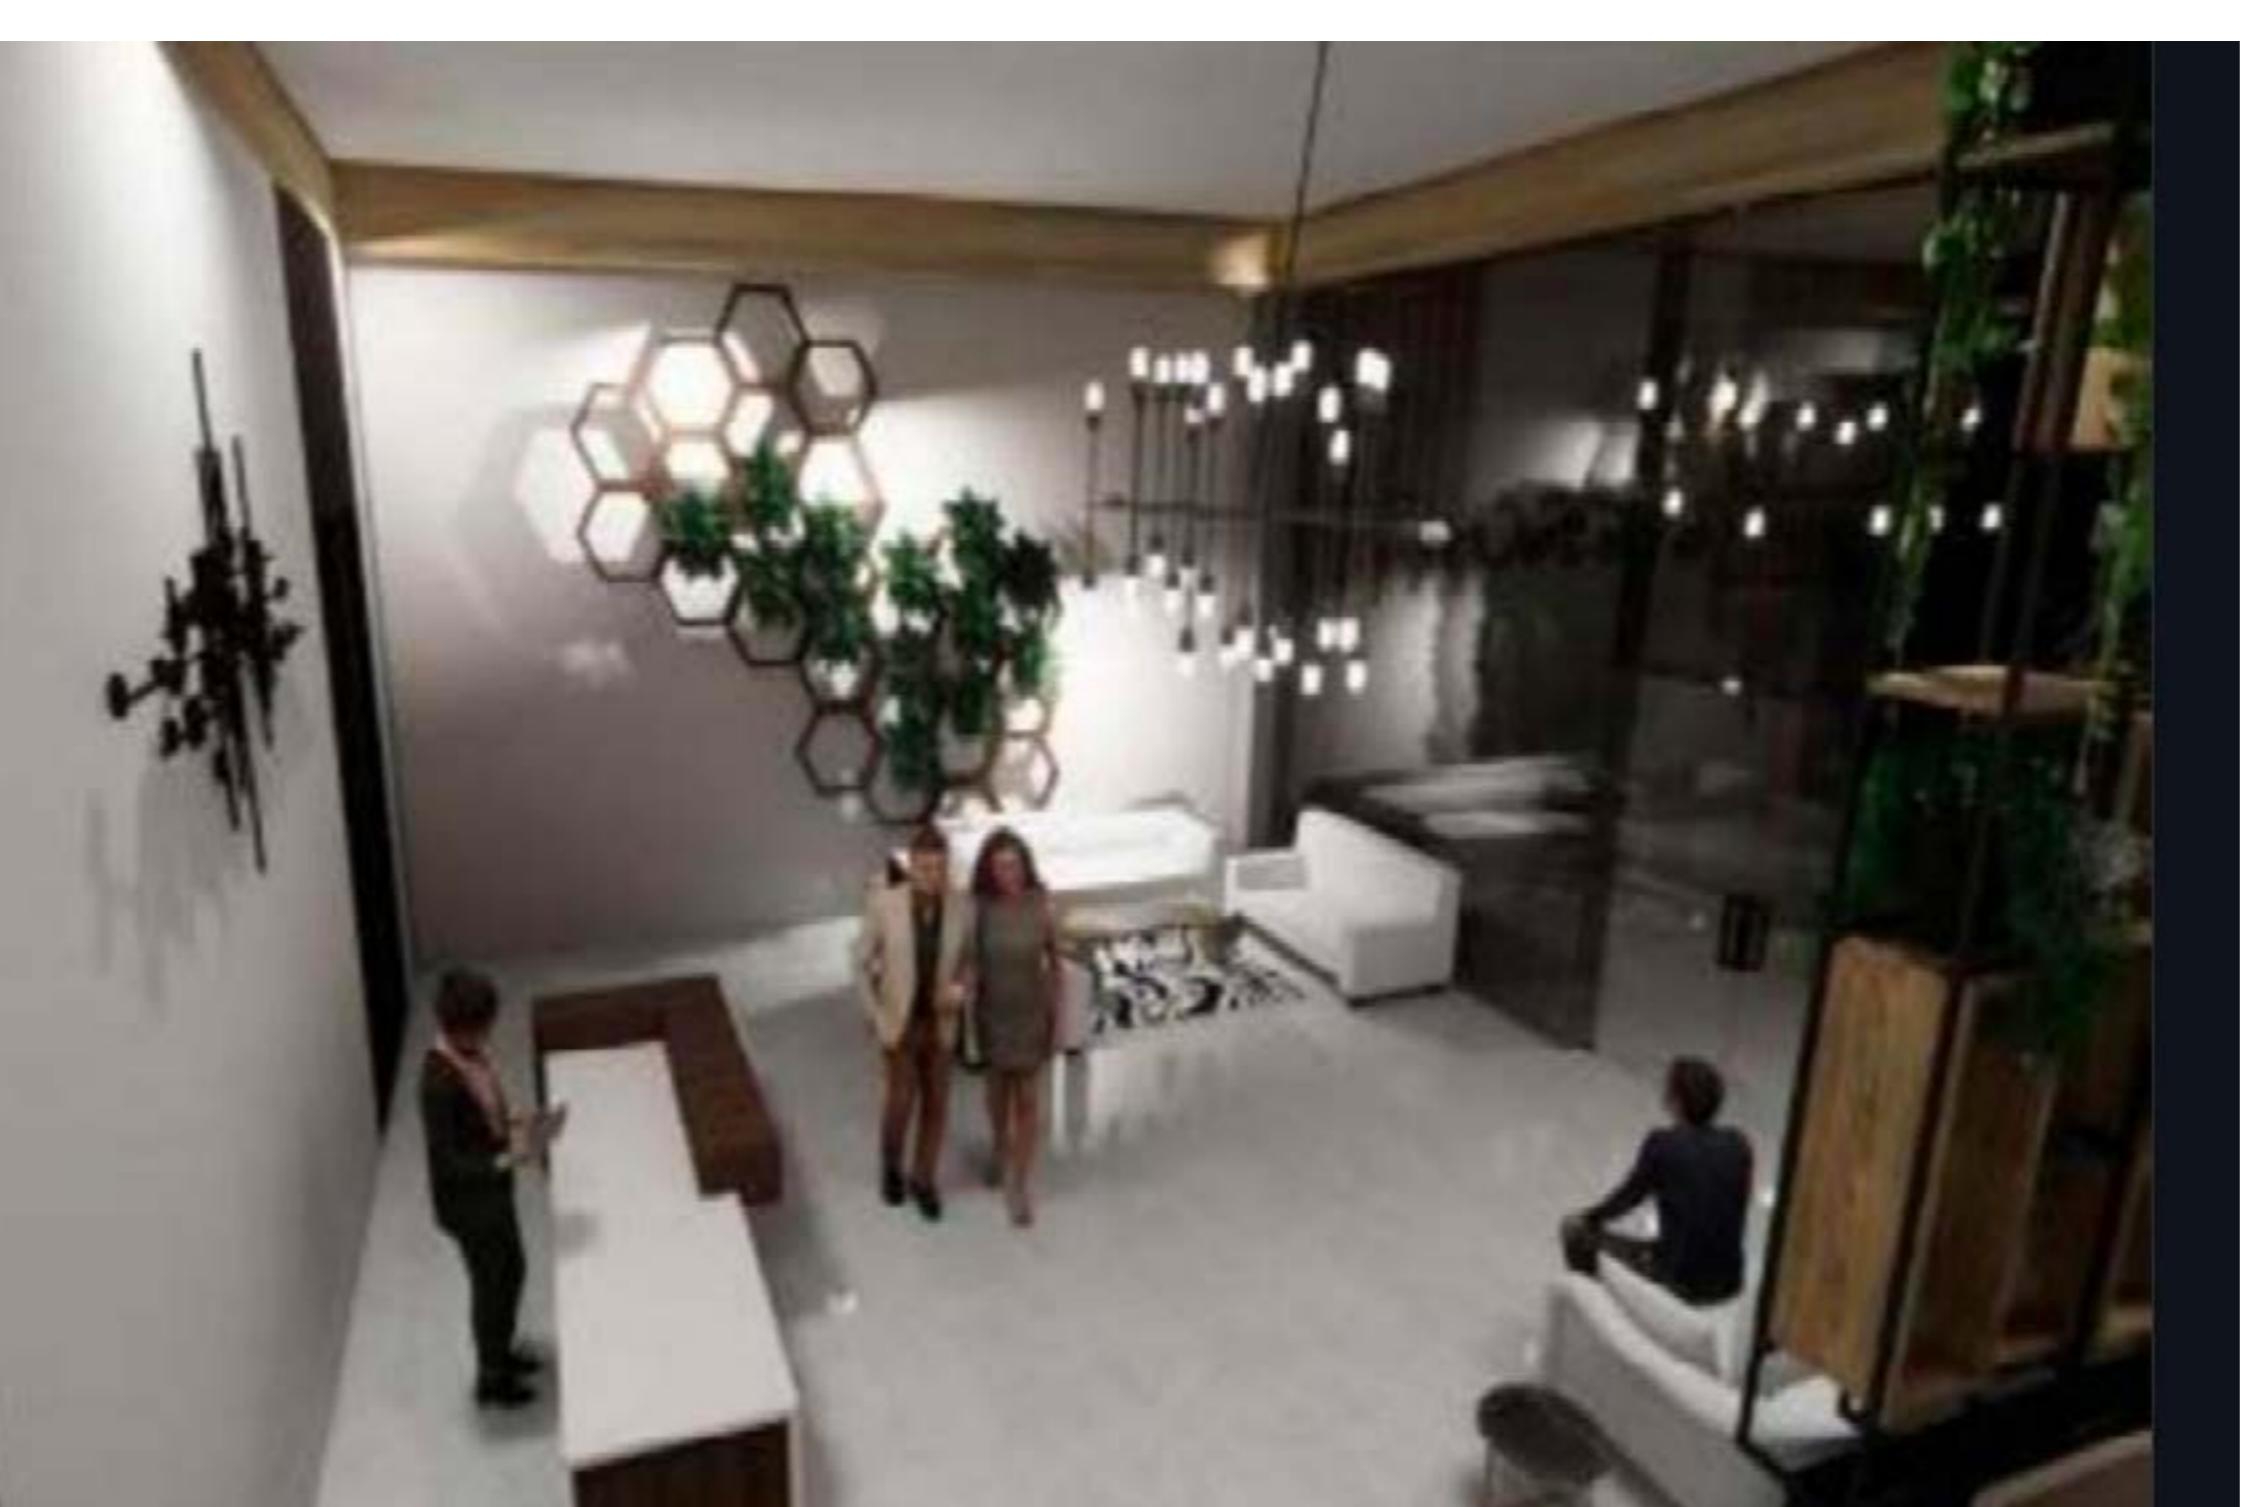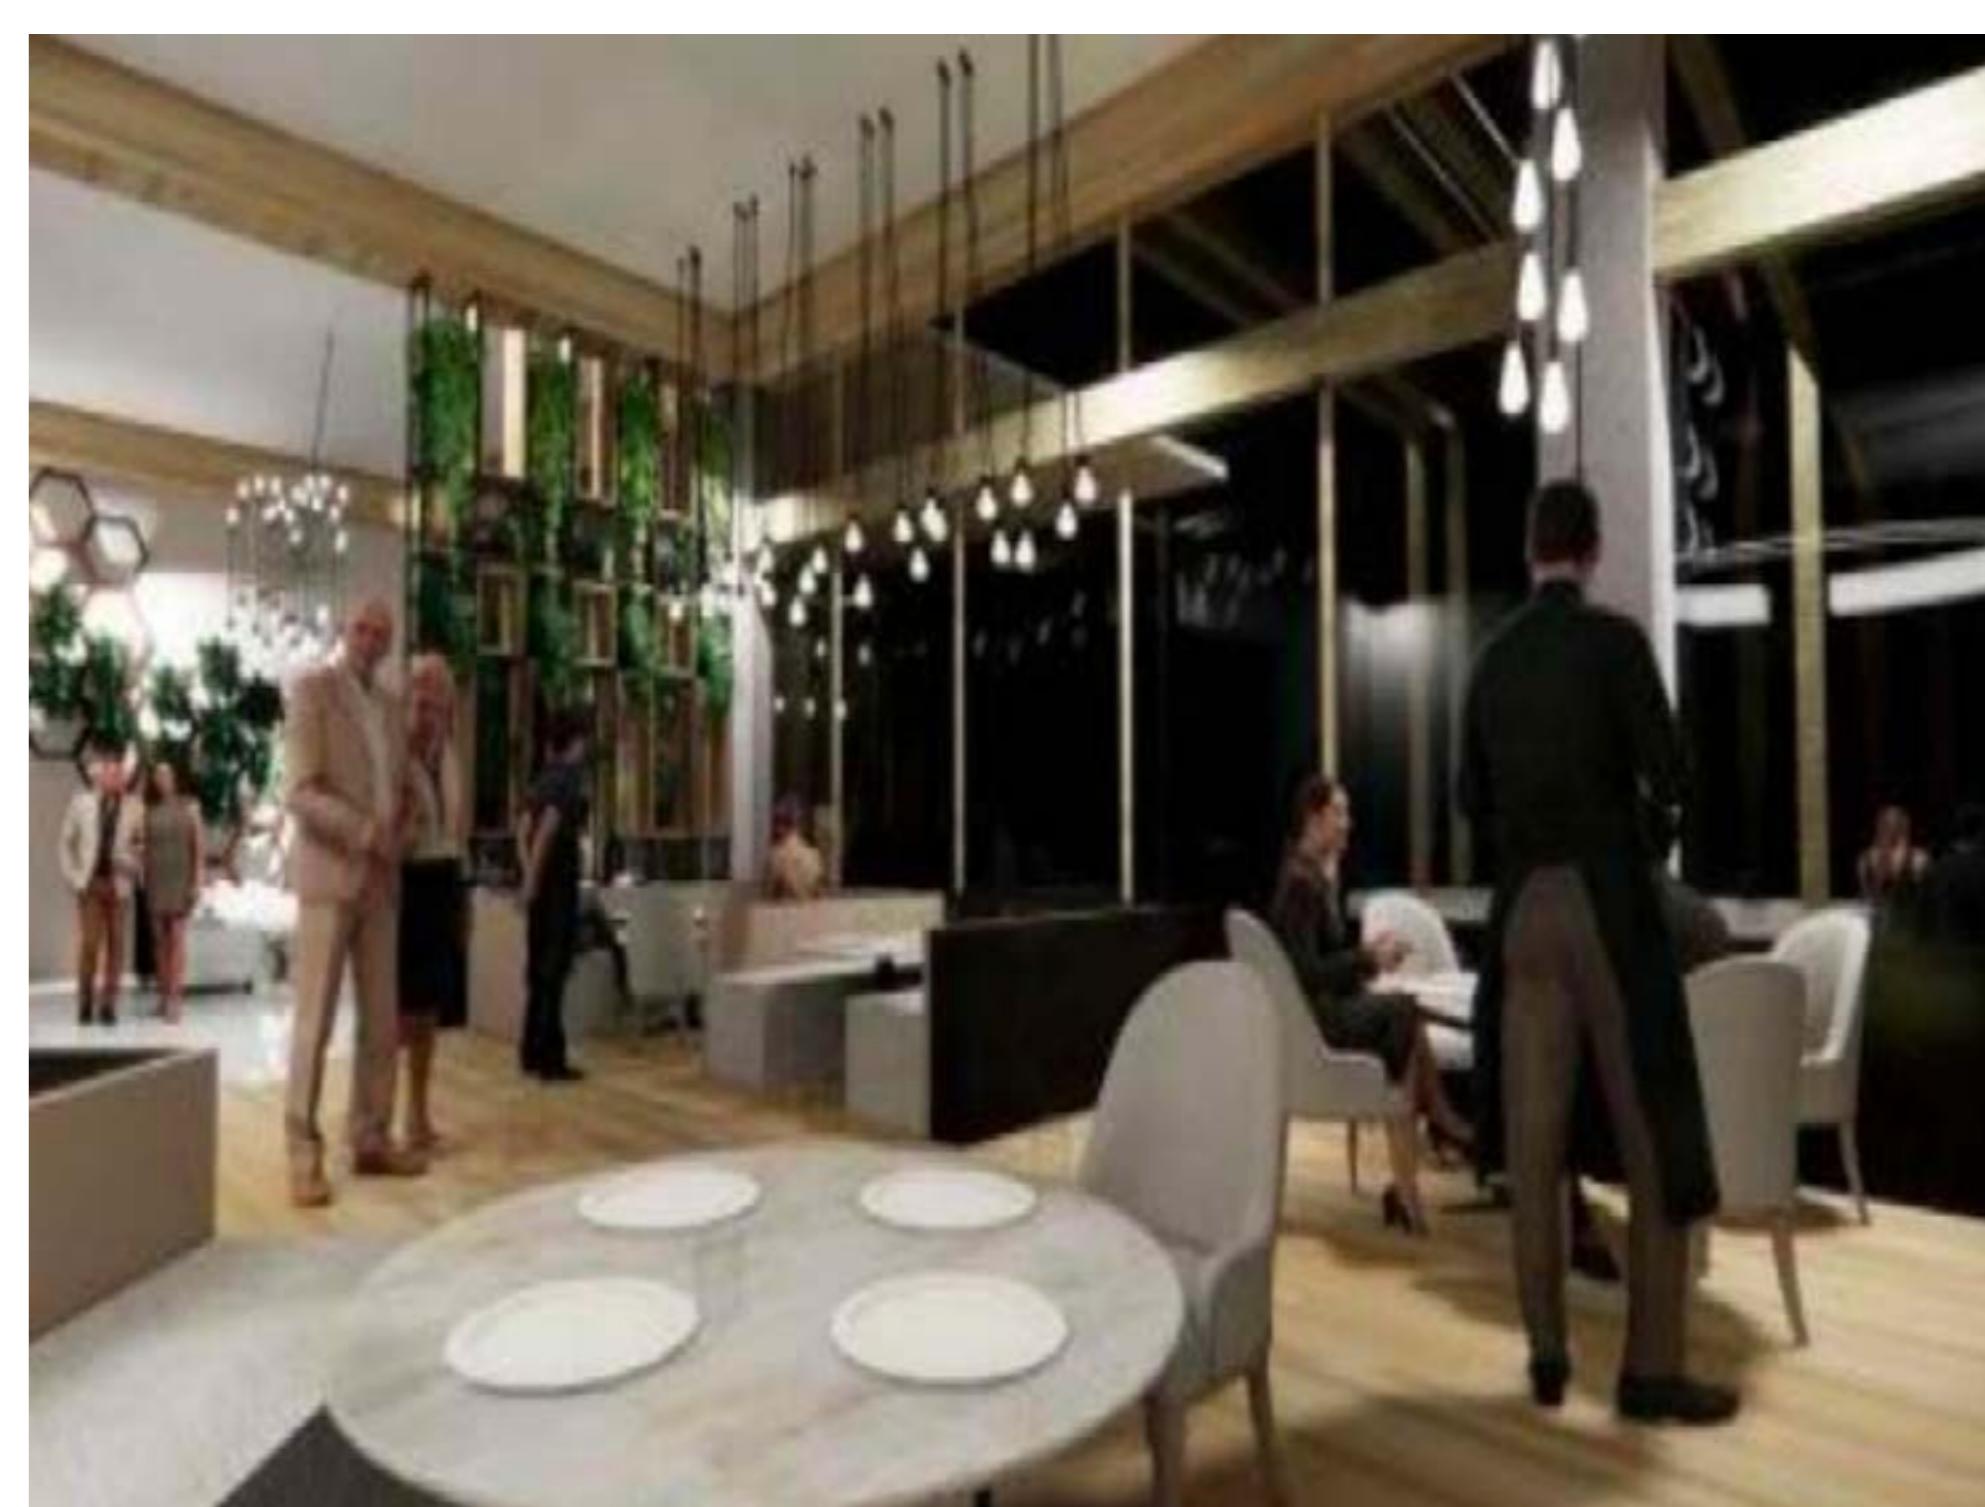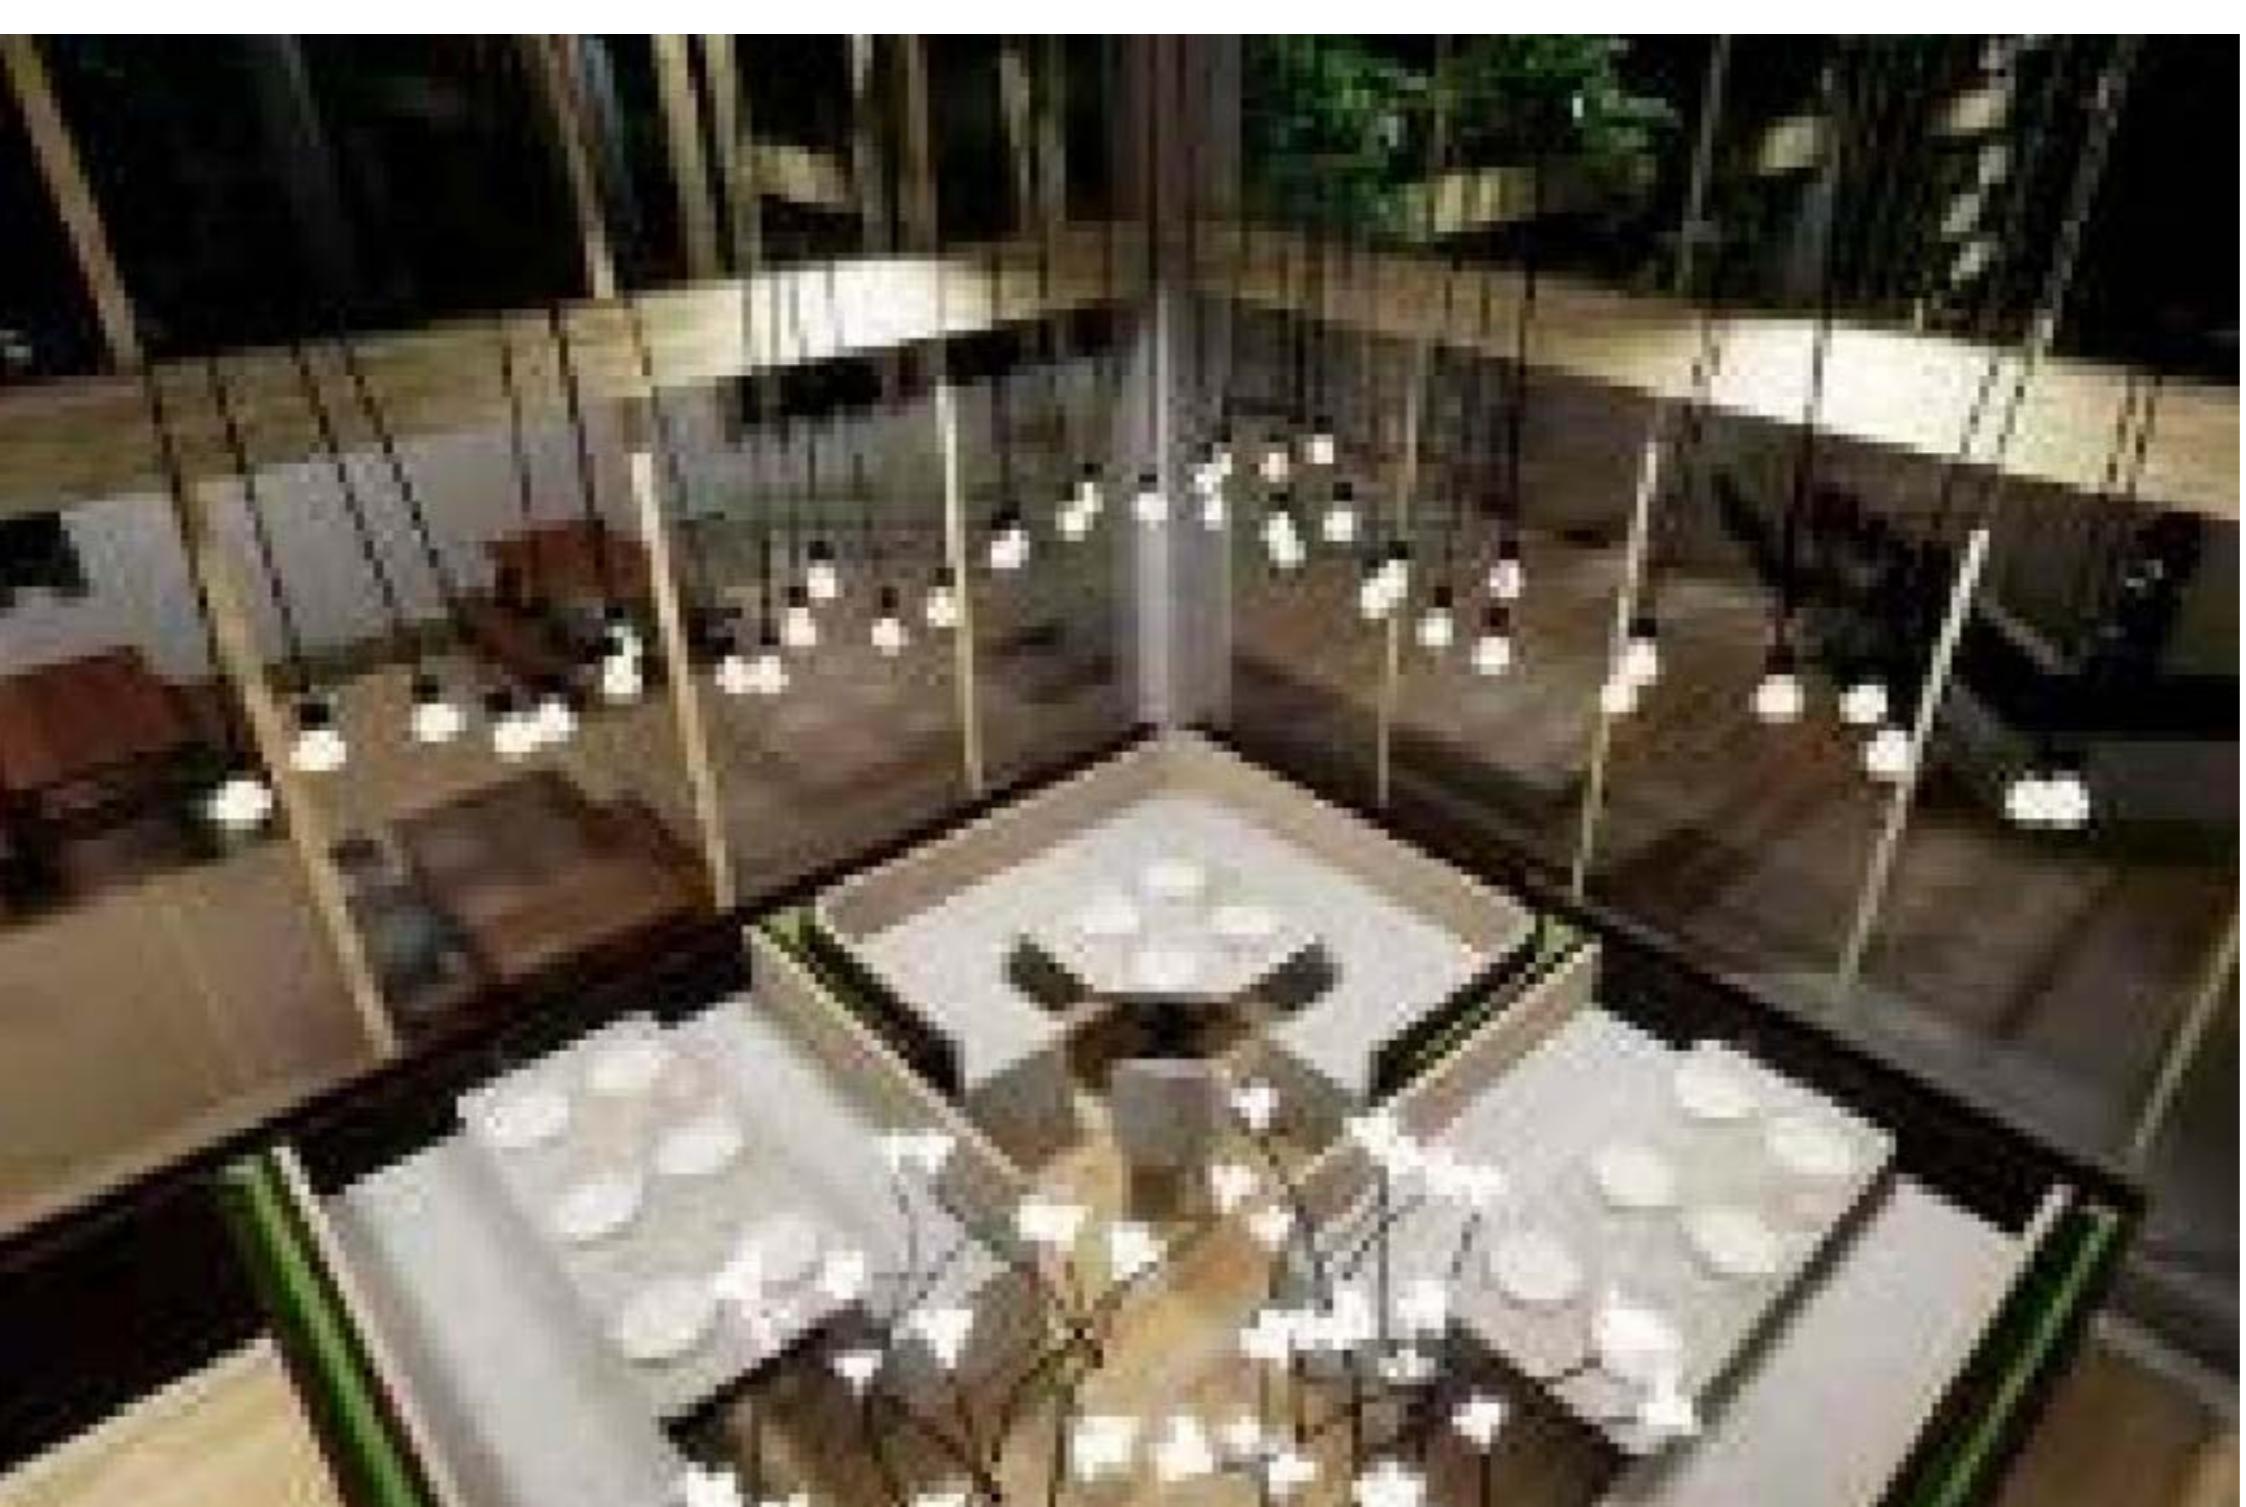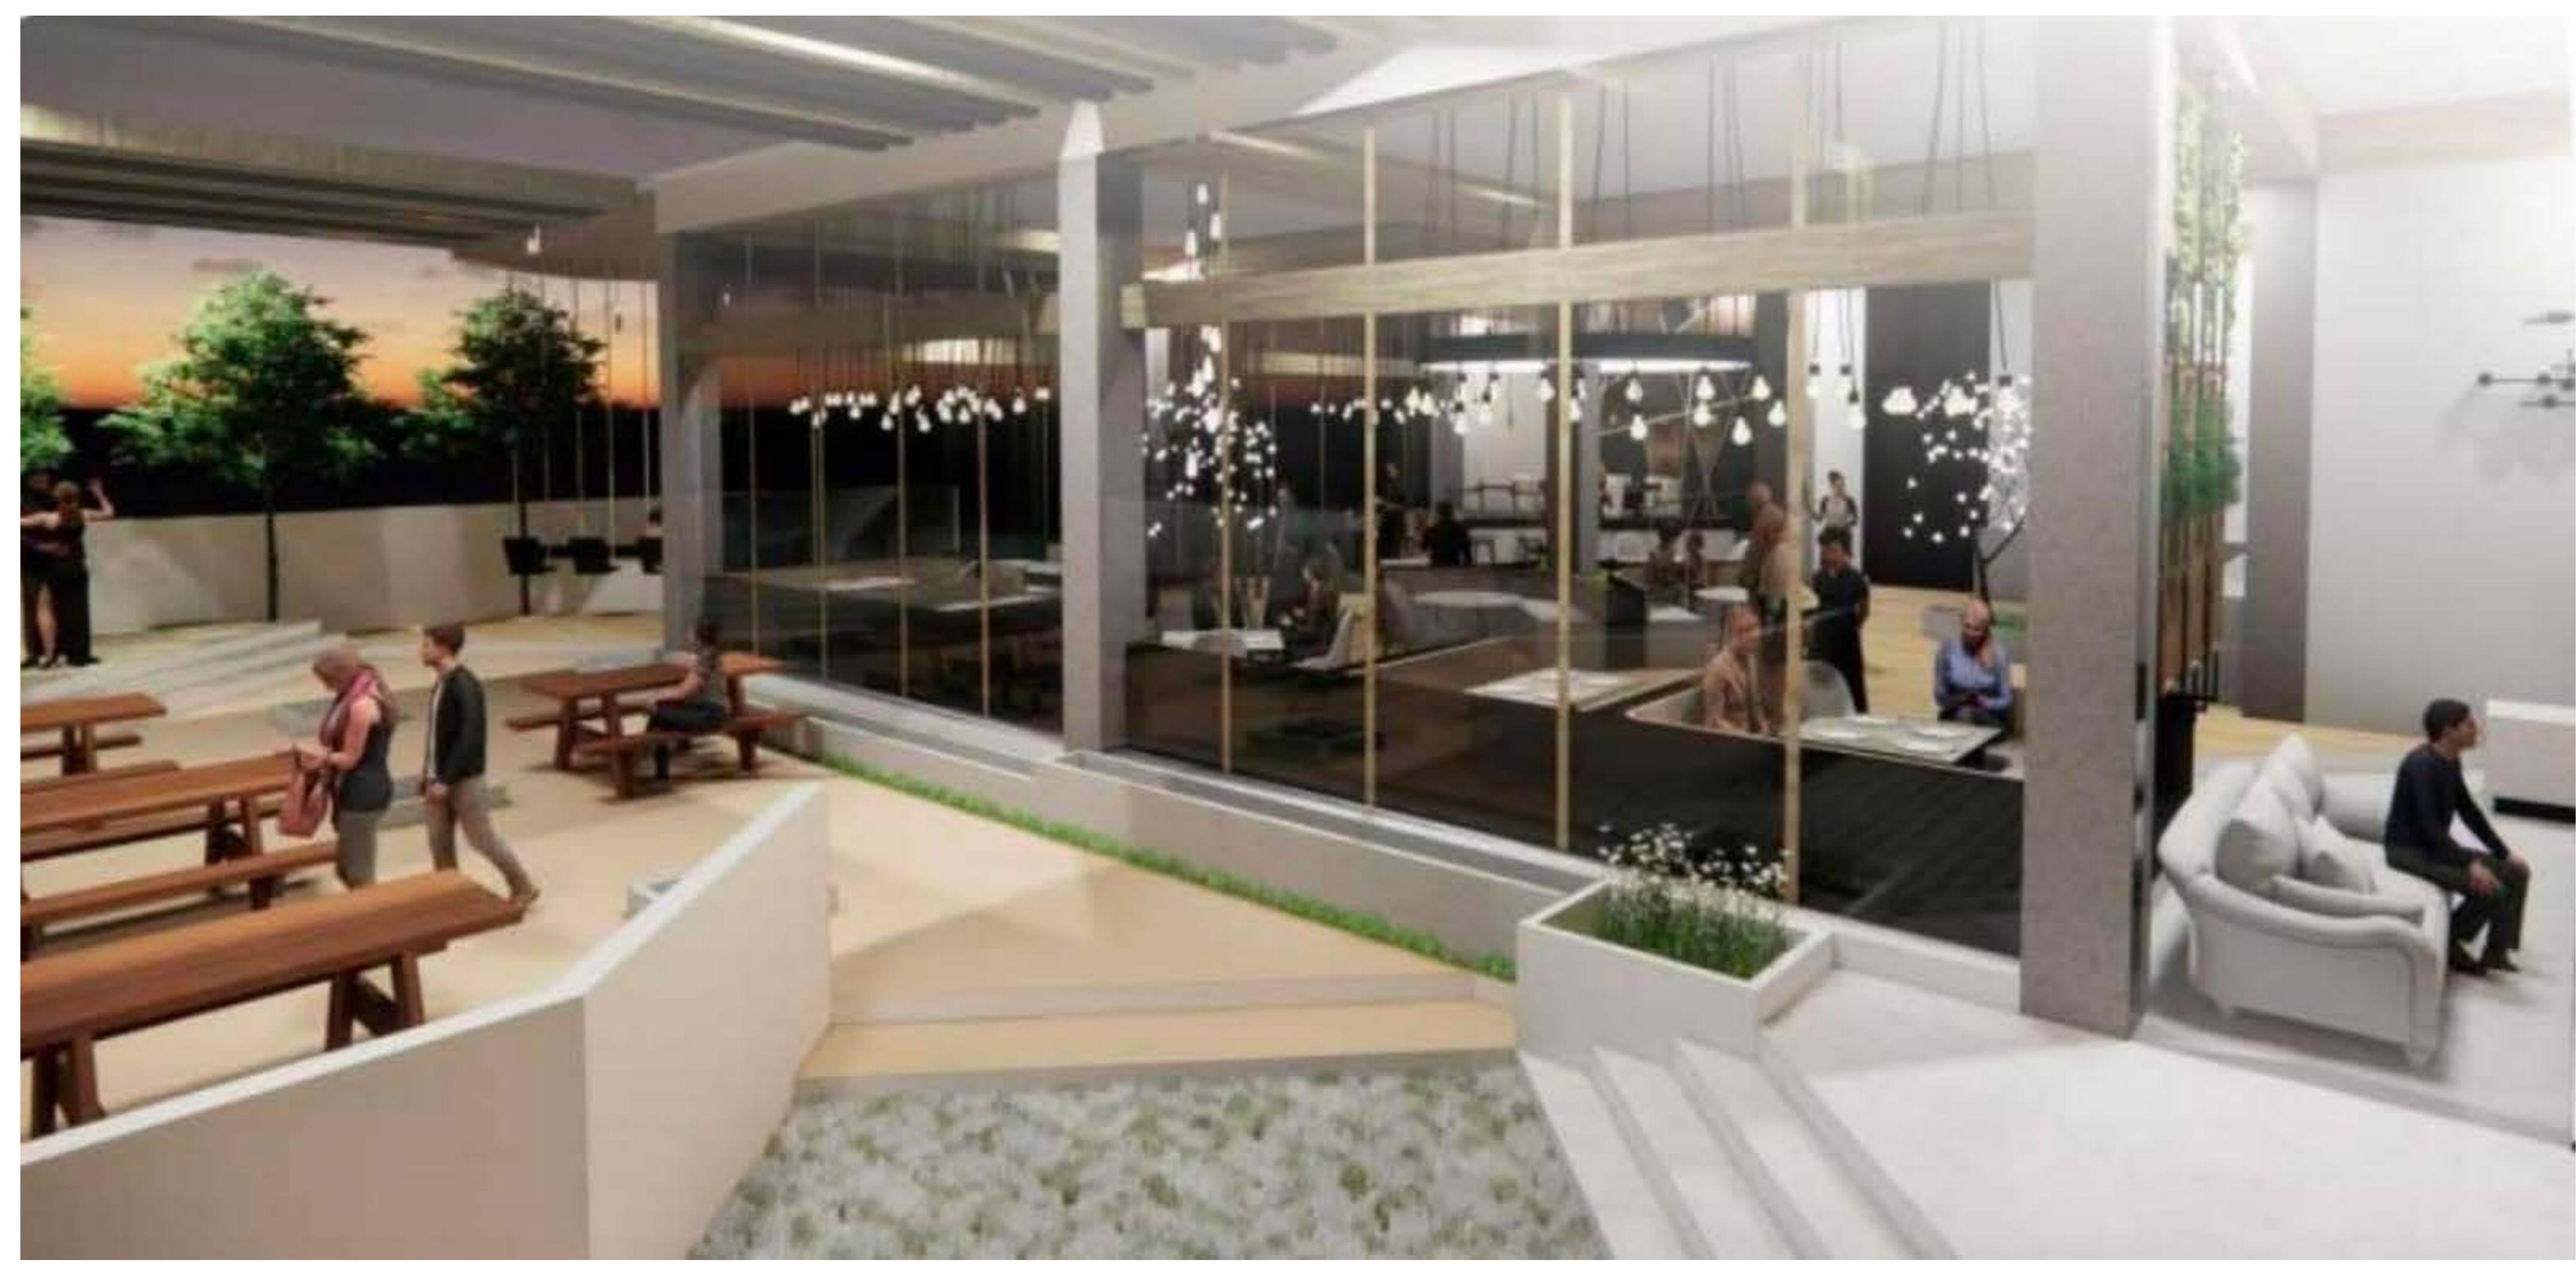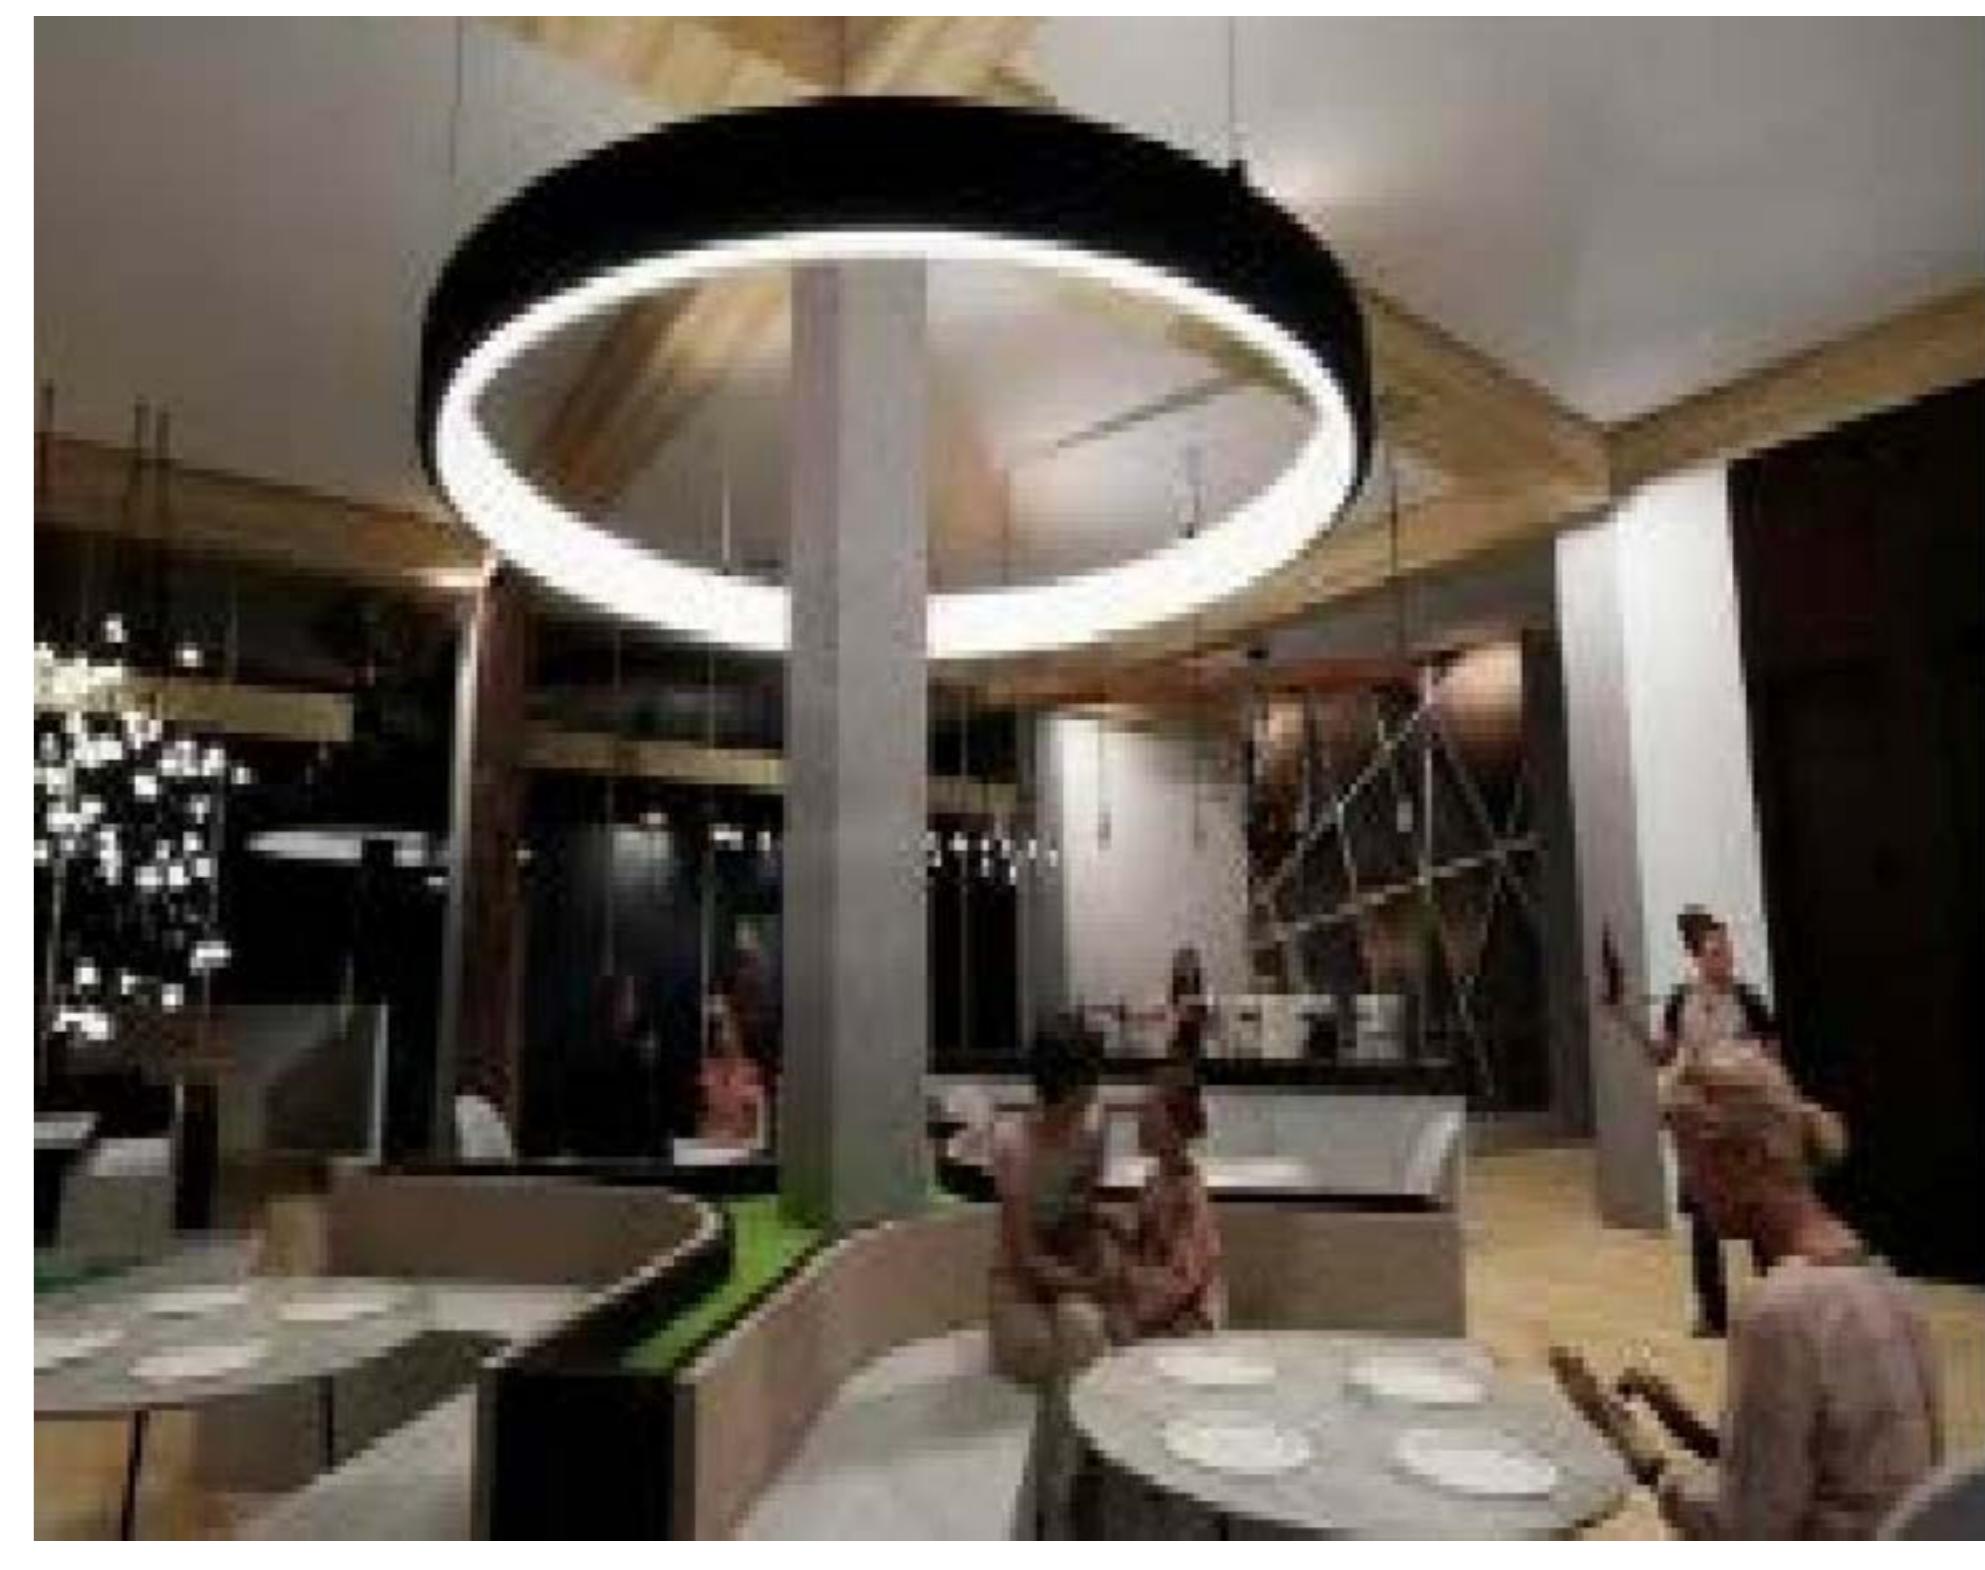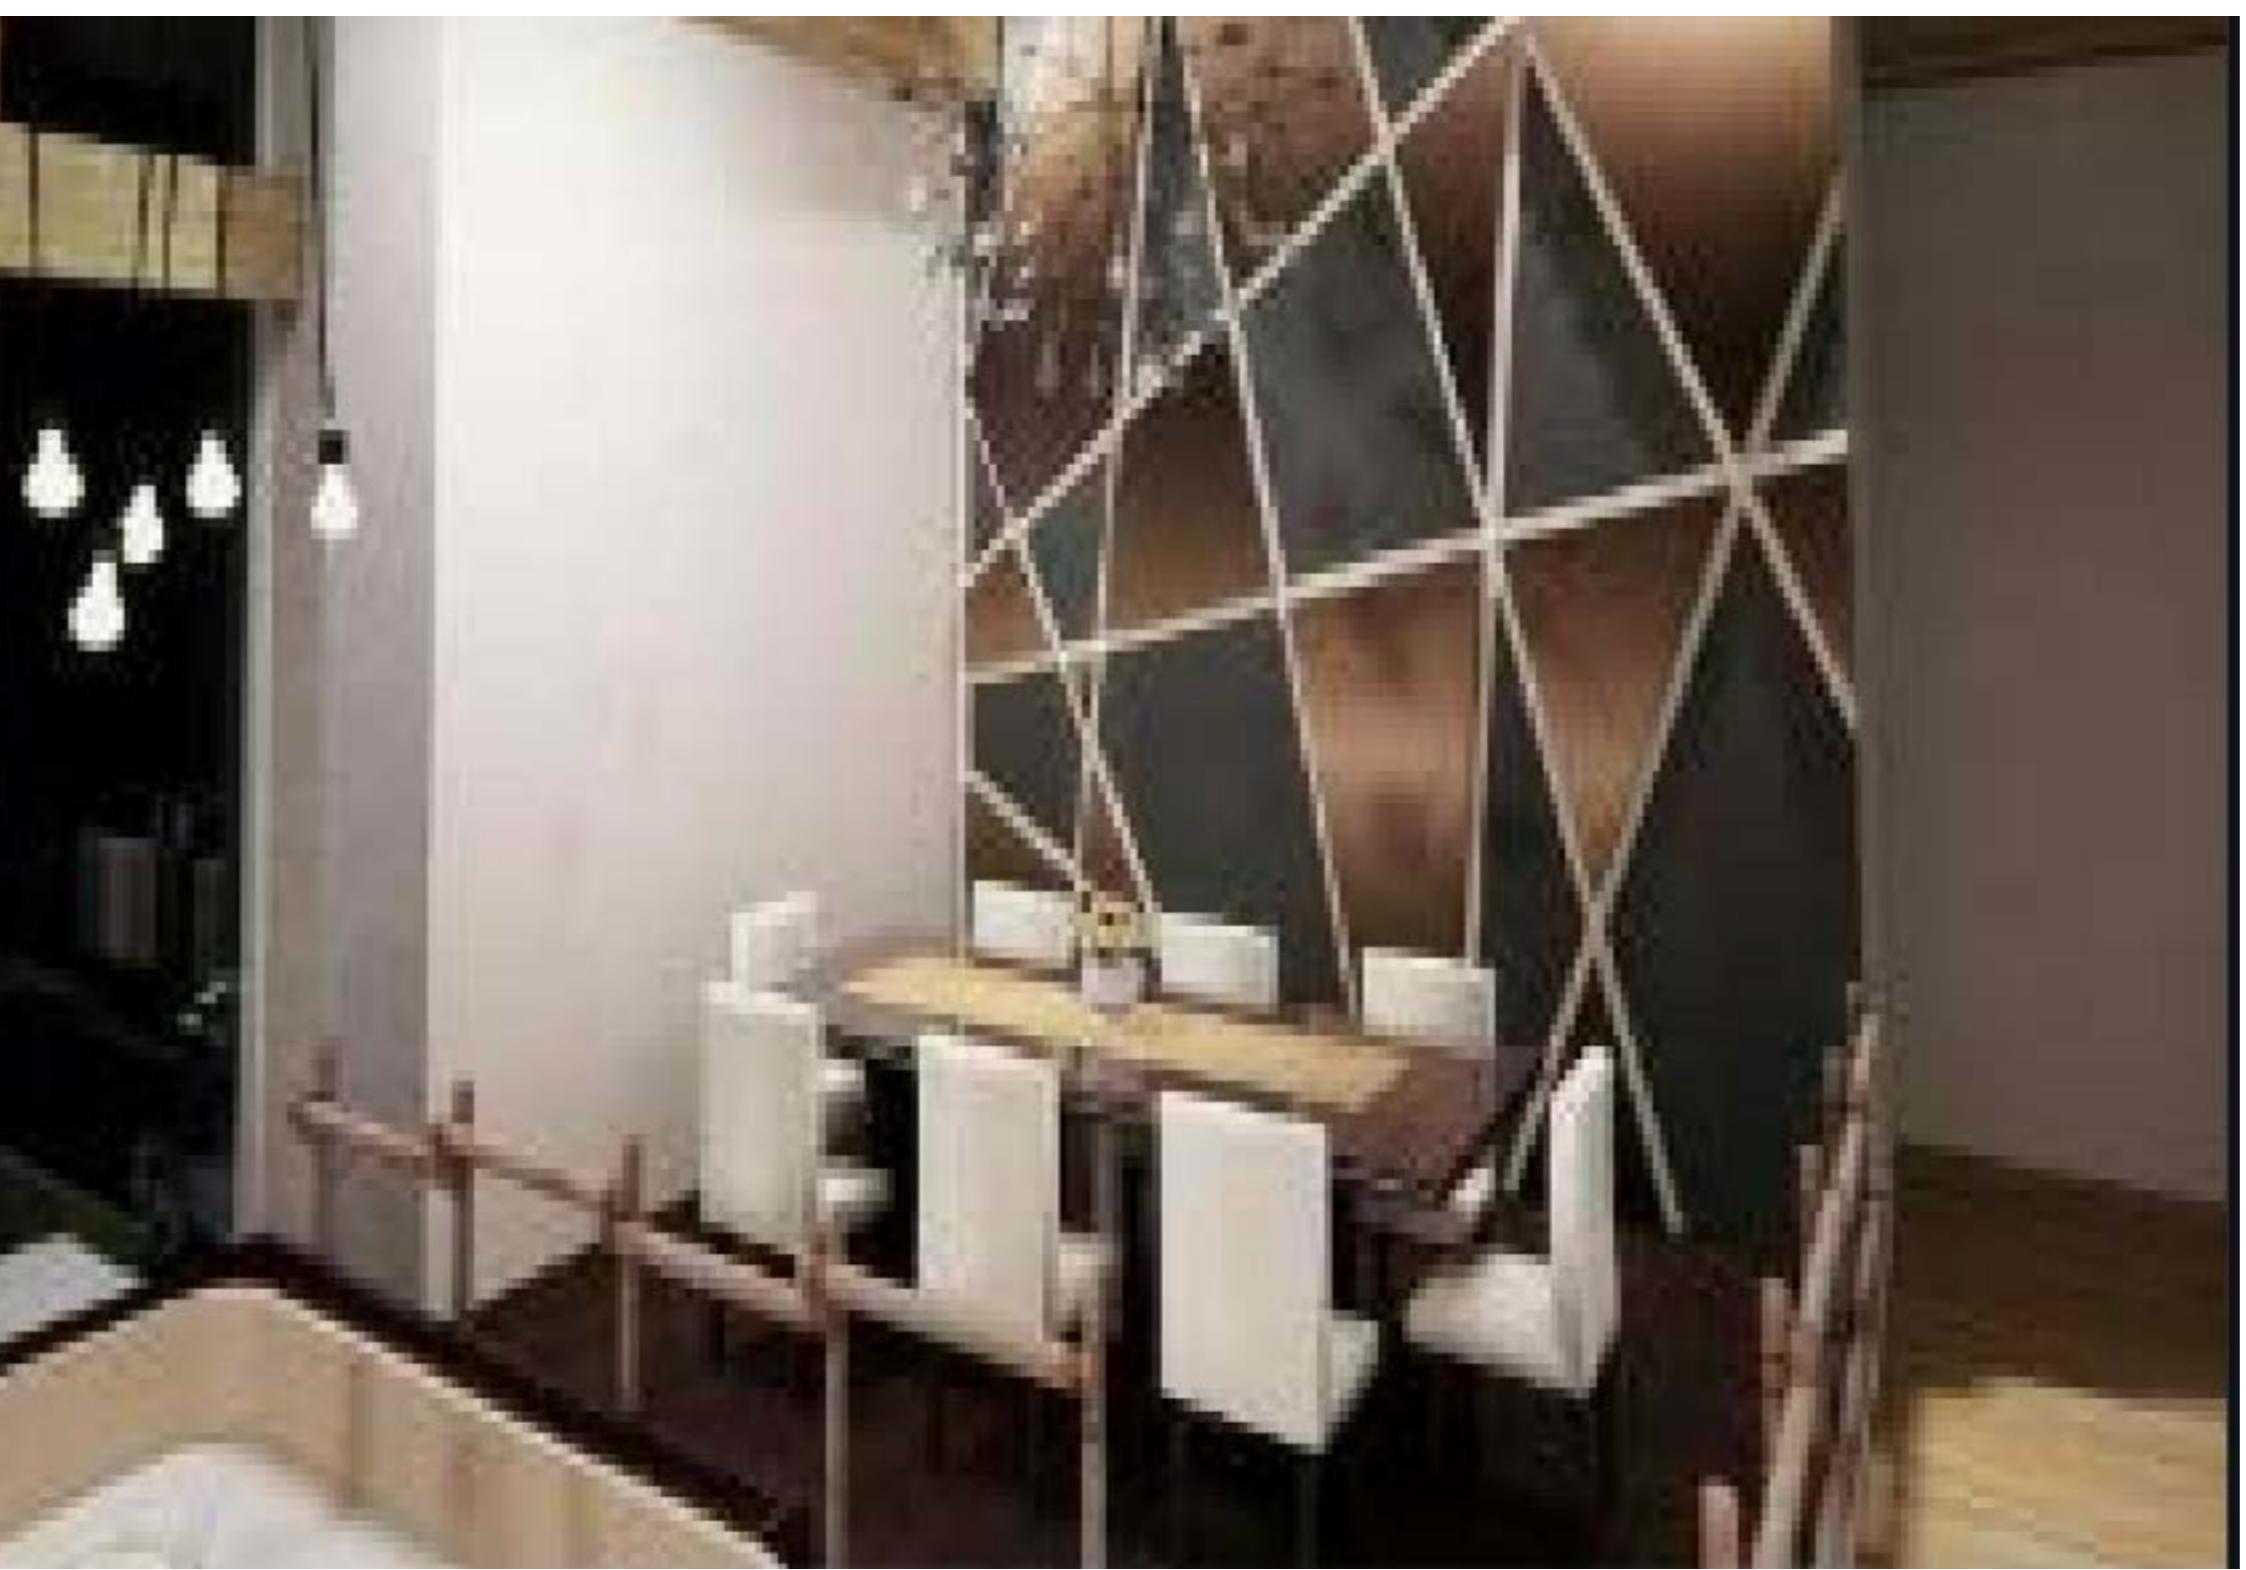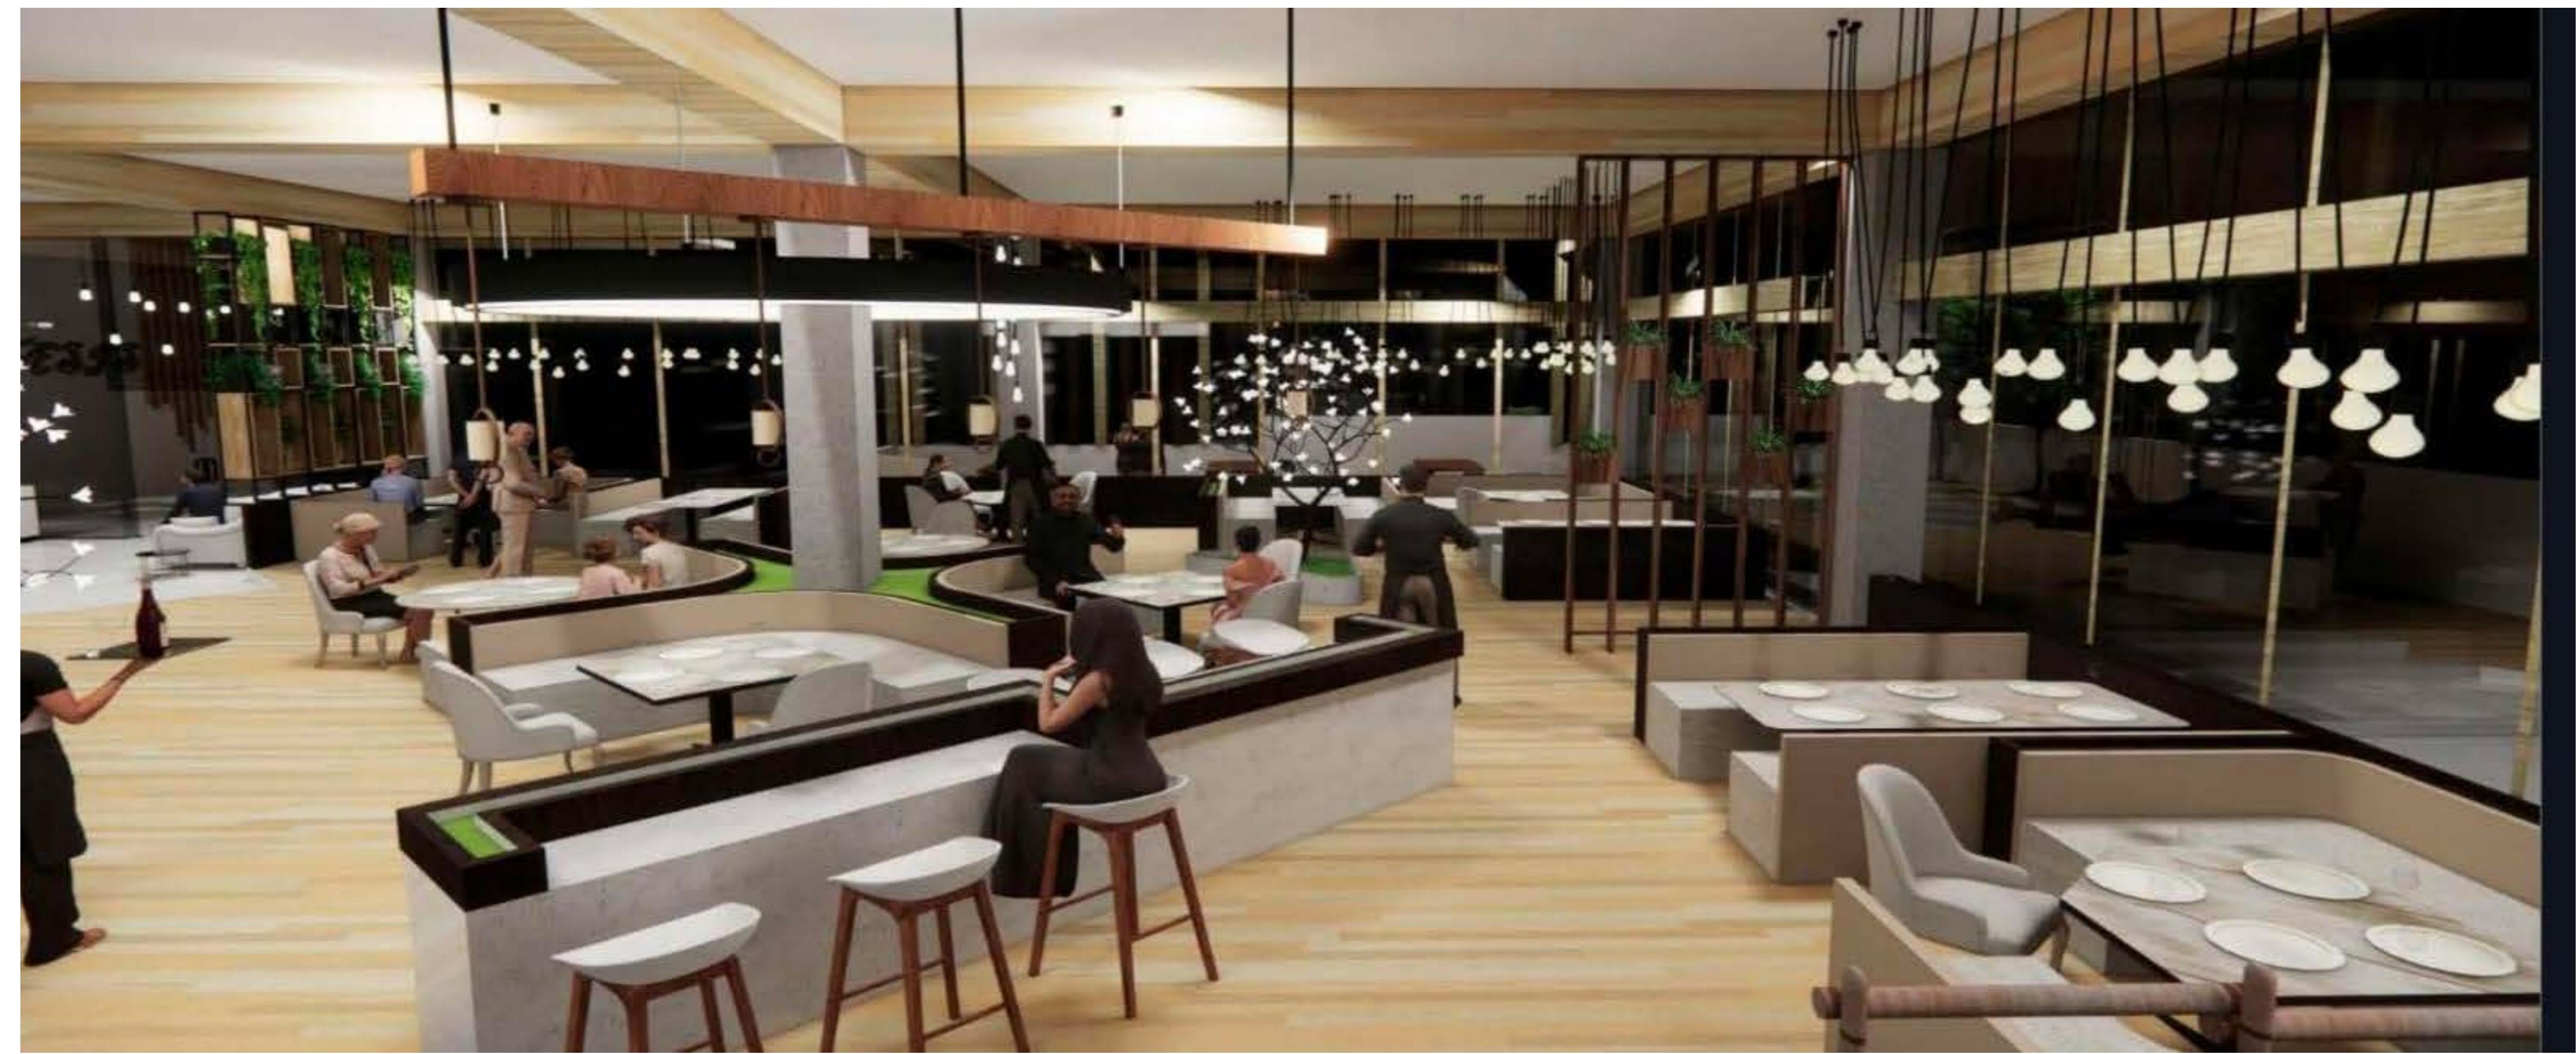







# TV Unit

## Semester 5

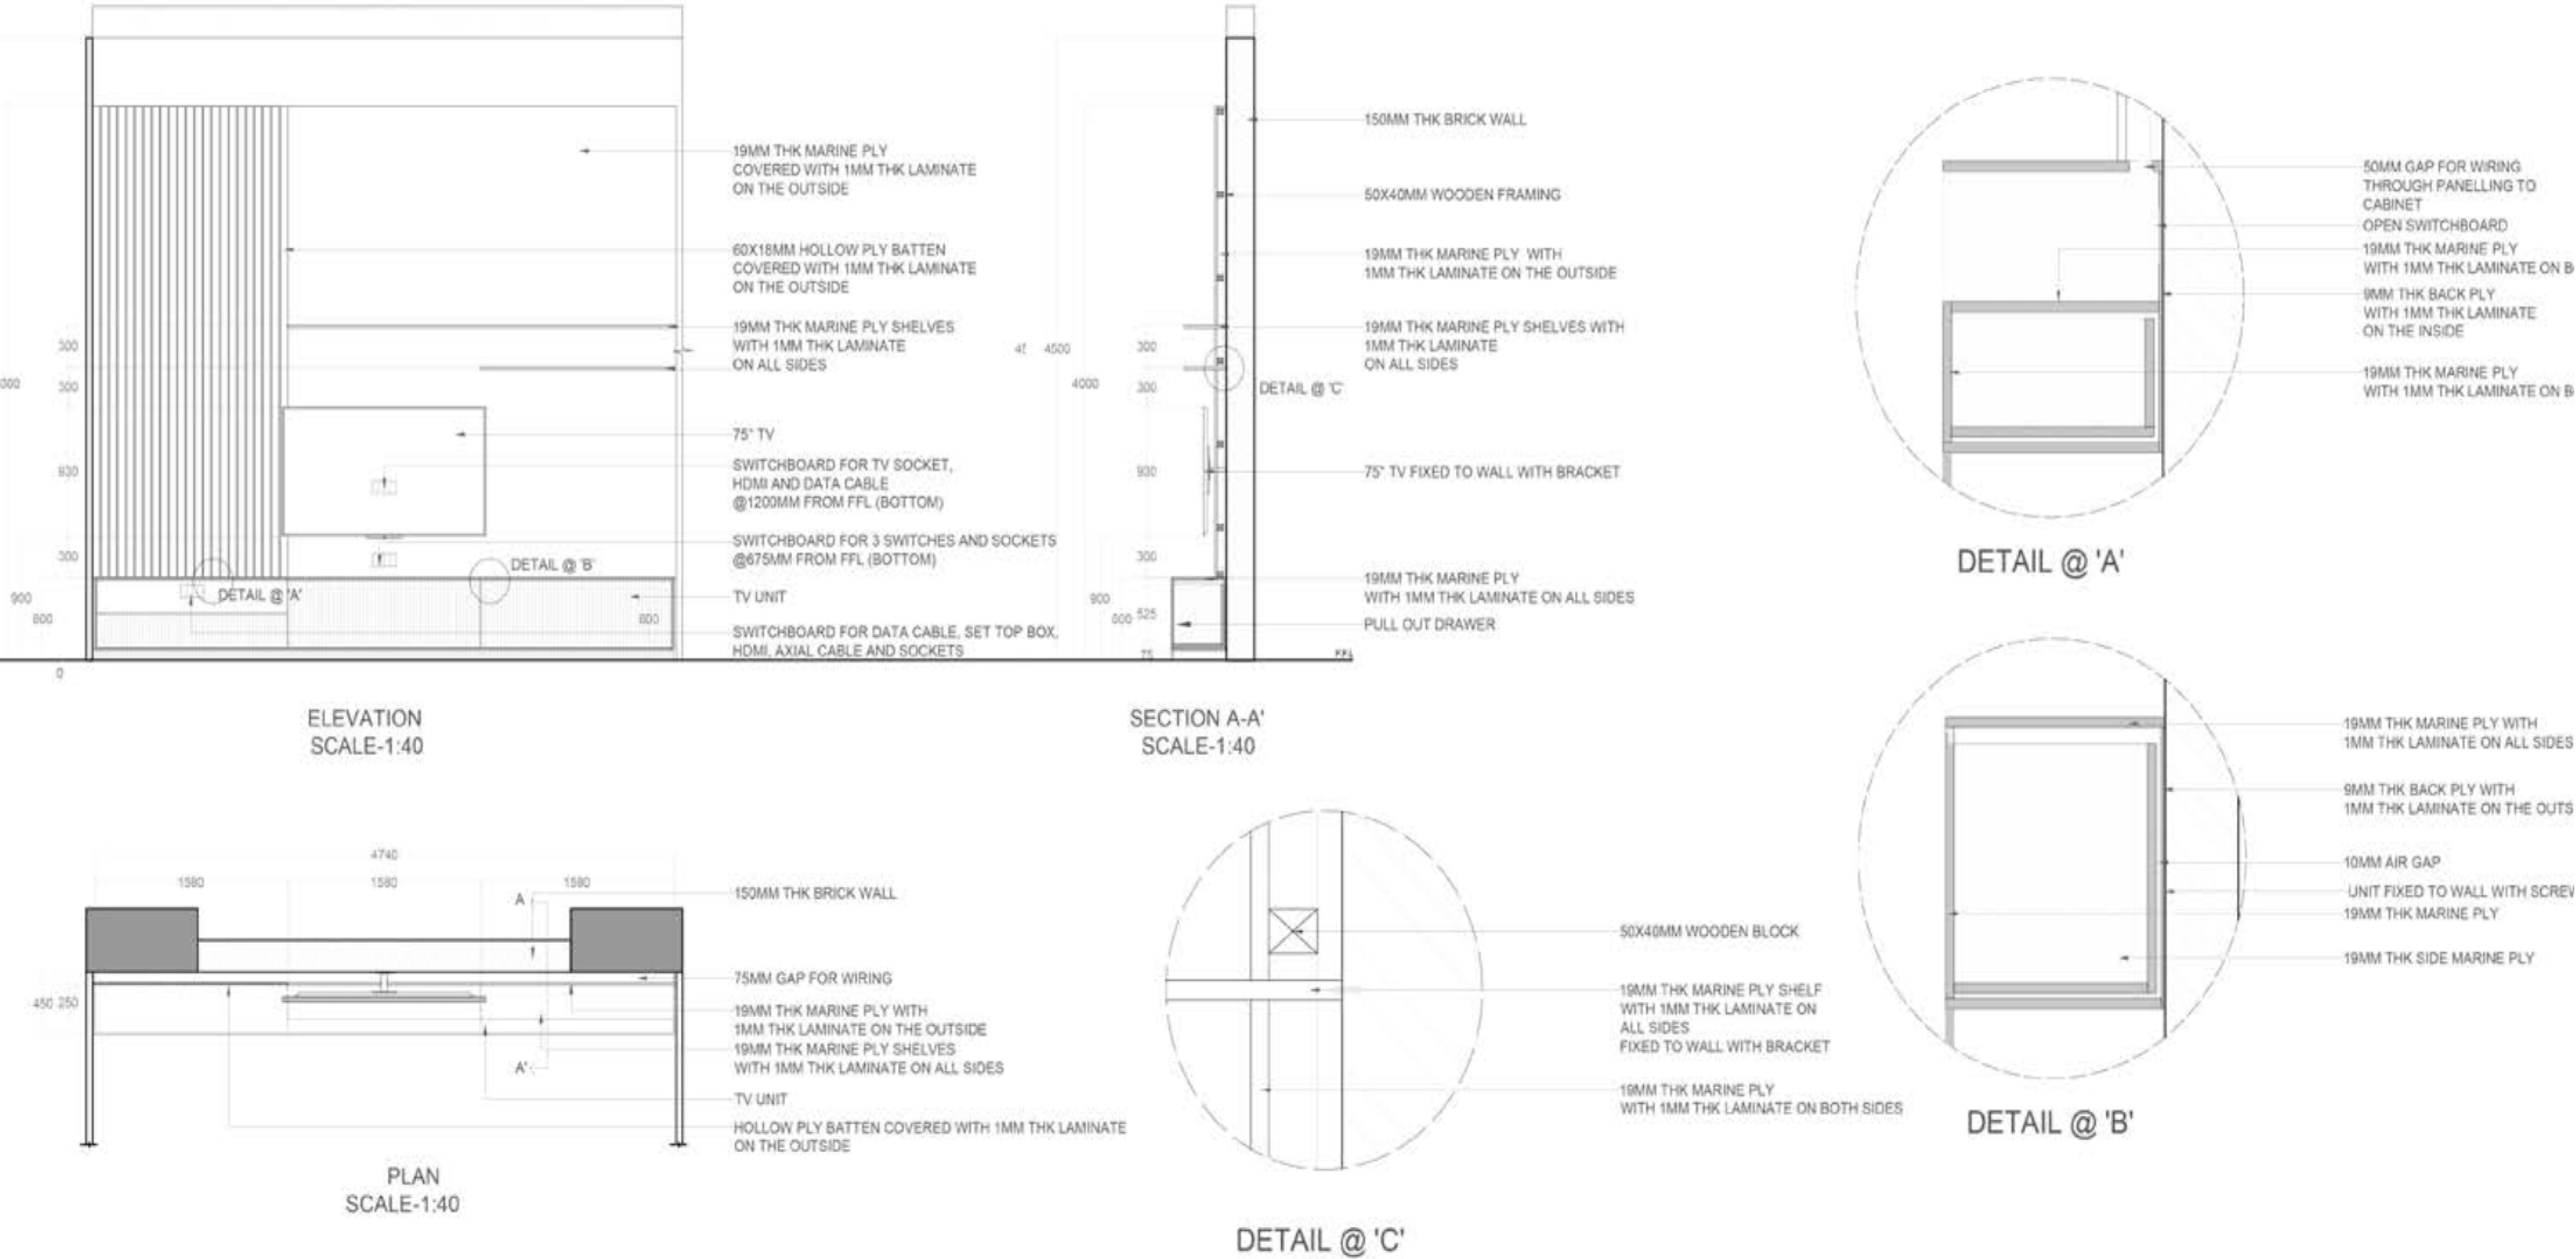


# Table and Chair

## Semester 5

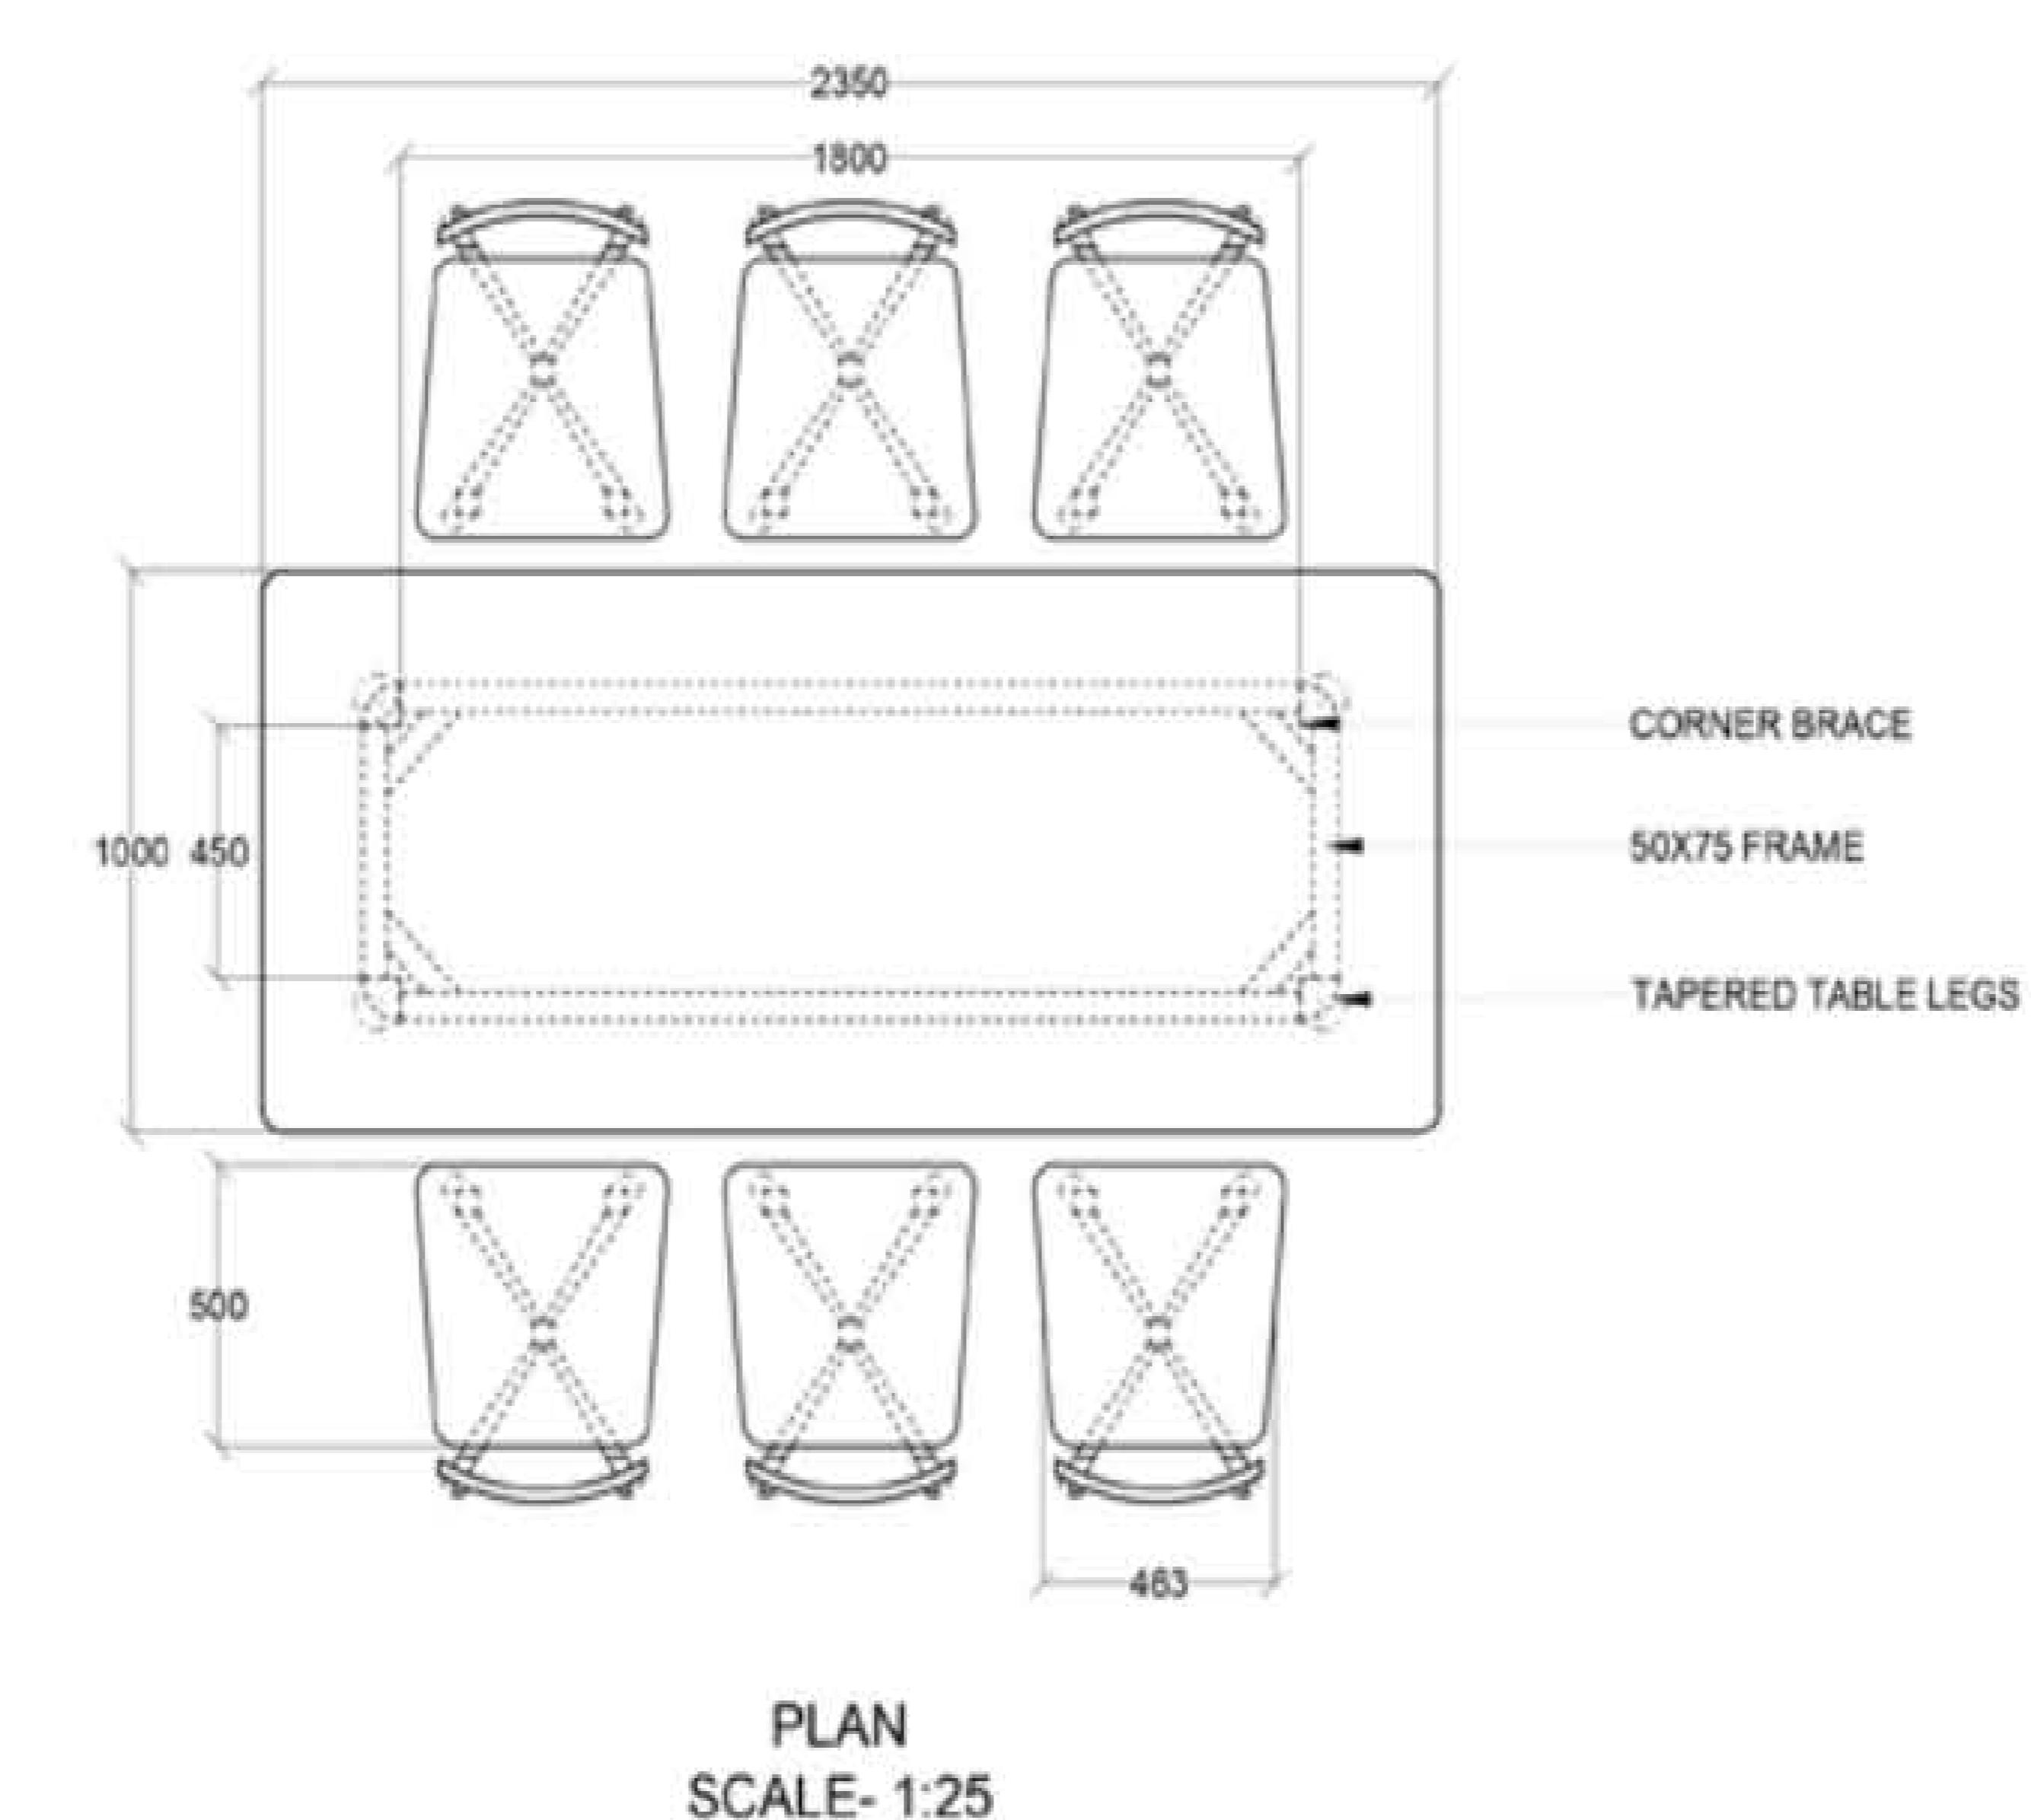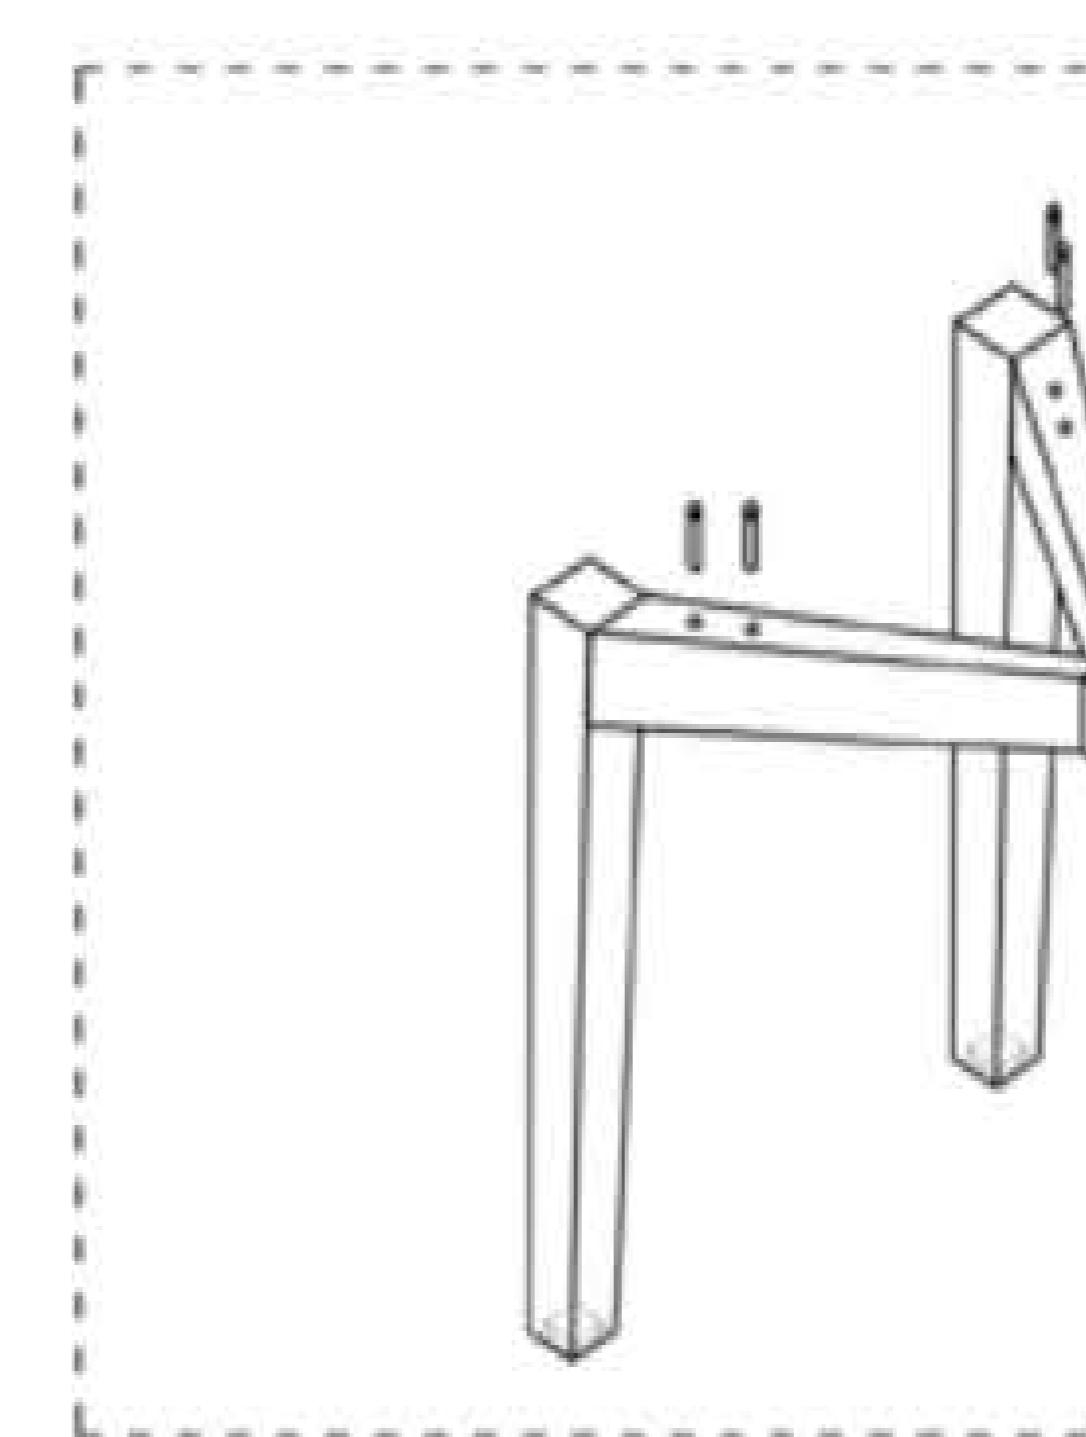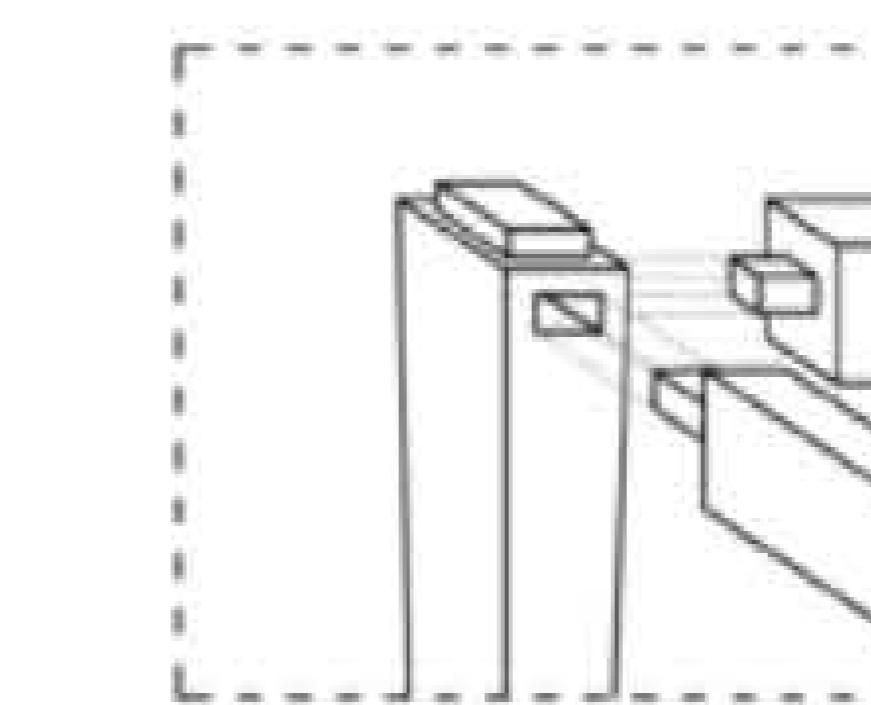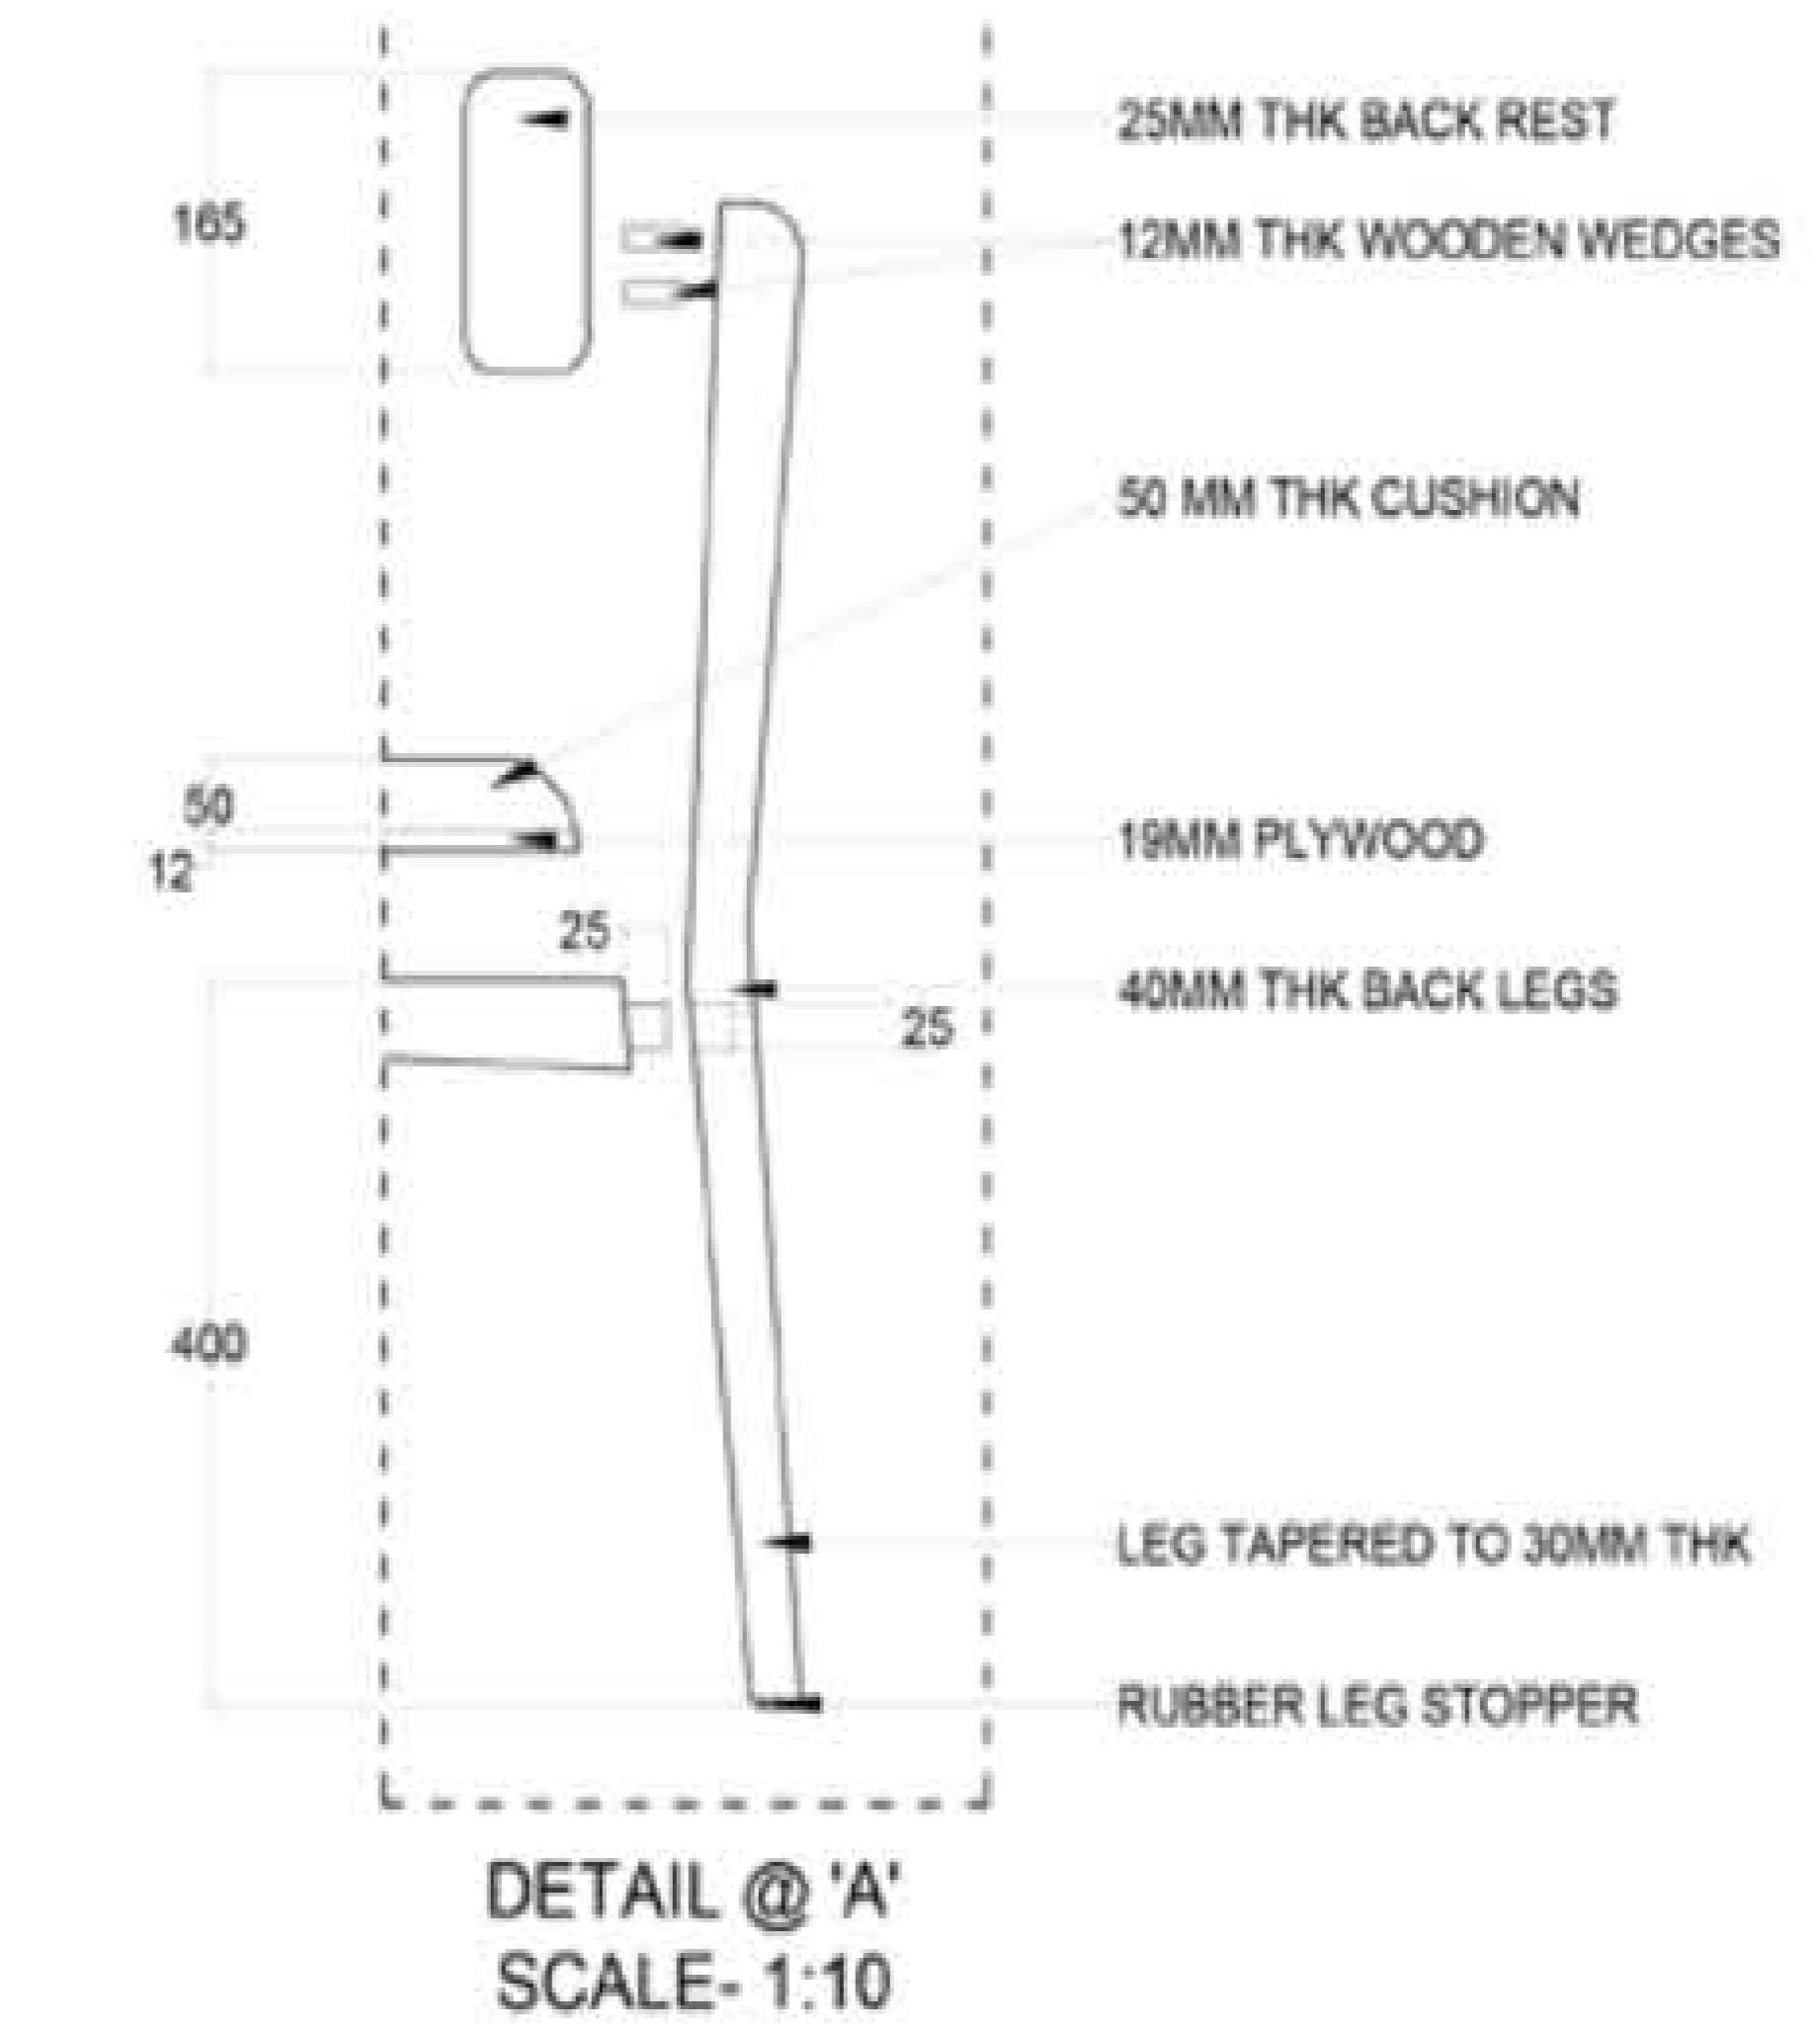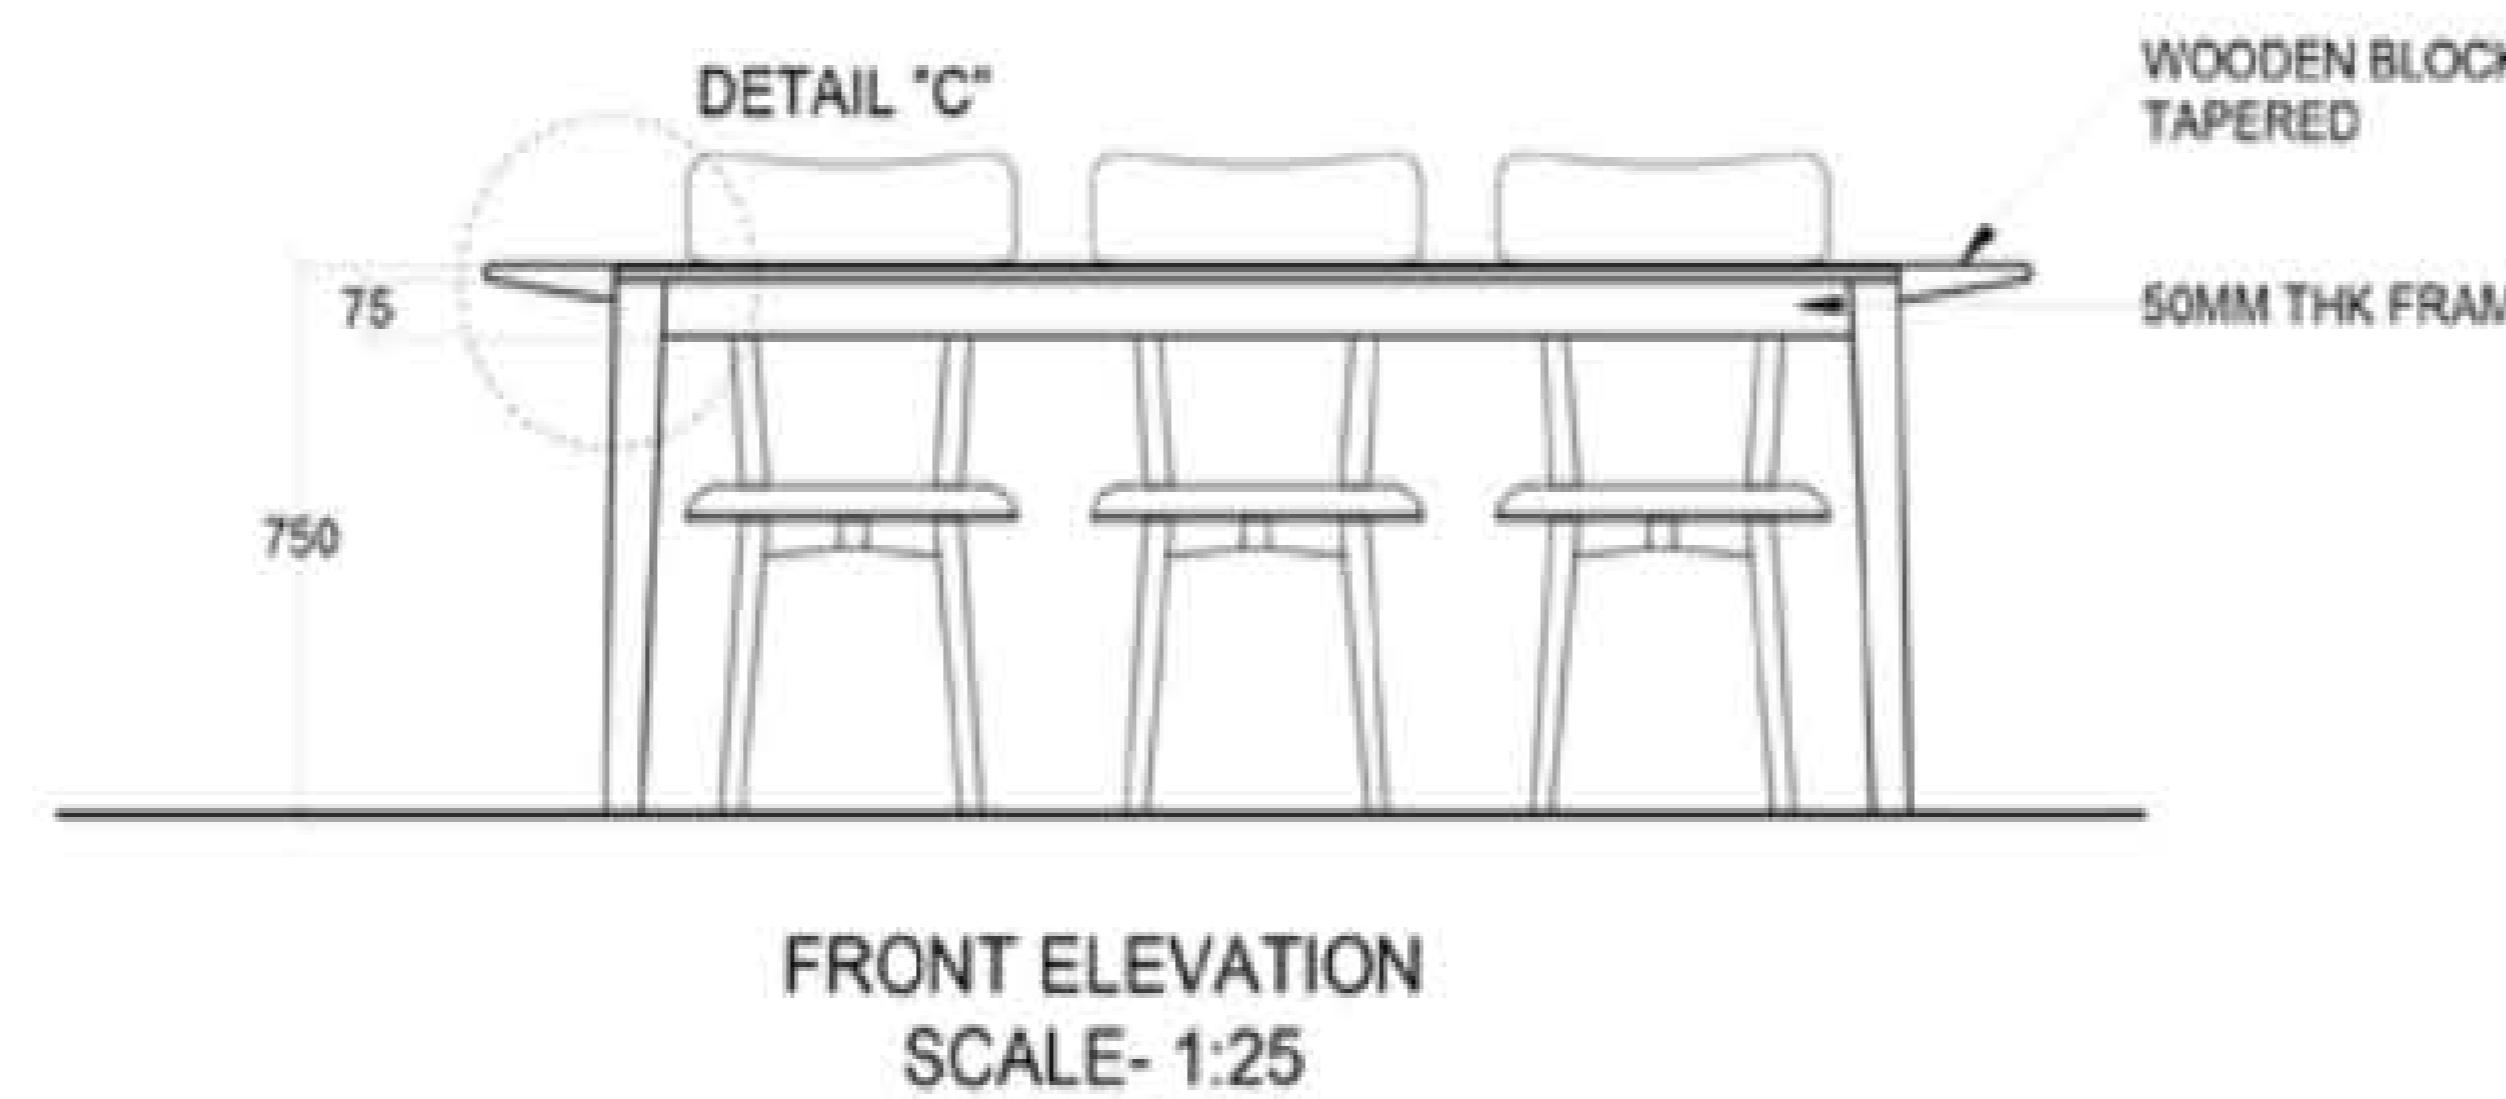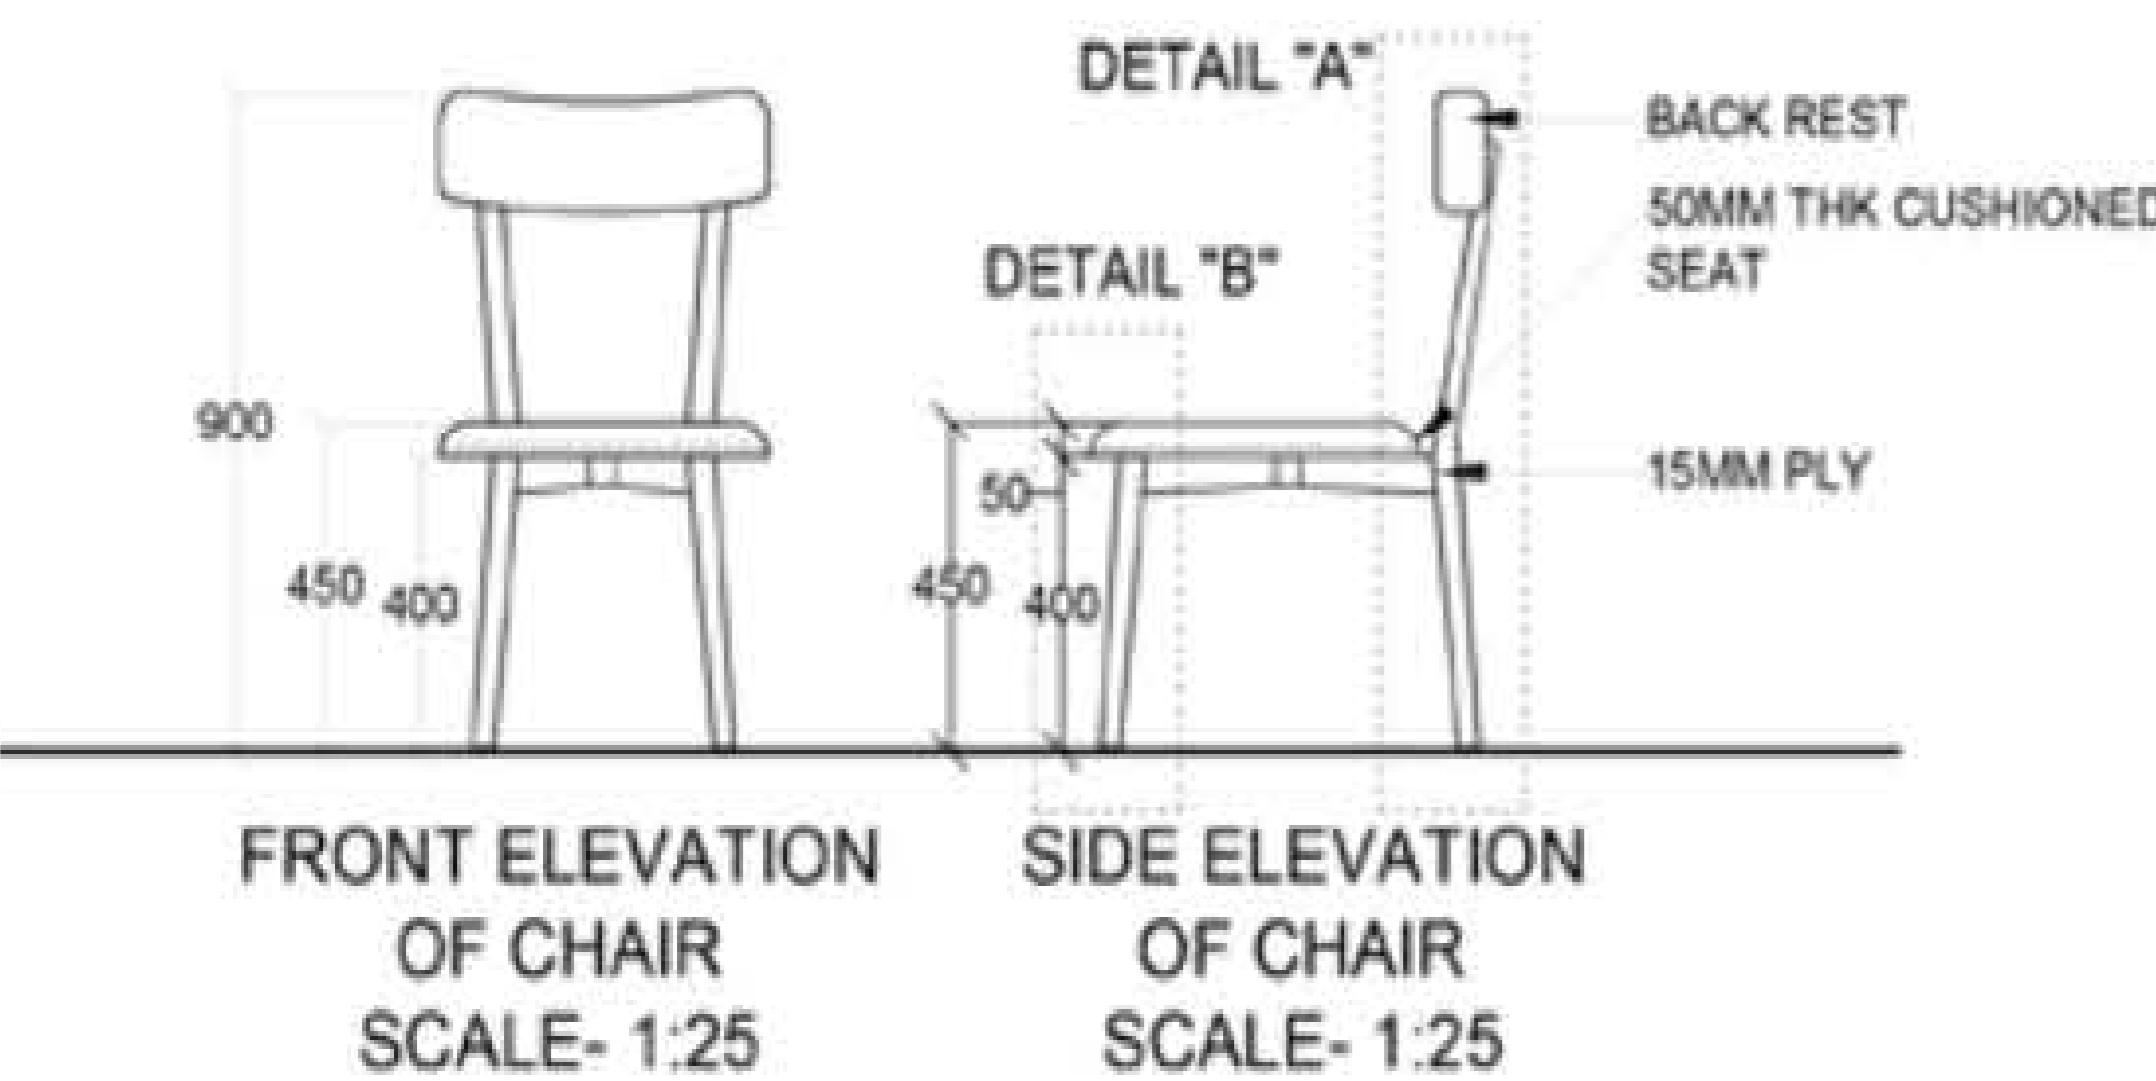

# Wardrobe

## Semester 5

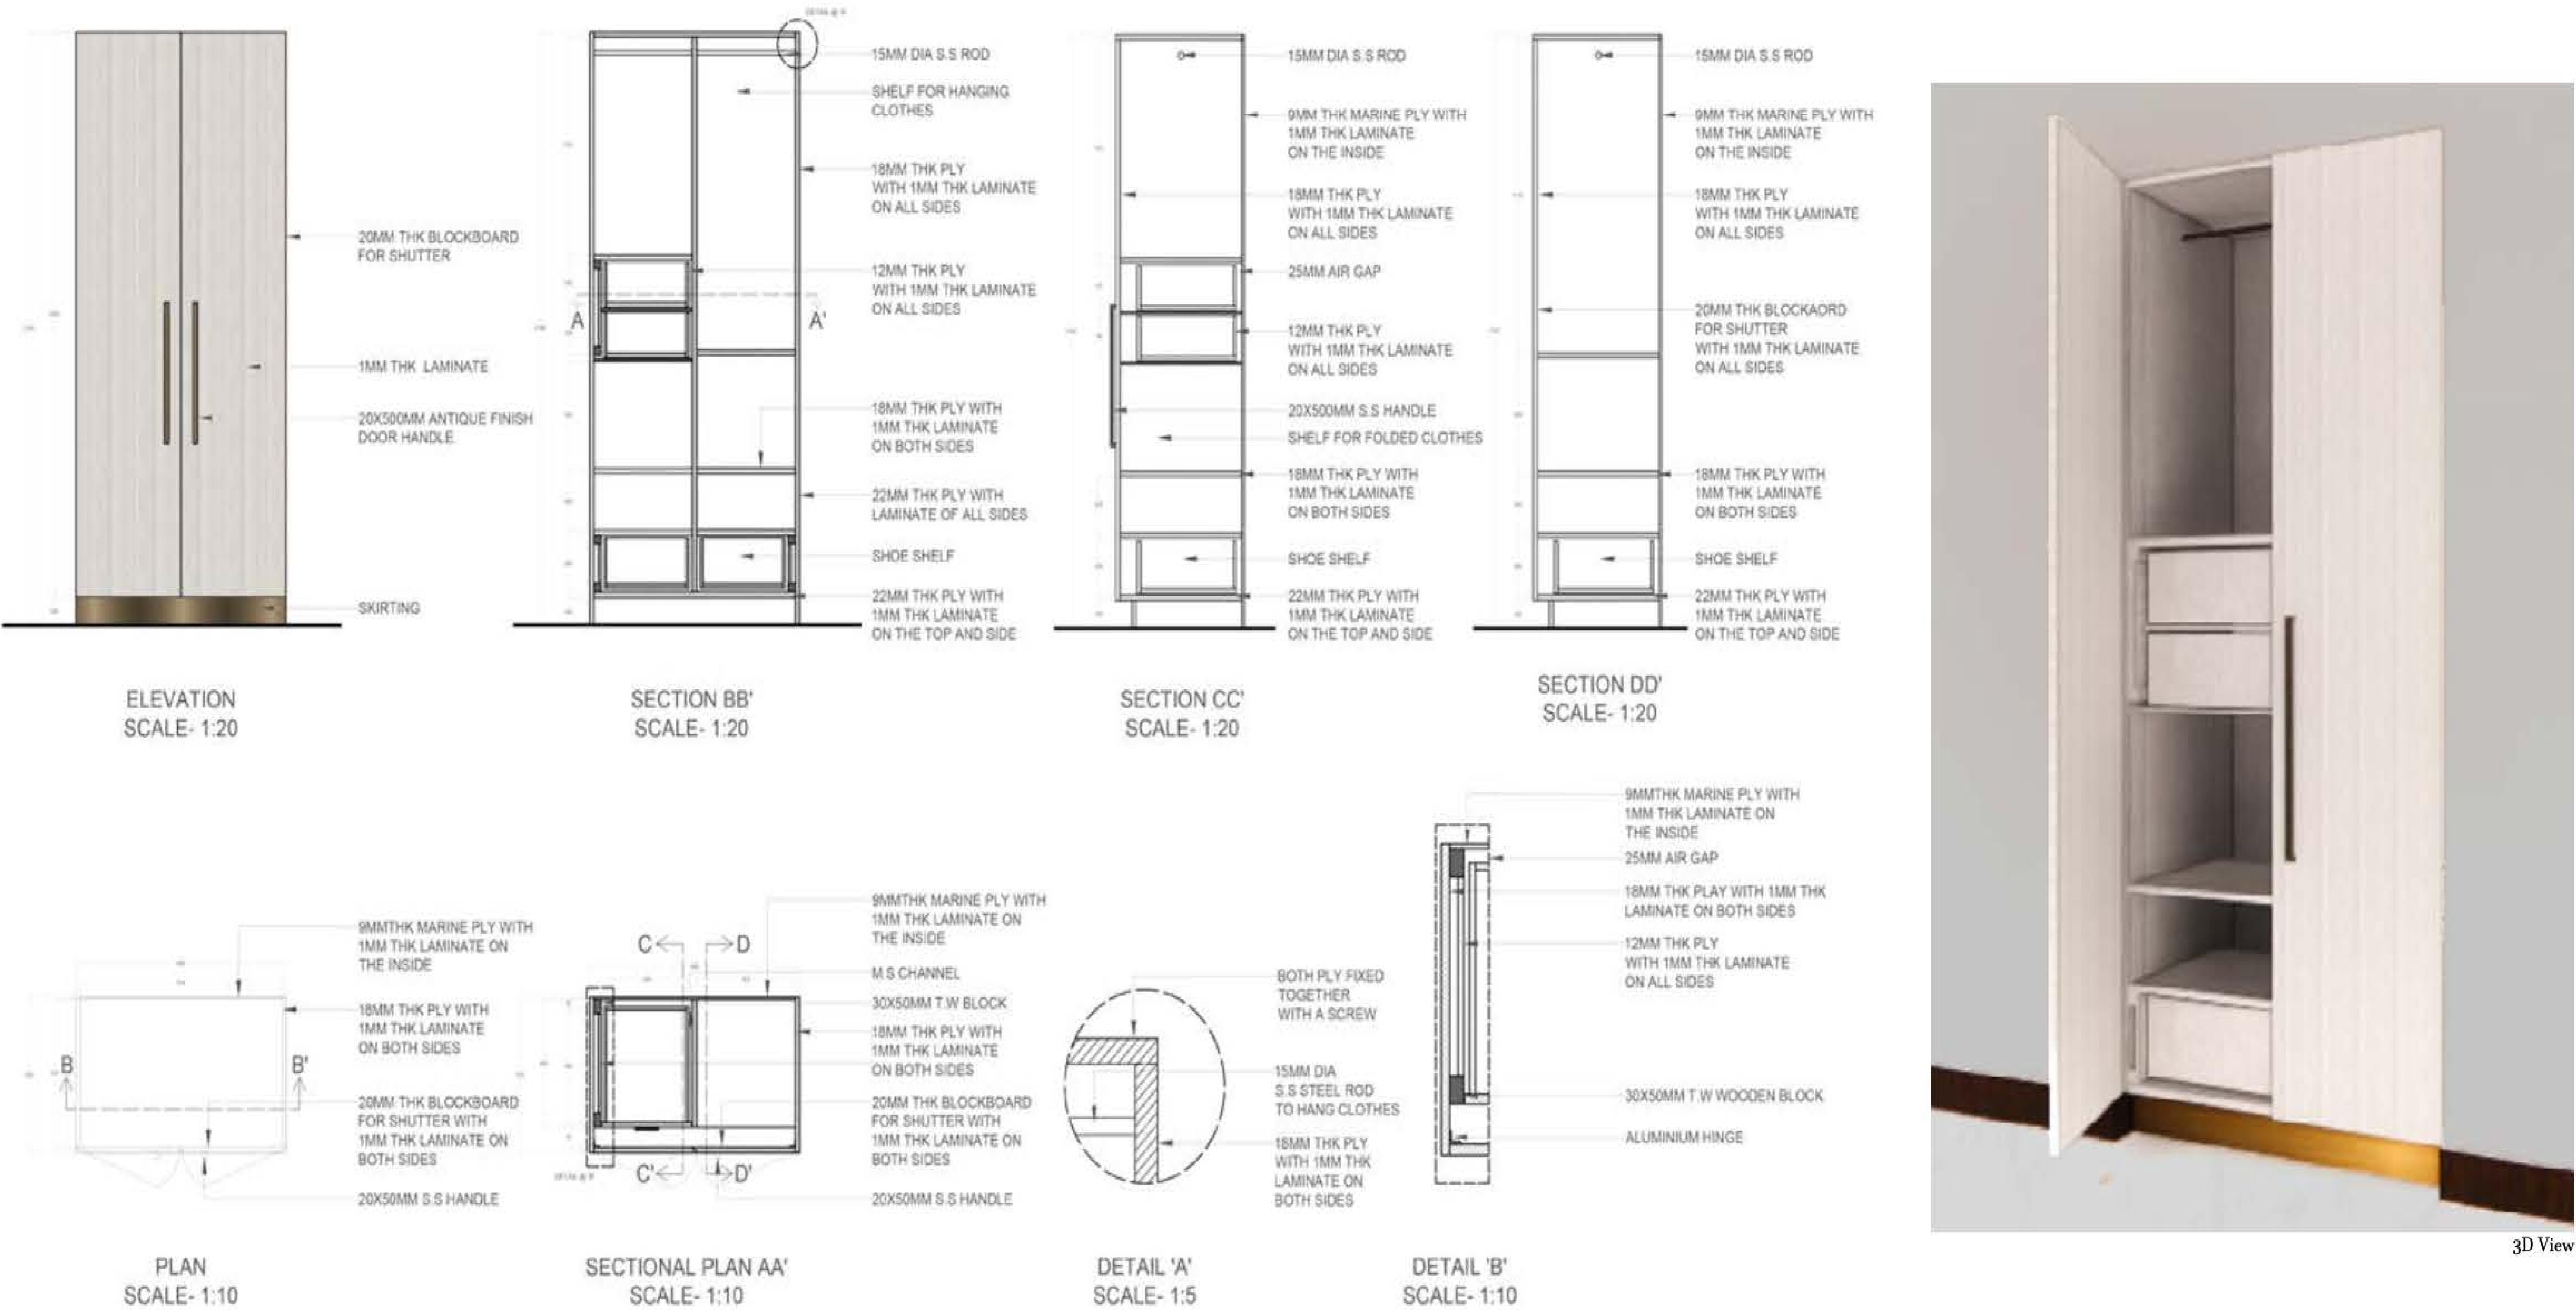

T H A N K  
Y O U